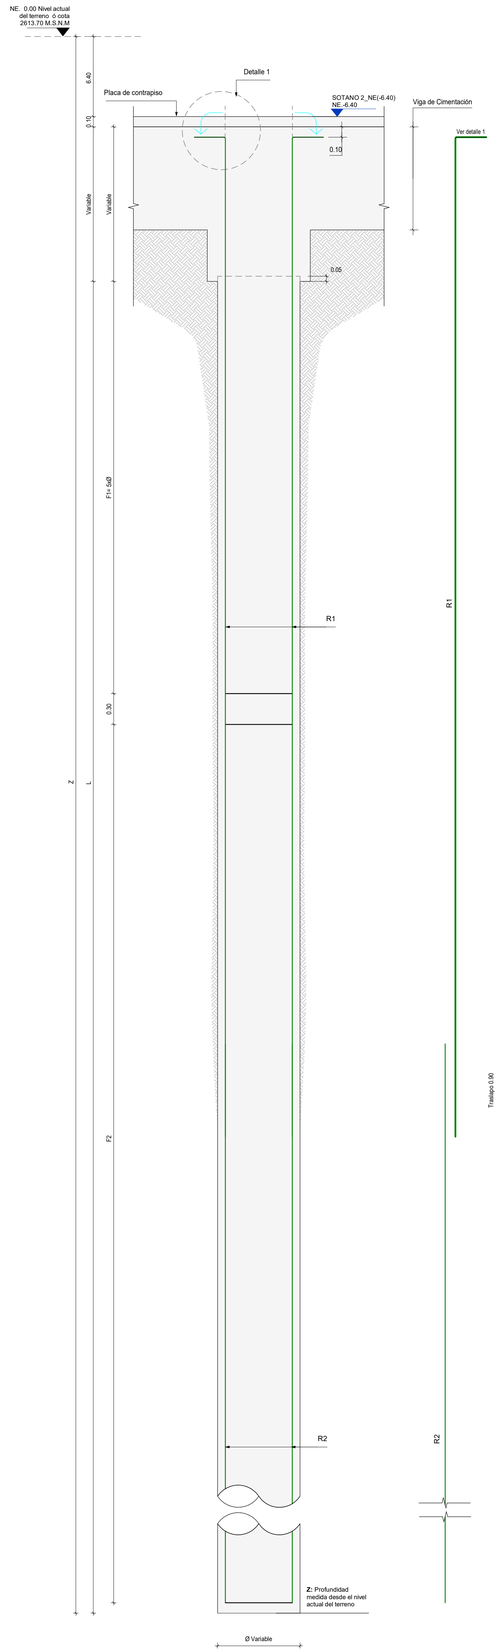

PILOTE TIPO 1, 2, 3 Y 4
Escala 1 : 25

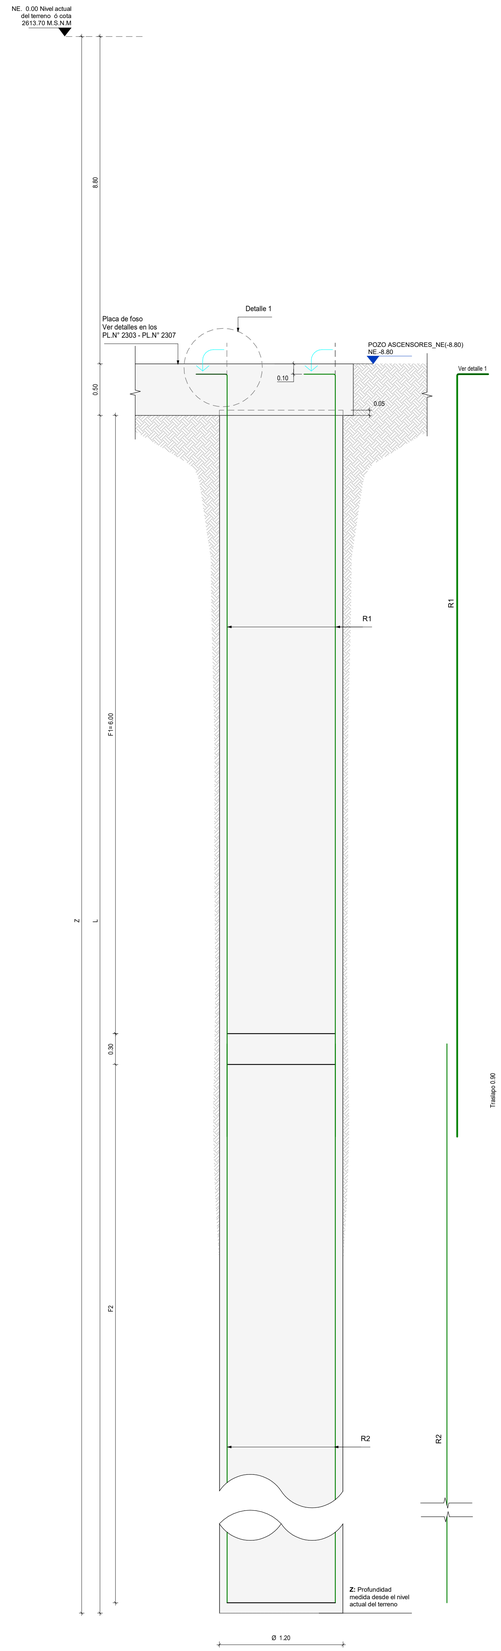

PILOTE TIPO 5
Escala 1 : 25

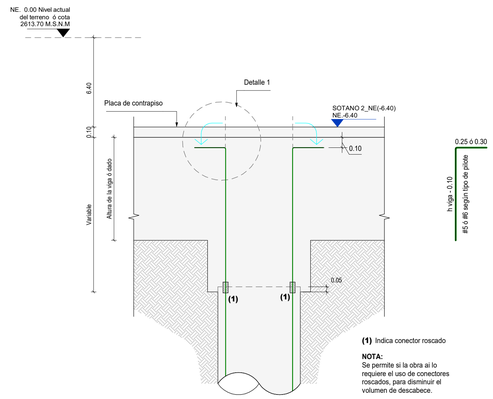

(1) Indica conector roscado

NOTA:
Se permite si la obra ai lo requiere el uso de conectores roscados, para disminuir el volumen de descabece.

DETALLE OPCIÓN 2
Escala 1 : 25

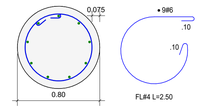

SECCIÓN PILOTE Ø 0.80
Escala 1 : 25

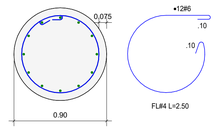

SECCIÓN PILOTE Ø 0.90
Escala 1 : 25

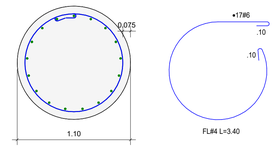

SECCIÓN PILOTE Ø 1.10
Escala 1 : 25

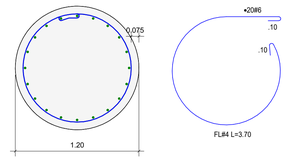

SECCIÓN PILOTE Ø 1.20
Escala 1 : 25

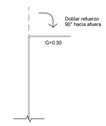

DETALLE 1
Escala 1 : 25

CUADRO REFUERZO DE PILOTES

VC: Volumen de concreto pilotes
Se calcula con la longitud "L" que se indica en el corte tipico.

WRL: Peso Refuerzo Longitudinal
WRT: Peso Refuerzo Transversal

NOTA: Estas cantidades no incluyen desperdicios

No Pilote	Tipo	Recuento	Z (m)	L	Refuerzo Longitudinal				Refuerzo Transversal								Resumen			Material
									Tramo F1				Tramo F2				Vc (m3)	W/RL (Kg)	W/RT (Kg)	
					Cant. Ref	# Barra	R1 (m)	R2 (m)	Cant. Ref	# Barra	Separación	Long. (m)	Cant. Ref	# Barra	Separación	Long. (m)				
1	S=0.80	97	27.50	21.00	9	# 6	10.00	12.00	55	#4	c/0.075	2.50	57	#4	c/0.30	2.50	948.65 m³	43606	27160	CONCRETO f'c=28 MPa-4000Psi
2	S=0.90	23	27.50	21.00	12	# 6	10.00	12.00	61	#4	c/0.075	2.80	55	#4	c/0.30	2.80	277.75 m³	13786	7470	CONCRETO f'c=28 MPa-4000Psi
3	S=1.10	12	27.50	21.00	17	# 6	10.00	12.00	75	#4	c/0.075	3.40	52	#4	c/0.30	3.40	217.44 m³	10190	5182	CONCRETO f'c=28 MPa-4000Psi
4	S=1.20	24	27.50	21.00	20	# 6	10.00	12.00	81	#4	c/0.075	3.70	50	#4	c/0.30	3.70	514.59 m³	23976	11633	CONCRETO f'c=28 MPa-4000Psi
5	S=1.20	2	27.50	18.70	20	# 6	7.70	12.00	81	#4	c/0.075	3.70	50	#4	c/0.30	3.70	41.17 m³	1998	969	CONCRETO f'c=28 MPa-4000Psi
Dado	S=100x100x150	1	8.00														1.36 m³	0	0	CONCRETO f'c=42 MPa-6000Psi
TOTAL		159															2000.95 m³	93556	52414	

NOTA:

La longitud ó profundidad del pilote deberá ser revisada y aprobada en obra por el Ingeniero de Suelos para garantizar que la capacidad del elemento sea la establecida en el estudio de suelos.

VºBº INGENIERO DE SUELOS

CONCRETO

f'c=28 MPa
f'c=280 kg/cm²
f'c=4000 psi

NOTAS

1. Ver detalles generales en el PL.N° 2002
2. Ver planta de localización de pilotes en el PL. N° 2100

EST - 2101-PD-P1
VERSIÓN PLANO V-01
OBRA No. 1157

CONSTRUCCIONES PLANIFICADAS
Carrera 13 No. 26A - 47 Piso 2
PBX: 339 41 11 Fax: 287 02 16

Robledales
RESERVADO

CONTIENE:

NOMBRE DEL PROYECTO
ROBLEDALES-TORRE PALMERI 1

Dirección AK 7 134 06

DETALLES Y CUADRO DE PILOTES

ESCALA: INDICADA

ARCHIVO: 1157-EST-2101-PD-P1-DETALLES Y CUADRO DE PILOTES.DWG

FECHA:	DIBUJADO POR:
12/02/2026	ANDRES DUARTE

DISEÑADOR ESTRUCTURAL
ROBERTO AYCARDI FONSECA
TP: 2520257258 CND

DISEÑADOR DE ELMENTOS NO ESTRUCTURALES
VICTOR H. DÁVILA F.
TP: 2520122782 CND

REVISOR ESTRUCTURAL
NICOLAS PARRA GARCIA
TP: 25202-62063 CND

CONSTRUCTOR RESPONSABLE
ALVARO DÍAZ ULLOA
TP: 2520275046 CND

CONSTRUCCIONES PLANIFICADAS

GERENTE DE DISEÑO

DIRECTOR DE ARQUITECTURA
ANDRÉS VALCARCEL

DIRECTOR DE INGENIERÍA
MARIO FERNANDO RIVERA

DIRECTOR DE PRESUPUESTOS
JAVIER CLAVIJO

EQUIPO DISEÑO CPSA
MP, CO, LL, EC.

MODIFICACIONES

#	Fecha	Emitida por	Modificación

VERSIONES DE PLANOS

Versión	Fecha
V-01	12/02/2026

PROPÓSITO DE LA EMISIÓN

DRAFT	
Coordinación Técnica	
Revisión	
Construcción	✖
Curaduría	
Presupuestos	

MODELO FUENTE:	VERSIÓN MODELO:
1157_ROBL-BOG_VIV_ESTR_TP1 17/03/2026	FASE III / V-03

EST - 2101-PD-P1
VERSIÓN PLANO V-01
OBRA No. 1157