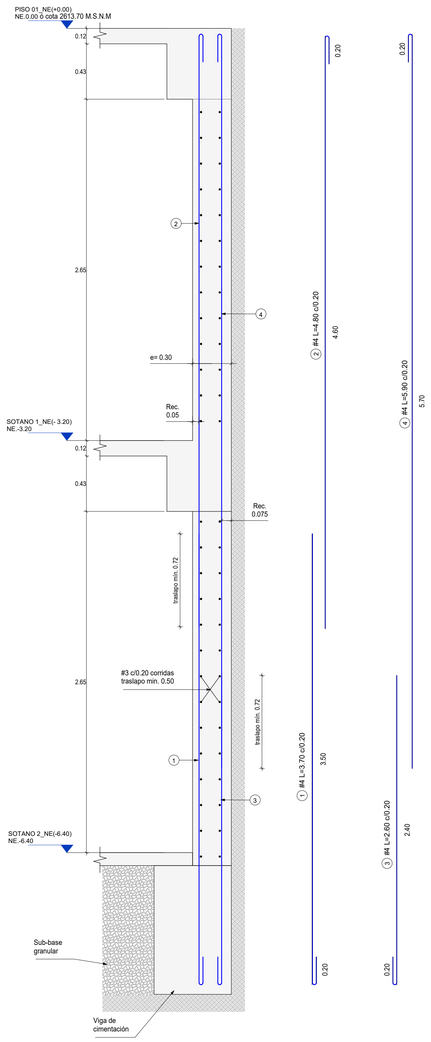

DETALLE MURO MC-1
Escala 1 : 20

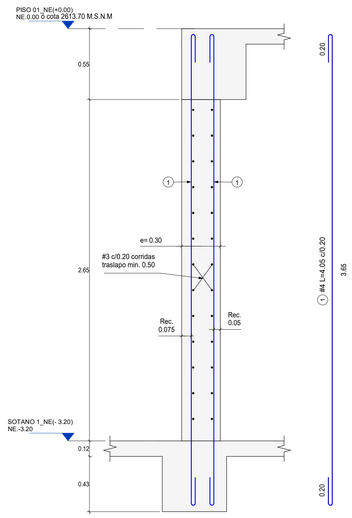

DETALLE MURO MC-2
Escala 1 : 20

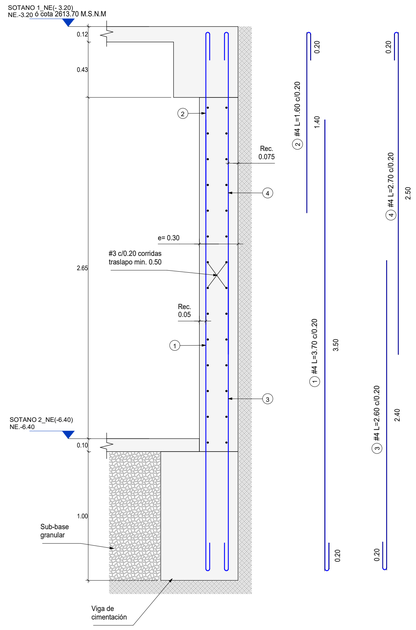

DETALLE MURO MC-3
Escala 1 : 20

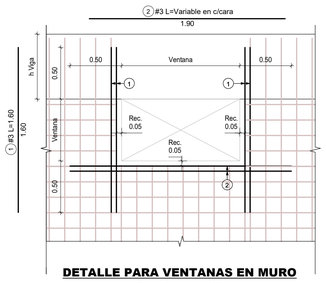

DETALLE PARA VENTANAS EN MURO
Escala 1 : 25

CONCRETO
f'c=35 MPa **f'c=350 kg/cm²** **f'c=5000 psi**
NOTAS
1. Ver detalles generales en el PL.N° 2002 2. Ver planta de localización de columnas y muros en el PL.N° 2200

EST - 2220-PD-P1
VERSIÓN PLANO V-01
OBRA No. 1157

CONSTRUCCIONES PLANIFICADAS
Carrera 13 No. 26A - 47 Piso 2
PBX: 339 41 11 Fax: 287 62 16

Robledales RESERVADO

CONTIENE:

NOMBRE DEL PROYECTO
ROBLEDALES-TORRE PALMERI 1

Dirección AK 7 134 06

DESPIECE DE MUROS DE CONTENCIÓN

ESCALA: INDICADA

ARCHIVO: EST-2220-PD-P1-DESPIECE DE MUROS DE CONTENCIÓN.DWG

FECHA:	DIBUJADO POR:
12/02/2026	ANDRES DUARTE

DISEÑADOR ESTRUCTURAL
ROBERTO AYCARDI FONSECA
TP: 2520257258 CND

DISEÑADOR DE ELMENTOS NO ESTRUCTURALES
VICTOR H. DÁVILA F.
TP: 2520122782 CND

REVISOR ESTRUCTURAL
NICOLAS PARRA GARCIA
TP: 25202-62063 CND

CONSTRUCTOR RESPONSABLE
ALVARO DÍAZ ULLOA
TP: 2520275046 CND

CONSTRUCCIONES PLANIFICADAS

GERENTE DE DISEÑO

DIRECTOR DE ARQUITECTURA
ANDRÉS VALCARCEL

DIRECTOR DE INGENIERÍA
MARIO FERNANDO RIVERA

DIRECTOR DE PRESUPUESTOS
JAVIER CLAVIJO

EQUIPO DISEÑO CPSA
MP, CO, LL, EC.

MODIFICACIONES

#	Fecha	Emitida por	Modificación

VERSIONES DE PLANOS

Versión	Fecha
V-01	12/02/2026

PROPÓSITO DE LA EMISIÓN

DRAFT	
Coordinación Técnica	
Revisión	
Construcción	✖
Curaduría	
Presupuestos	

MODELO FUENTE: 1157_ROBL-BOG_VIV_ESTR_TP1
17/03/2026

VERSIÓN MODELO: FASE III / V-03

EST - 2220-PD-P1
VERSIÓN PLANO V-01
OBRA No. 1157