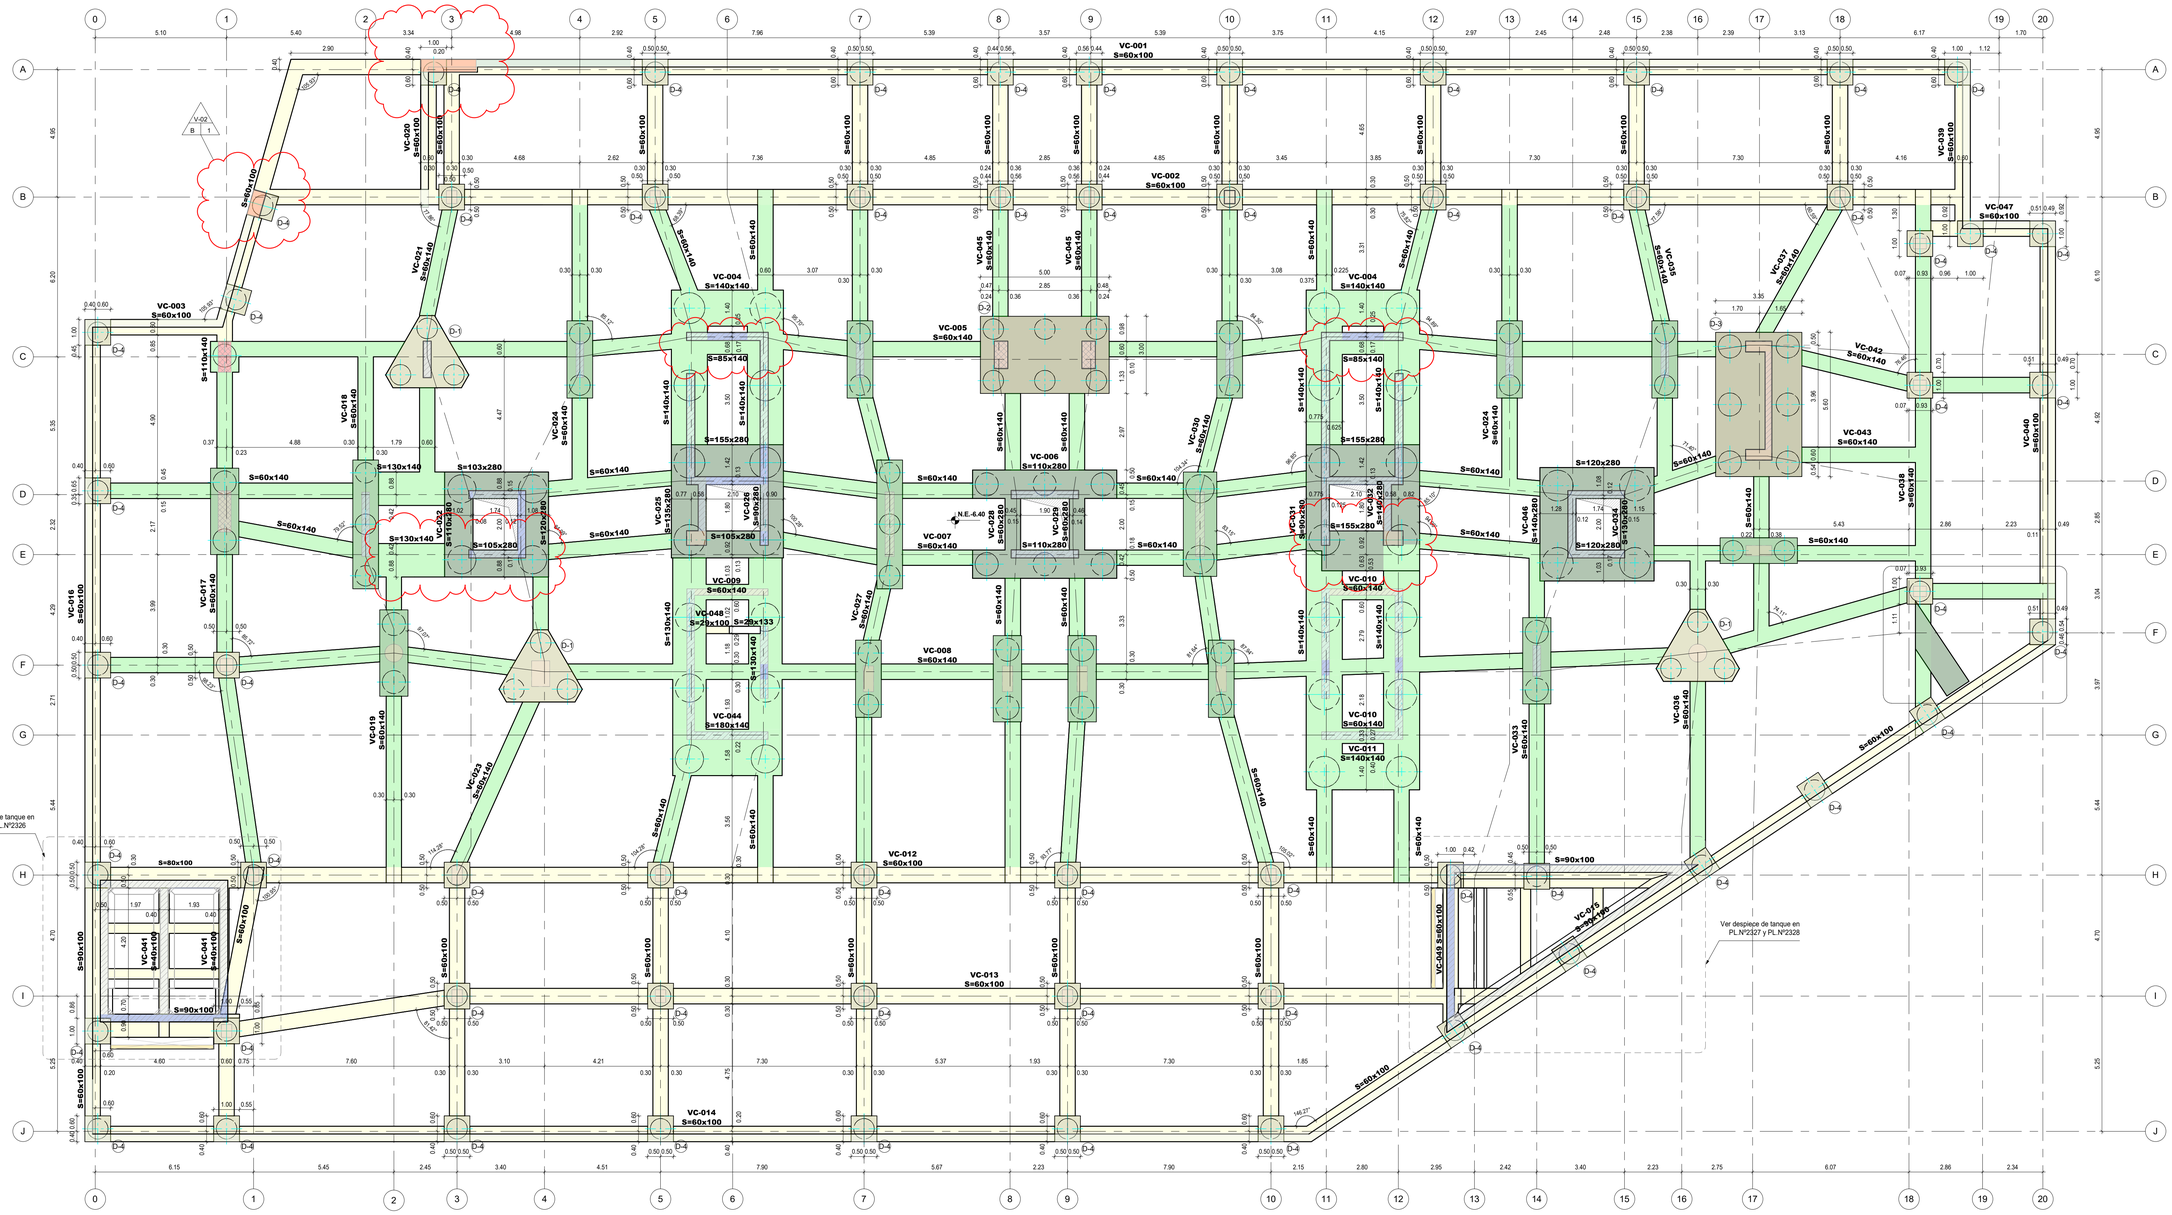

PLANTA DE CIMENTACIÓN NE(-6.40)
Escala 1 : 100

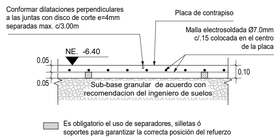

DETALLE JUNTA DE CONTRACCIÓN
Escala 1 : 20

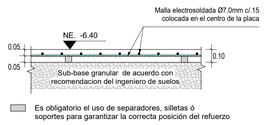

CORTE TÍPICO PLACA DE CONTRAPISO
Escala 1 : 20

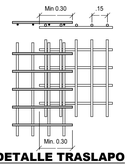

DETALLE TRASLAPO DE MALLAS
Escala 1 : 25

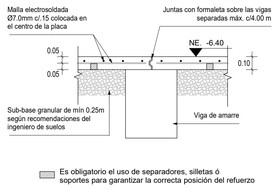

DETALLE JUNTA DE CONSTRUCCIÓN
Escala 1 : 20

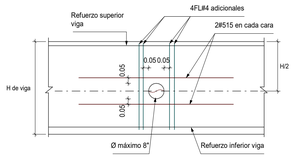

DETALLE PASE EN VIGAS DE CIMENTACIÓN
Escala 1 : 25

CONCRETO
f'c=42 MPa
f'c=420 kg/cm²
f'c=6000 psi

CONVENCIONES

- Indica muros e=0.25m
- Indica muros e=0.30m
- Indica muros e=0.35m
- Indica muros e=0.50m
- Indica columnas
- Indica muros de contención
- Indica vigas de cimentación
- VC-000 Indica N° de viga
- D-# Indica N° de dado

NOTAS

1. Ver detalles generales en el PL.N° 2002
2. Ver detalle de dados en los PL. N° 2301 y PL. N° 2302
3. Ver despieces de vigas en los PL.N° 2303 - PL.N° 2307

NOTA:
Este plano debe ser revisado y aprobado por el Ingeniero de suelos.

V°B° INGENIERO DE SUELOS

EST - 2300-PP-P1
VERSIÓN PLANO V-02
OBRA No. 1157

CONSTRUCCIONES PLANIFICADAS
Carrera 13 No. 26A - 47 Piso 2
PBX: 339 41 11 Fax: 287 62 16

Robledales RESERVADO

CONTIENE:

NOMBRE DEL PROYECTO
ROBLEDALES-TORRE PALMERI 1

Dirección AK 7 134 06

PLANTA DE CIMENTACIÓN

ESCALA: INDICADA

ARCHIVO:	1157-EST-2300-PP-P1-PLANTA DE CIMENTACIÓN.DWG
FECHA: 11/03/2026	DIBUJADO POR: ANDRES DUARTE

DISEÑADOR ESTRUCTURAL
ROBERTO AYCARDI FONSECA
TP: 2520257258 CND

DISEÑADOR DE ELMENTOS NO ESTRUCTURALES
VICTOR H. DÁVILA F.
TP: 2520122782 CND

REVISOR ESTRUCTURAL
NICOLAS PARRA GARCIA
TP: 25202-62063 CND

CONSTRUCTOR RESPONSABLE
ALVARO DÍAZ ULLOA
TP: 2520275046 CND

CONSTRUCCIONES PLANIFICADAS
GERENTE DE DISEÑO
DIRECTOR DE ARQUITECTURA
ANDRÉS VALCARCEL
DIRECTOR DE INGENIERÍA
MARIO FERNANDO RIVERA
DIRECTOR DE PRESUPUESTOS
JAVIER CLAVIJO

EQUIPO DISEÑO CPSA
MP, CO, LL, EC.

MODIFICACIONES

#	Fecha	Emitida por	Modificación
1	11/03/2026	B	se incluyen columnas para manejo de voladizo y se ajustan secciones de vigas.

VERSIONES DE PLANOS

Versión	Fecha
V-01	20/02/2026
V-02	11/03/2026

PROPÓSITO DE LA EMISIÓN

DRAFT	
Coordinación Técnica	
Revisión	
Construcción	✖
Curaduría	
Presupuestos	

MODELO FUENTE: 1157_ROBL-BOG_VIV_ESTR_TP1 17/03/2026	VERSIÓN MODELO: FASE III / V-03

EST - 2300-PP-P1
VERSIÓN PLANO V-02
OBRA No. 1157