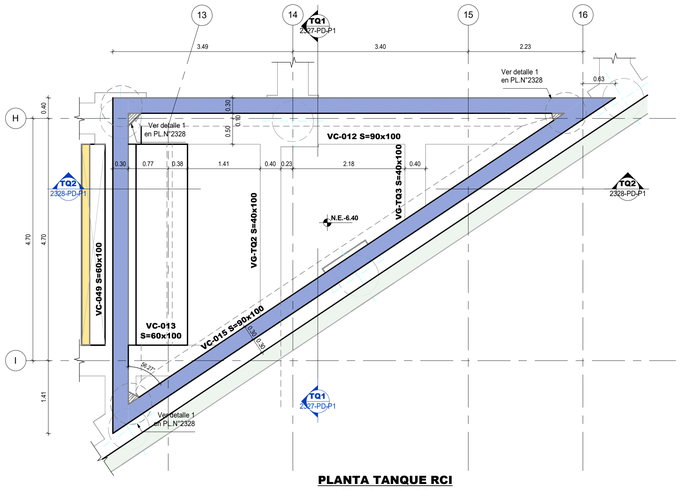

PLANTA TANQUE RCI
Escala 1 : 50

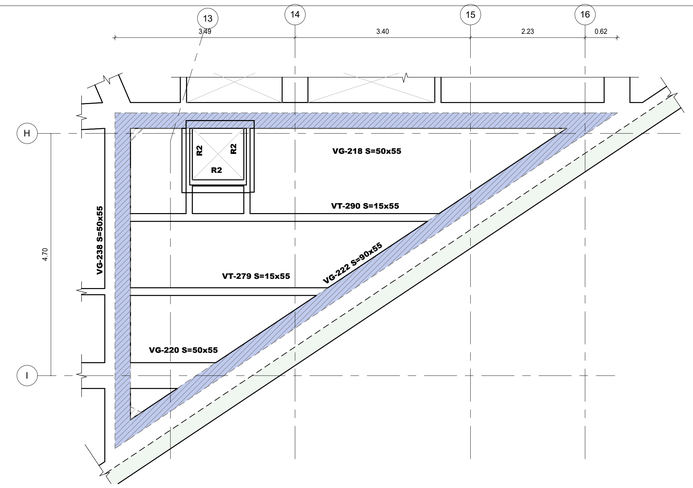

PLANTA TAPA DE TANQUE RCI
Escala 1 : 50

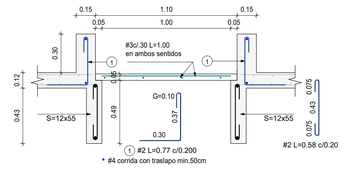

DETALLE TAPA DE TANQUE RCI
Escala 1 : 20

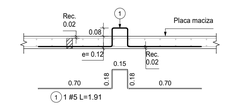

NOTAS:

1. Capacidad de gancho 3 T.
2. La varilla para gancho de linea de vida debe estar posicionada en la malla inferior de la placa
3. Las varillas expuestas para ganchos se deben protegen contra la corrosión con éposxico según proveedores especializados.

DETALLE DE GANCHO PARA LINEA DE VIDA
Escala 1 : 25

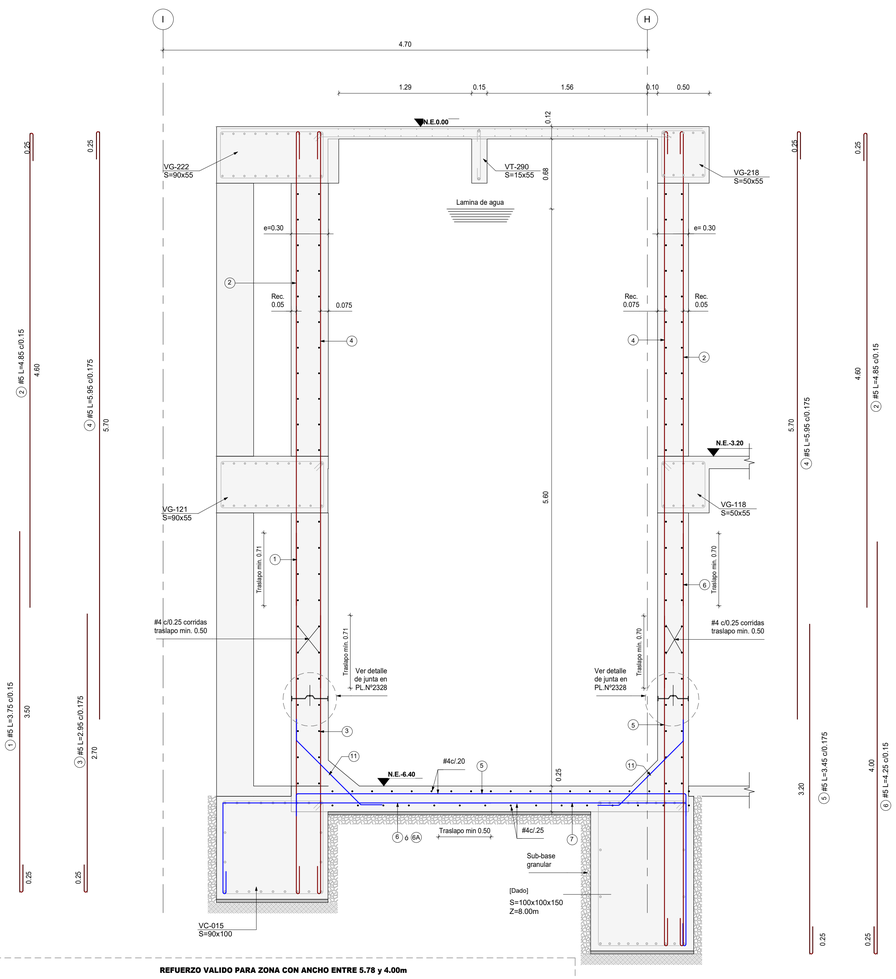

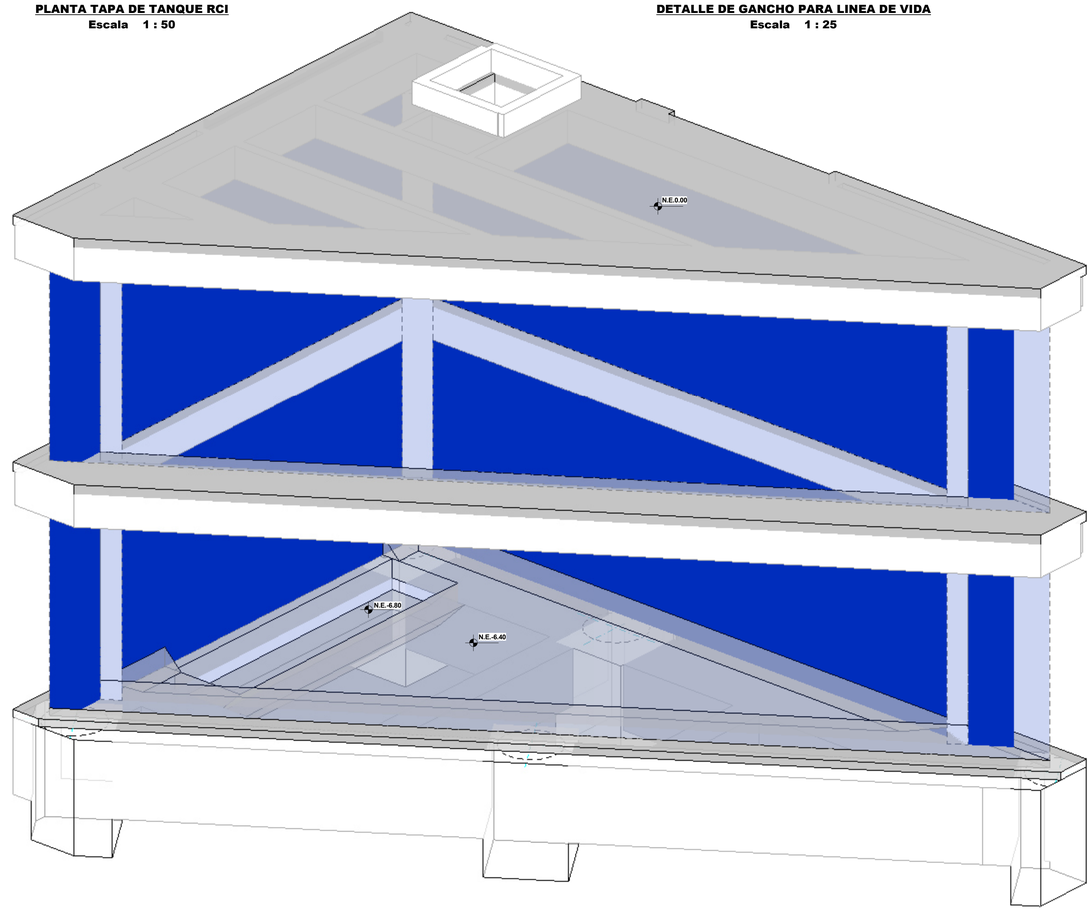

ESQUEMA 3D TANQUE RCI
Sin escala

REFUERZO VALIDO PARA ZONA CON ANCHO ENTRE 5.78 y 4.00m

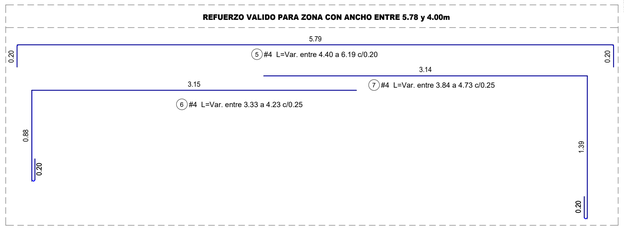

REFUERZO VALIDO PARA ZONA CON ANCHO ENTRE 4.00m y 1.40m

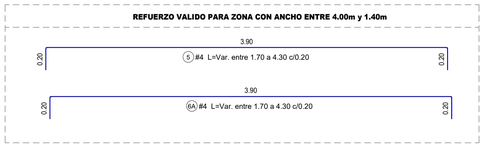

CORTE TANQUE RCI TQ1 - TQ1
Escala 1 : 25

CONCRETO

- **f'c=4000 Psi**
- **f'c=28 MPa**
- Relación A/C=<0.50
- Curado intensivo por lo menos durante 15 dias.

CONVENCIONES

- Indica muros tanque e=0.30m
- Indica muros de contención

NOTAS

1. Ver detalles generales en el PL.N° 2002
2. Ver planta de cimentación en el PL.N° 2300
3. Ver corte TQ2-TQ2 en el PL.N° 2328
4. Ver despieces de vigas TQ RCI en el PL.N° 2328

NOTA:
Este plano debe ser revisado y aprobado por el Ingeniero de suelos.

VºBº INGENIERO DE SUELOS

EST - 2327-PD-P1
VERSIÓN PLANO V-01
OBRA No. 1157

CONSTRUCCIONES PLANIFICADAS
Carrera 13 No. 26A - 47 Piso 2
PBX: 339 41 11 Fax: 287 62 16

Robledales RESERVADO

CONTIENE:

NOMBRE DEL PROYECTO
ROBLEDALES-TORRE PALMERI 1

Dirección AK 7 134 06

DESPIECE DE TANQUE 2

ESCALA: INDICADA

ARCHIVO: 1157-EST-2327-PD-P1-DESPIECE DE TANQUE 2.DWG
FECHA: 20/02/2026
DIBUJADO POR: KAREN CASTILLO

DISEÑADOR ESTRUCTURAL
ROBERTO AYCARDI FONSECA
TP: 2520257258 CND

DISEÑADOR DE ELMENTOS NO ESTRUCTURALES
VICTOR H. DÁVILA F.
TP: 2520122782 CND

REVISOR ESTRUCTURAL
NICOLAS PARRA GARCIA
TP: 25202-62063 CND

CONSTRUCTOR RESPONSABLE
ALVARO DÍAZ ULLOA
TP: 2520275046 CND

CONSTRUCCIONES PLANIFICADAS

GERENTE DE DISEÑO

DIRECTOR DE ARQUITECTURA
ANDRÉS VALCARCEL

DIRECTOR DE INGENIERÍA
MARIO FERNANDO RIVERA

DIRECTOR DE PRESUPUESTOS
JAVIER CLAVIJO

EQUIPO DISEÑO CPSA
MP, CO, LL, EC.

MODIFICACIONES

#	Fecha	Emitida por	Modificación

VERSIONES DE PLANOS

Versión	Fecha
V-01	20-02-2026

PROPÓSITO DE LA EMISIÓN

DRAFT	
Coordinación Técnica	
Revisión	
Construcción	X
Curaduría	
Presupuestos	

MODELO FUENTE: 1157_ROBL-BOG_VIV_ESTR_TP1
17/03/2026
VERSIÓN MODELO: FASE III / V-03

EST - 2327-PD-P1
VERSIÓN PLANO V-01
OBRA No. 1157