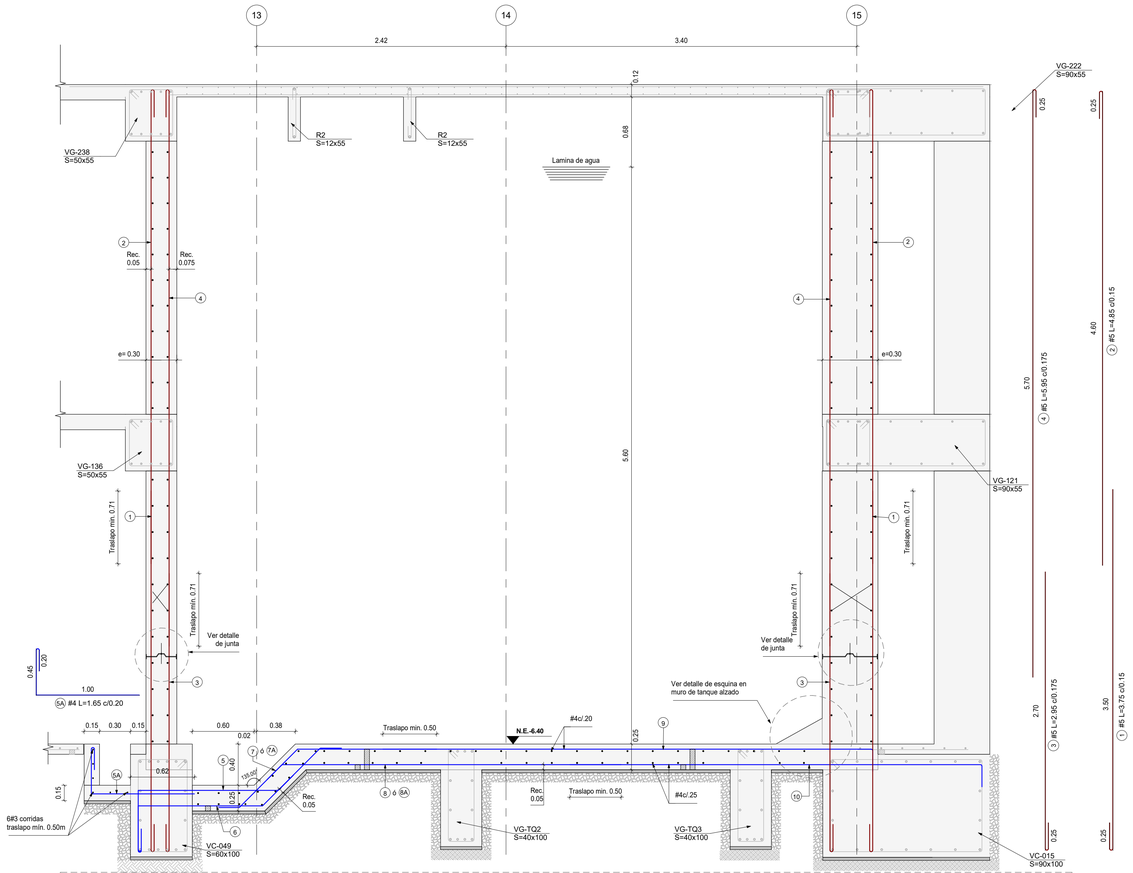

REFUERZO VALIDO PARA ZONA CON ANCHO ENTRE 5.78 y 3.20m

REFUERZO VALIDO PARA ZONA CON ANCHO ENTRE 3.10 y 1.00m

CORTE TANQUE RCI TQ2 - TQ2

Escala 1 : 25

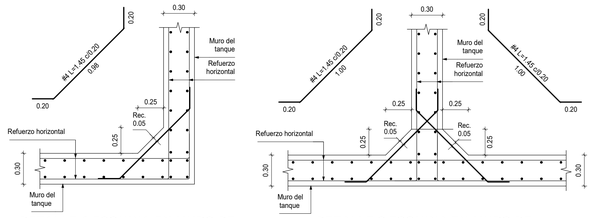

DETALLE 1 ESQUINA EN MURO DE TANQUE (PLANTA)

Escala 1 : 25

DETALLE 2 ESQUINA EN MURO DE TANQUE (PLANTA)

Escala 1 : 25

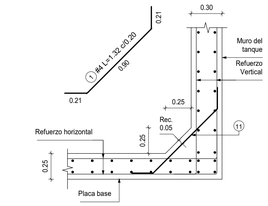

DETALLE ESQUINA EN MURO DE TANQUE (ALZADO) e= 0.30m

Escala 1 : 25

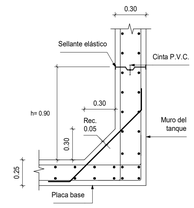

DETALLE DE JUNTA (ALZADO)

Escala 1 : 25

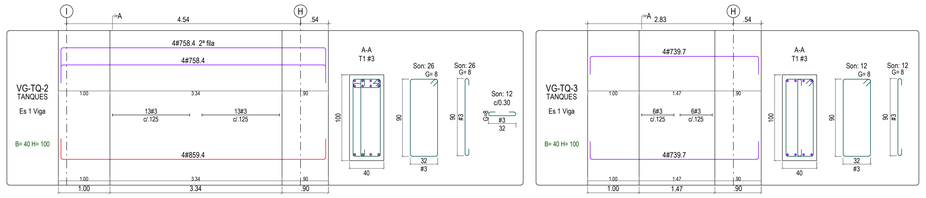

CONCRETO
• **f'c=4000 Psi**
• **f'c=28 MPa**
• Relación A/C=<0.50
• Curado intensivo por lo menos durante 15 días.

CONVENCIONES

- Indica muros tanque e=0.30m
- Indica muros de contención

NOTAS

1. Ver detalles generales en el PL.N° 2002
2. Ver planta de cimentación en el PL.N° 2300
3. Ver planta de tanque RCI en el PL.N° 2327
4. Ver corte TQ1-TQ1 en el PL.N° 2327

EST - 2328-PD-P1

VERSIÓN PLANO V-01

OBRA No. 1157

CONSTRUCCIONES PLANIFICADAS
Carrera 13 No. 26A - 47 Piso 2
PBX: 339 41 11 Fax: 287 02 16

Robledales RESERVADO

CONTIENE:

NOMBRE DEL PROYECTO
ROBLEDALES-TORRE PALMERI 1

Dirección AK 7 134 06

DESPIECE DE TANQUE 2

ESCALA: INDICADA

ARCHIVO: 1157-EST-2328-PD-P1-DESPIECE DE TANQUE 2.DWG

FECHA:	DIBUJADO POR:
20/02/2026	KAREN CASTILLO

DISEÑADOR ESTRUCTURAL
ROBERTO AYCARDI FONSECA
TP: 2520257258 CND

DISEÑADOR DE ELMENTOS NO ESTRUCTURALES
VICTOR H. DÁVILA F.
TP: 2520212278 2 CND

REVISOR ESTRUCTURAL
NICOLAS PARRA GARCIA
TP: 25202-62063 CND

CONSTRUCTOR RESPONSABLE
ALVARO DÍAZ ULLOA
TP: 2520275046 CND

CONSTRUCCIONES PLANIFICADAS
GERENTE DE DISEÑO
DIRECTOR DE ARQUITECTURA
ANDRÉS VALCARCEL
DIRECTOR DE INGENIERÍA
MARIO FERNANDO RIVERA
DIRECTOR DE PRESUPUESTOS
JAVIER CLAVIJO

EQUIPO DISEÑO CPSA
MP, CO, LL, EC.

MODIFICACIONES

#	Fecha	Emitida por	Modificación

VERSIONES DE PLANOS

Versión	Fecha
V-01	20-02-2026

PROPÓSITO DE LA EMISIÓN

DRAFT	
Coordinación Técnica	
Revisión	
Construcción	✖
Curaduría	
Presupuestos	

MODELO FUENTE: 1157_ROBL-BOG_VIV_ESTR_TP1
17/03/2026

VERSIÓN MODELO: FASE III / V-03

EST - 2328-PD-P1
VERSIÓN PLANO V-01
OBRA No. 1157