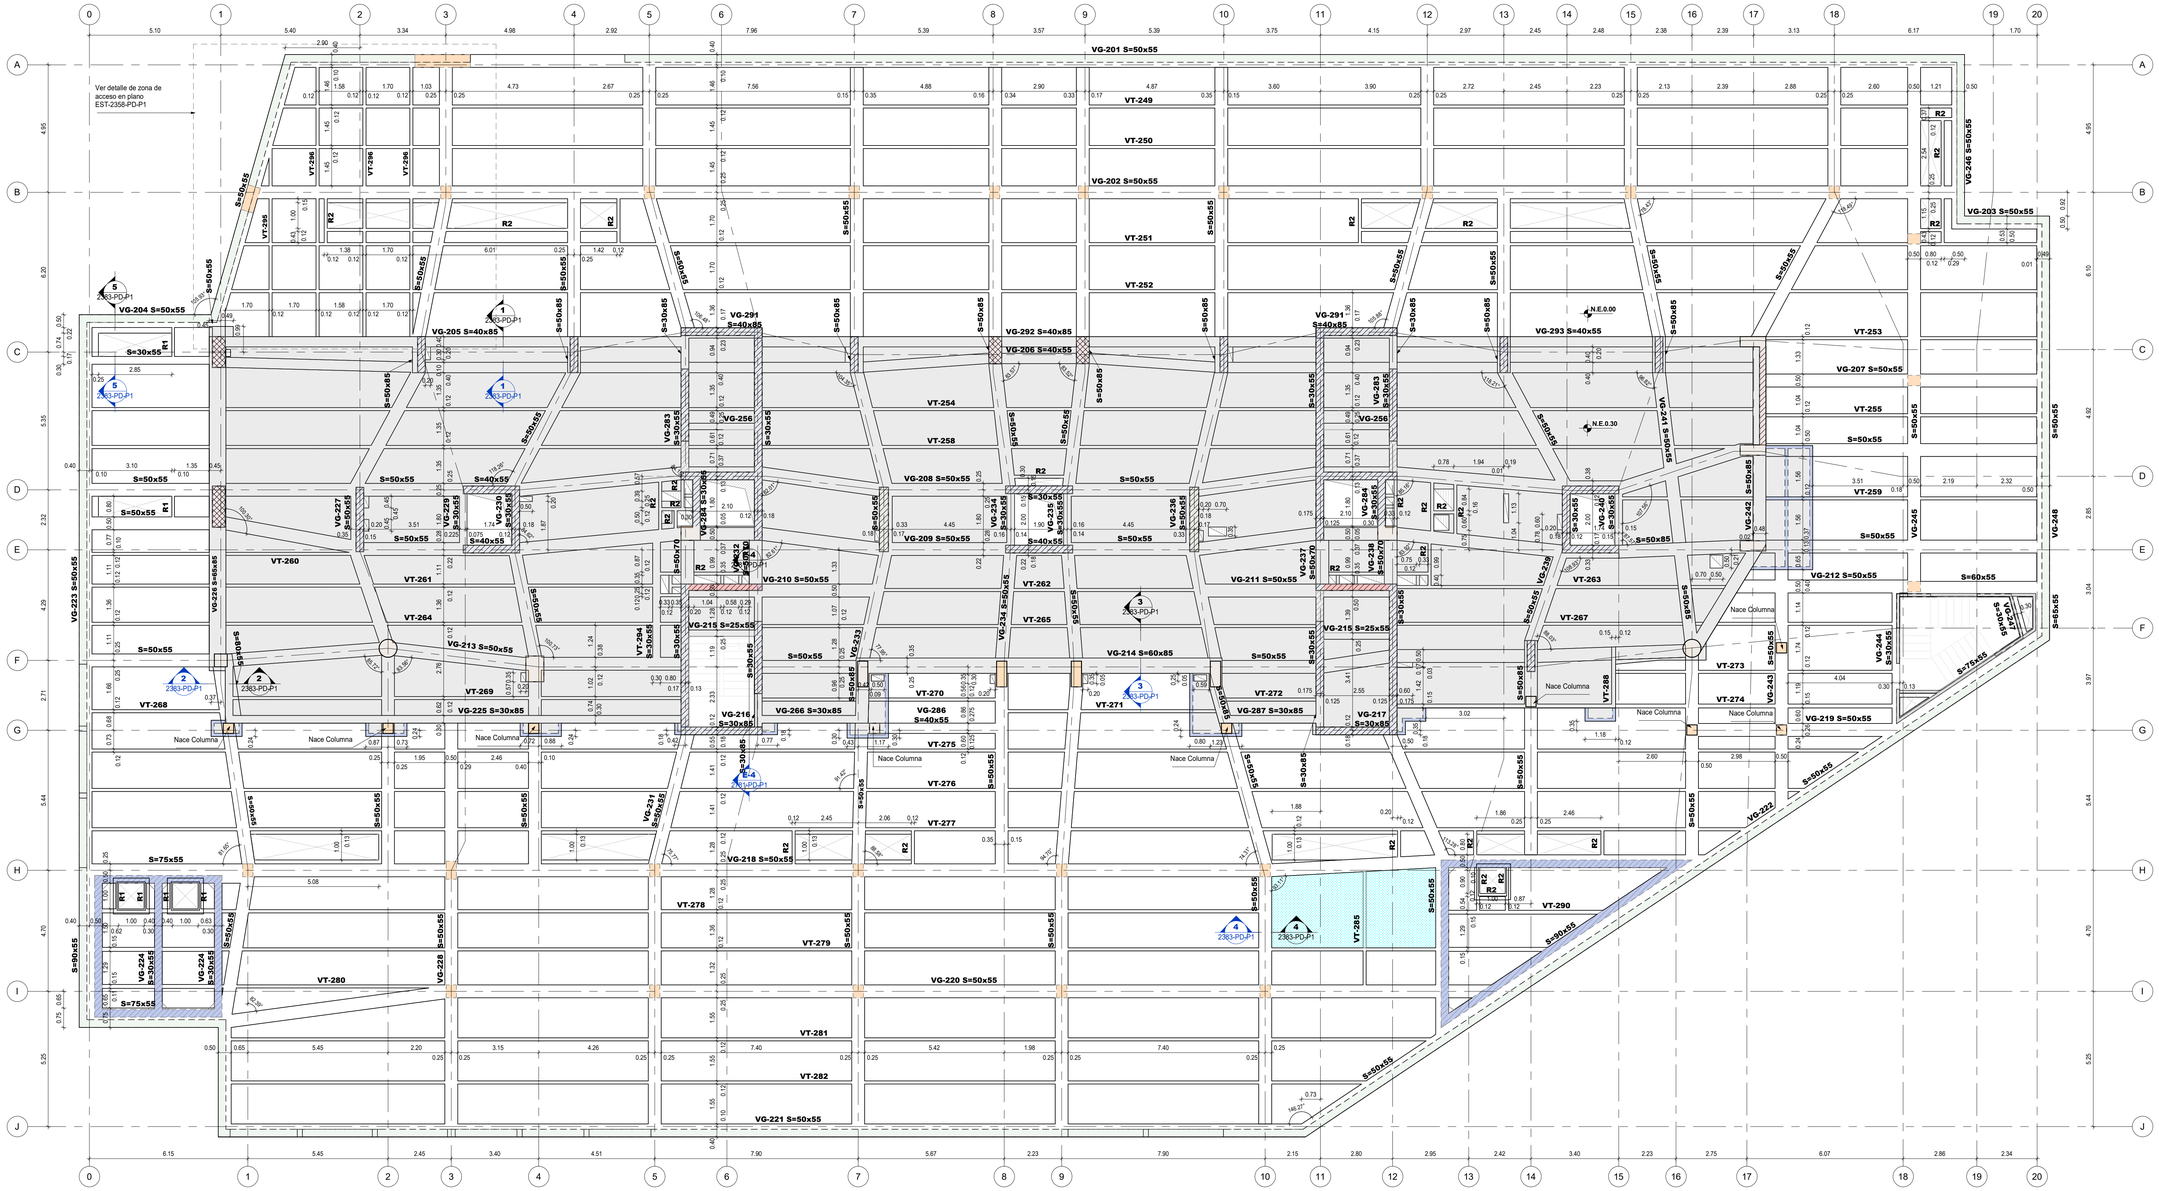

PLANTA DE PISO 01_NE(+0.00)
Escala 1 : 100

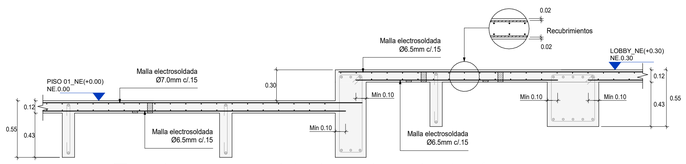

Es obligatorio el uso de separadores, silletas ó soportes para garantizar la correcta posición del refuerzo.
Losa NE 0.00, se debe garantizar un tiempo mínimo de curado intensivo de por lo menos 15 días.

CORTE TÍPICO DE PLACA e=0.12
Escala 1 : 25

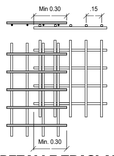

DETALLE TRASLAPO DE MALLAS
Escala 1 : 25

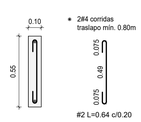

RIOSTRA 10X55 (R1)
Escala 1 : 20

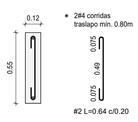

RIOSTRA 12X55 (R2)
Escala 1 : 20

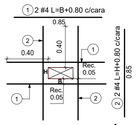

DETALLE DE VACÍOS
Escala 1 : 25

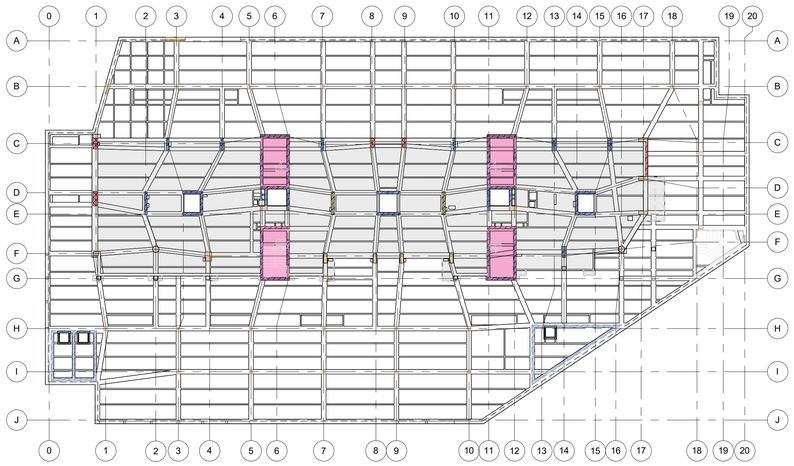

PLANTA DE PISO 01_NE(+0.00)-CARGAS VIVAS
Sin escala

CONVENCIONES CARGA VIVA

- Indica carga viva 500 Kg/m²
- Indica carga viva 300 Kg/m²
- Indica carga viva 500 Kg/m²

CONCRETO

f'c=42 MPa
f'c=420 kg/cm²
f'c=6000 psi

CONVENCIONES

- Indica muros e=0.25m
- Indica muros e=0.30m
- Indica muros e=0.35m
- Indica muros e=0.50m
- Indica columnas
- Indica muros de contención
- Indica columnas que mueren
- Indica vigas
- VG-000 Indica N° de viga
- Indica placa NE.+0.30
- Indica muro en mampostería

NOTAS

1. Ver detalles generales en el PL.N° 2002
2. Ver despieces de vigas en los PL.N° 2376 - PL.N° 2382
3. Ver cortes del 1-1 al 7-7 en PL.N° 2383

EST - 2375-PP-P1
VERSIÓN PLANO V-01
OBRA No. 1157

CONSTRUCCIONES PLANIFICADAS
Carrera 13 No. 26A - 47 Piso 2
PBX: 339 41 11 Fax: 287 62 16

Robledales RESERVADO

CONTIENE:

NOMBRE DEL PROYECTO
ROBLEDALES-TORRE PALMERI 1

Dirección AK 7 134 06

PLANTA PISO 1

ESCALA: INDICADA

ARCHIVO:	1157-EST-2375-PP-P1-PLANTA PISO 1.DWG
FECHA: 26/01/2026	DIBUJADO POR: KAREN CASTILLO

DISEÑADOR ESTRUCTURAL
ROBERTO AYCARDI FONSECA
TP: 2520257258 CND

DISEÑADOR DE ELMENTOS NO ESTRUCTURALES
VICTOR H. DÁVILA F.
TP: 2520122782 CND

REVISOR ESTRUCTURAL
NICOLAS PARRA GARCIA
TP: 25202-62063 CND

CONSTRUCTOR RESPONSABLE
ALVARO DÍAZ ULLOA
TP: 2520275046 CND

CONSTRUCCIONES PLANIFICADAS
GERENTE DE DISEÑO
DIRECTOR DE ARQUITECTURA
ANDRÉS VALCARCEL
DIRECTOR DE INGENIERÍA
MARIO FERNANDO RIVERA
DIRECTOR DE PRESUPUESTOS
JAVIER CLAVIJO

EQUIPO DISEÑO CPSA
MP, CO, LL, EC.

MODIFICACIONES

#	Fecha	Emitida por	Modificación

VERSIONES DE PLANOS

Versión	Fecha
V-01	26-01-2026

PROPÓSITO DE LA EMISIÓN

DRAFT	
Coordinación Técnica	
Revisión	
Construcción	✖
Curaduría	
Presupuestos	

MODELO FUENTE: 1157_ROBL-BOG_VIV_ESTR_TP1 17/03/2026	VERSIÓN MODELO: FASE III / V-03

EST - 2375-PP-P1
VERSIÓN PLANO V-01
OBRA No. 1157