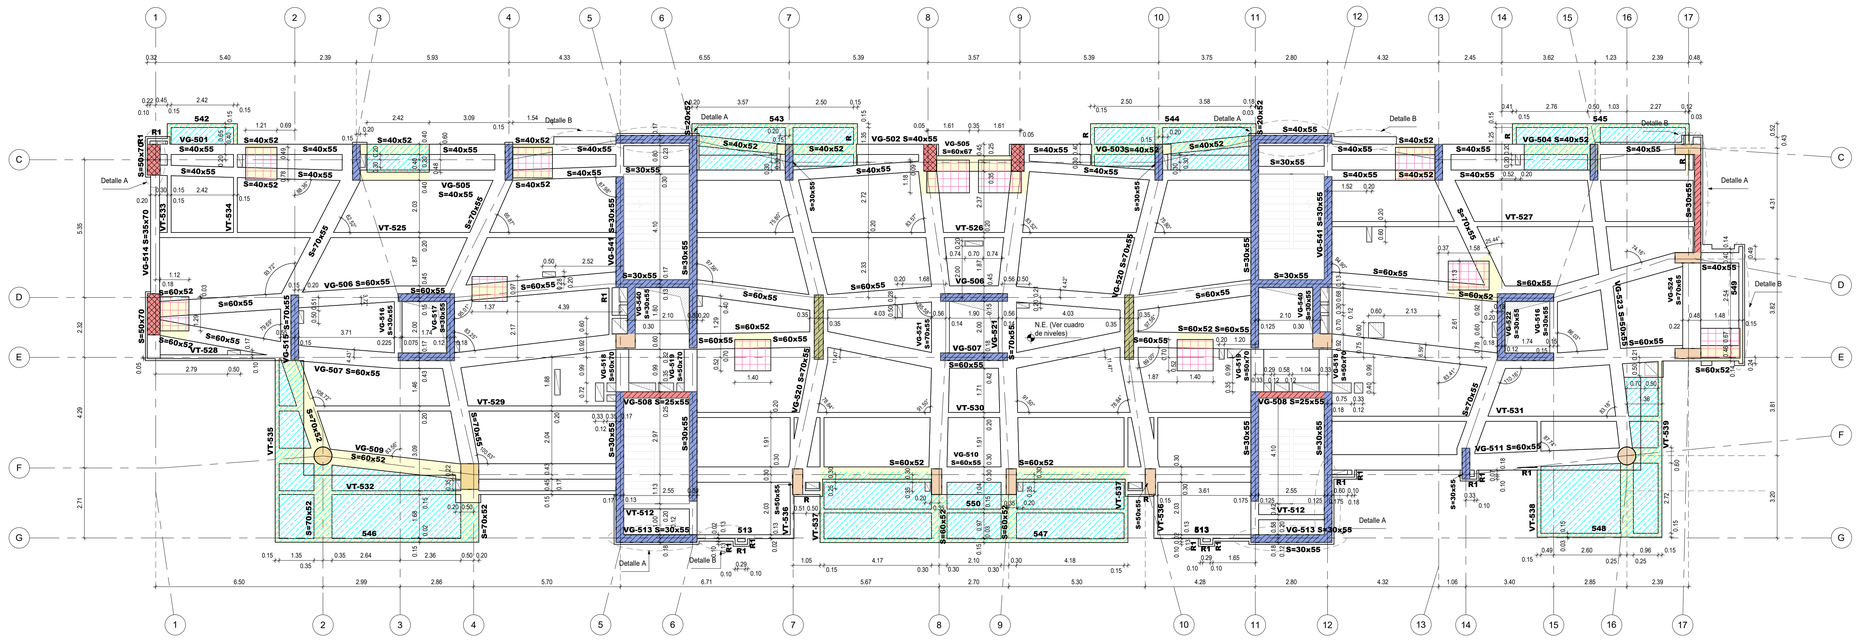

PLANTA DE PISO TIPO 2 (4,6,8 Y 10)
Escala 1 : 100

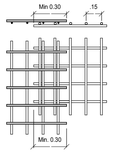

DETALLE TRASLAPO DE MALLAS
Escala 1 : 25

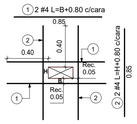

DETALLE DE VACÍOS
Escala 1 : 25

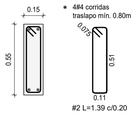

RIOSTRA 15X55 (R)
Escala 1 : 20

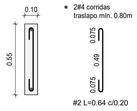

RIOSTRA 10X55 (R1)
Escala 1 : 20

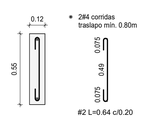

RIOSTRA 12X55 (R2)
Escala 1 : 20

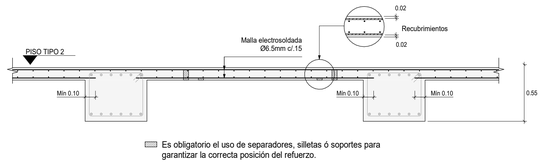

CORTE TÍPICO DE PLACA e=0.12
Escala 1 : 25

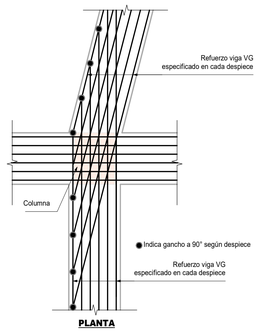

PLANTA

DETALLE DE DOBLEZ EN COLUMNA
Escala 1 : 25

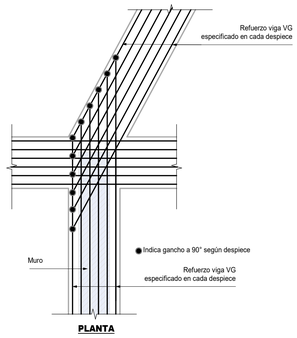

PLANTA

DETALLE DE DOBLEZ EN MURO
Escala 1 : 25

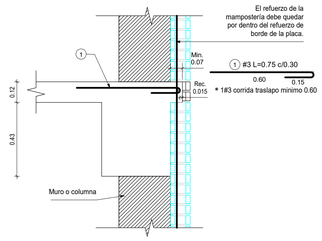

DETALLE A
Escala 1 : 15

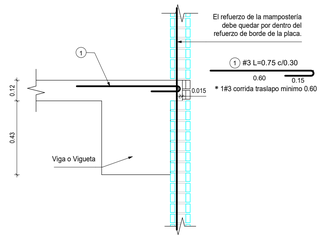

DETALLE B
Escala 1 : 15

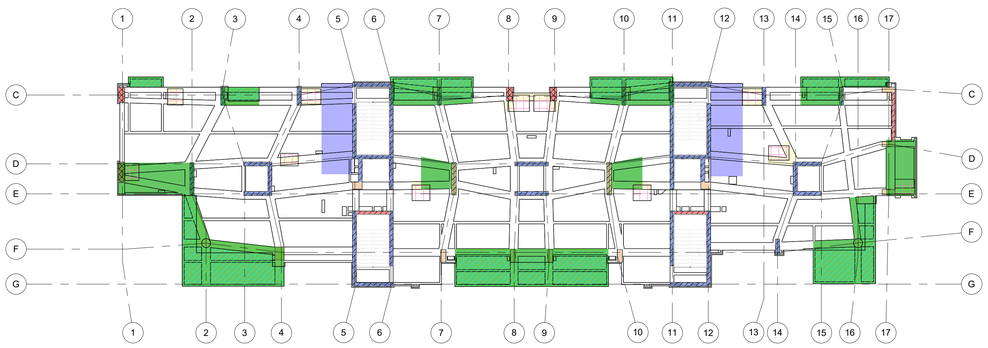

CONVENCIONES CARGA VIVA
- Indica carga viva 500 Kg/m²
- Indica carga viva 600 Kg/m²
- Indica carga viva 180 Kg/m²

PLANTA DE PISO TIPO 2 (4,6,8 Y 10)-CARGAS VIVAS
Escala 1 : 200

CUADRO DE NIVELES PISO TIPO 2

PISO	NIVEL	NIVEL A
PISO 04_NE(+12.60)	12.60	12.57
PISO 06_NE(+19.80)	19.80	19.77
PISO 08_NE(+27.00)	27.00	26.97
PISO 10_NE(+34.20)	34.20	34.17

CONCRETO

PLACAS-VIGAS

• PISO 4	• PISO 6 Y PISO 8	• PISO 10
f'c=42 MPa	**f'c=35 MPa**	**f'c=31.5 MPa**
f'c=420 kg/cm²	**f'c=350 kg/cm²**	**f'c=315 kg/cm²**
f'c=6000 psi	**f'c=5000 psi**	**f'c=4500 psi**

CONVENCIONES
- Indica muros e=0.25m
- Indica muros e=0.30m
- Indica muros e=0.35m
- Indica muros e=0.50m
- Indica columnas S=40x100
- Indica columnas S=70x100
- Indica columnas S=75x55
- Indica columnas S=Ø70
- Indica columnas que mueren
- Indica vigas
- Indica placa e=0.12 N.E. 5.37
- Indica placa e=0.09 N.E. 5.37
- **VG-000** Indica N° de viga

NOTAS
1. Ver detalles generales en el PL.N° 2002
2. Ver despieces de vigas en los PL.N° 2452 - PL.N° 2460
3. Todas las vigas que se encuentren en el desnivel de -0.03m por presencia de duchas o balcones son de h=52
4. Ver plano de localización de Duchas y balcones en PL.N° 2451
5. Prever riostras para apoyo superior de ventanería piso a techo de los balcones, las cuales se fundirán en conjunto con la placa y vigas de cada entrepiso.

EST - 2450-PP-P1
VERSIÓN PLANO V-01
OBRA No. 1157

CONSTRUCCIONES PLANIFICADAS
Carrera 13 No. 26A - 47 Piso 2
PBX: 339 41 11 Fax: 287 62 16

Robledales RESERVADO

CONTIENE:

NOMBRE DEL PROYECTO
ROBLEDALES-TORRE PALMERI 1

Dirección AK 7 134 06

PLANTA PISO TIPO 2 (4,6,8 Y 10)

ESCALA: INDICADA

ARCHIVO: 1157-EST-2450-PP-P1-PLANTA PISO TIPO 2 (4,6,8 Y 10).DWG

FECHA:	DIBUJADO POR:
02/02/2026	KAREN CASTILLO

DISEÑADOR ESTRUCTURAL
ROBERTO AYCARDI FONSECA
TP: 2520257258 CND

DISEÑADOR DE ELMENTOS NO ESTRUCTURALES
VICTOR H. DÁVILA F.
TP: 2520122782 CND

REVISOR ESTRUCTURAL
NICOLAS PARRA GARCIA
TP: 25202-62063 CND

CONSTRUCTOR RESPONSABLE
ALVARO DÍAZ ULLOA
TP: 2520275046 CND

CONSTRUCCIONES PLANIFICADAS
GERENTE DE DISEÑO
DIRECTOR DE ARQUITECTURA
ANDRÉS VALCARCEL
DIRECTOR DE INGENIERÍA
MARIO FERNANDO RIVERA
DIRECTOR DE PRESUPUESTOS
JAVIER CLAVIJO

EQUIPO DISEÑO CPSA
MP, CO, LL, EC.

MODIFICACIONES

#	Fecha	Emitida por	Modificación

VERSIONES DE PLANOS

Versión	Fecha
V-01	02-02-2026

PROPÓSITO DE LA EMISIÓN

DRAFT	
Coordinación Técnica	
Revisión	
Construcción	✖
Curaduría	
Presupuestos	

MODELO FUENTE: 1157_ROBL-BOG_VIV_ESTR_TP1
17/03/2026

VERSIÓN MODELO: FASE III / V-03

EST - 2450-PP-P1
VERSIÓN PLANO V-01
OBRA No. 1157