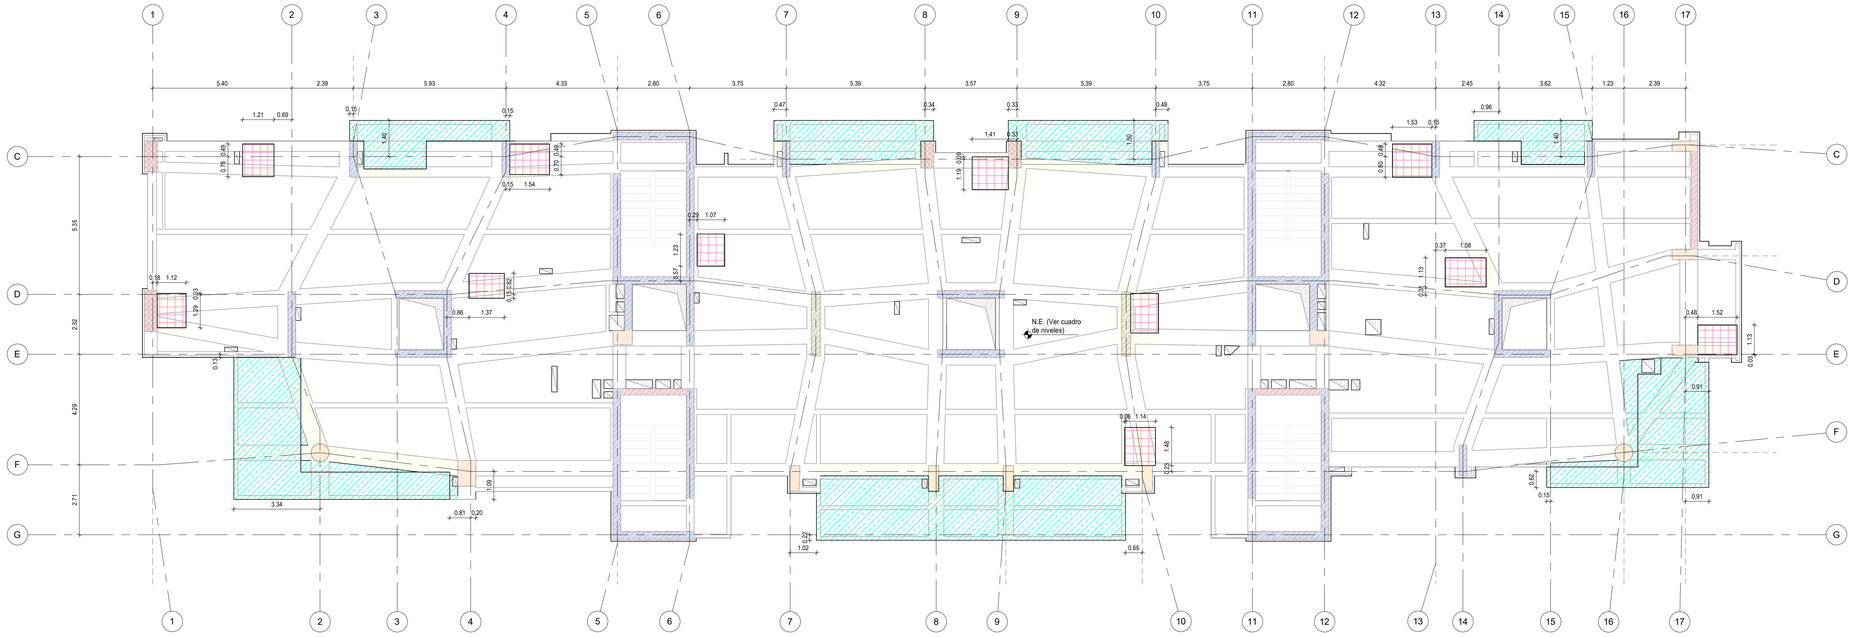


**PLANTA LOCALIZACIÓN DE DUCHAS PISO 13 Y PISO 15**
**Escala 1 : 100**

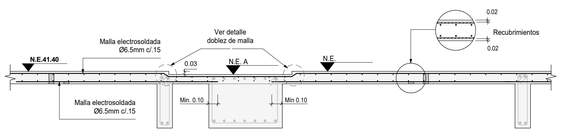


Es obligatorio el uso de separadores, silletas ó soportes para garantizar la correcta posición del refuerzo.

**CORTE TÍPICO DE PLACA ZONA DE DUCHAS**
**Escala 1 : 25**

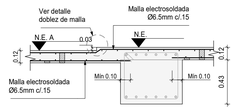


Es obligatorio el uso de separadores, silletas ó soportes para garantizar la correcta posición del refuerzo.

**CORTE TÍPICO DE PLACA e=0.12 con paso a PLACA e=0.12 EN APOYO PLACA**
**Escala 1 : 25**

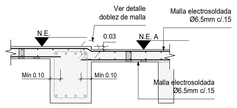


Es obligatorio el uso de separadores, silletas ó soportes para garantizar la correcta posición del refuerzo.

**CORTE TÍPICO DE PLACA e=0.12 con paso a PLACA e=0.12 EN APOYO VIGA**
**Escala 1 : 25**

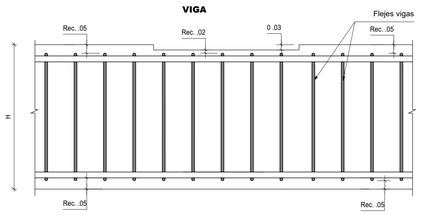


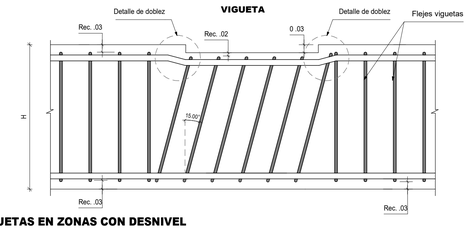


**RECUBRIMIENTOS CAMBIOS DE SECCIÓN VIGAS Y VIGUETAS EN ZONAS CON DESNIVEL**

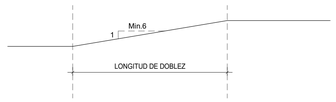


**DETALLE DE DOBLEZ DE MALLA Y VARILLA**
**Escala 1 : 10**

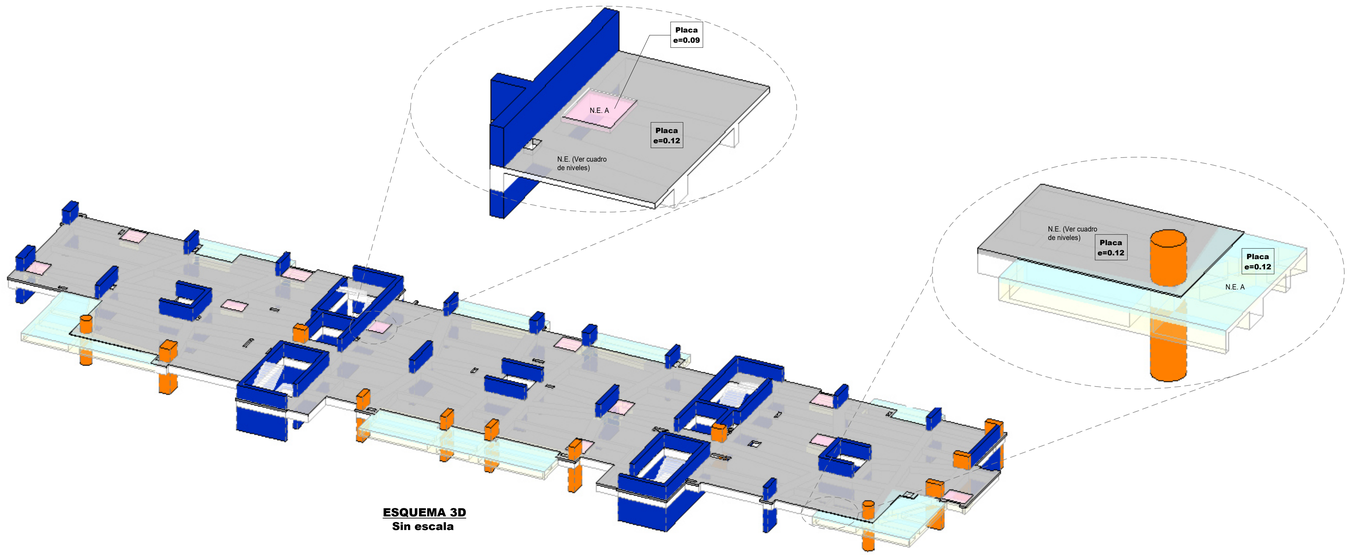


**ESQUEMA 3D**
**Sin escala**

| CUADRO DE NIVELES PISO 13 Y 15 | |
|---|---|
| PISO | NIVEL |
| PISO 13_NE(+45.00) | 45.00 |
| PISO 15_NE(+52.20) | 52.20 |

**CONCRETO**

| • PISO 12 | • PISO 14 |
|---|---|
| **f'c=31.5 MPa** | **f'c=28 MPa** |
| **f'c=315 kg/cm²** | **f'c=280 kg/cm²** |
| **f'c=4500 psi** | **f'c=4000 psi** |

**CONVENCIONES**

- Indica muros e=0.25m
- Indica muros e=0.30m
- Indica muros e=0.35m
- Indica muros e=0.50m
- Indica columnas S=40x100
- Indica columnas S=70x100
- Indica columnas S=75x55
- Indica columnas S=Ø70
- Indica columnas que mueren
- Indica vigas
- 000 Indica N° de viga

**NOTAS**

1. Ver detalles generales en el PL.N° 2002
2. Ver despieces de vigas en los PL.N° 2527 - PL.N° 2528
3. Todas las vigas que se encuentren en el desnivel de -0.03m por presencia de duchas o balcones son de h=52.

EST - 2526-PP-P1
VERSIÓN PLANO V-01
OBRA No. 1157

CONSTRUCCIONES PLANIFICADAS
Carrera 13 No. 26A - 47 Piso 2
PBX: 339 41 11 Fax: 287 62 16

Robledales RESERVADO

CONTIENE:

NOMBRE DEL PROYECTO
ROBLEDALES-TORRE PALMERI 1

Dirección AK 7 134 06

PLANTA DUCHAS PISO 13 Y 15

ESCALA: INDICADA

ARCHIVO: 1157-EST-2526-PP-P1-PLANTA DUCHAS PISO 13 Y 15.DWG

| FECHA: | DIBUJADO POR: |
|---|---|
| 20/02/2026 | ANDRES DUARTE |

DISEÑADOR ESTRUCTURAL
ROBERTO AYCARDI FONSECA
TP: 2520257258 CND

DISEÑADOR DE ELMENTOS NO ESTRUCTURALES
VICTOR H. DÁVILA F.
TP: 2520122782 CND

REVISOR ESTRUCTURAL
NICOLAS PARRA GARCIA
TP: 25202-62063 CND

CONSTRUCTOR RESPONSABLE
ALVARO DÍAZ ULLOA
TP: 2520275046 CND

CONSTRUCCIONES PLANIFICADAS

GERENTE DE DISEÑO

DIRECTOR DE ARQUITECTURA
ANDRÉS VALCARCEL

DIRECTOR DE INGENIERÍA
MARIO FERNANDO RIVERA

DIRECTOR DE PRESUPUESTOS
JAVIER CLAVIJO

EQUIPO DISEÑO CPSA
MP, CO, LL, EC.

MODIFICACIONES

| # | Fecha | Emitida por | Modificación |
|---|---|---|---|

VERSIONES DE PLANOS

| Versión | Fecha |
|---|---|
| V-01 | 20-02-2026 |

PROPÓSITO DE LA EMISIÓN

| | |
|---|---|
| DRAFT | |
| Coordinación Técnica | |
| Revisión | |
| Construcción | X |
| Curaduría | |
| Presupuestos | |

| MODELO FUENTE: | VERSIÓN MODELO: |
|---|---|
| 1157_ROBL-BOG_VIV_ESTR_TP1<br>17/03/2026 | FASE III / V-03 |

EST - 2526-PP-P1
VERSIÓN PLANO V-01
OBRA No. 1157