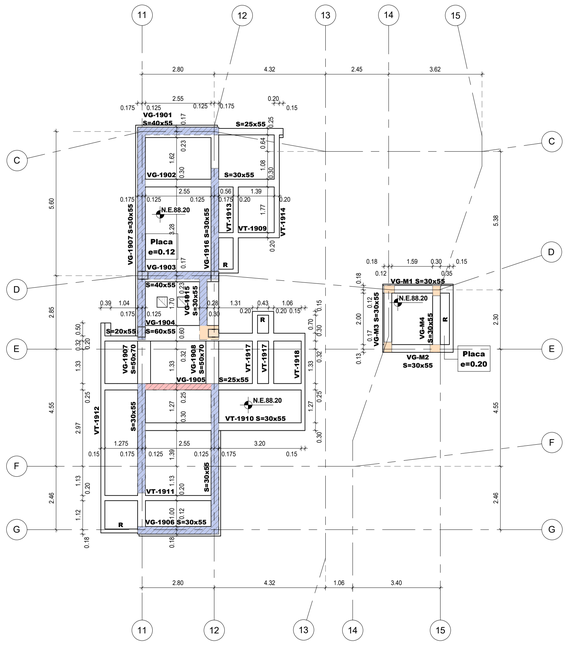

PLANTA DE PISO 25 NE(+88.20)
Escala 1 : 100

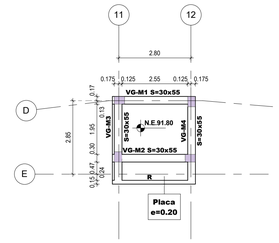

PLANTA DE CUBIERTA NE(+91.80)
Escala 1 : 100

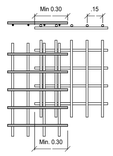

DETALLE TRASLAPO DE MALLAS
Escala 1 : 25

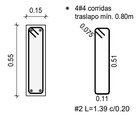

RIOSTRA 15X55 (R)
Escala 1 : 20

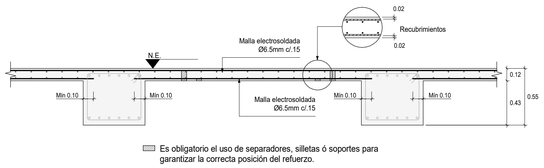

CORTE TÍPICO PLACA e=0.12
Escala 1 : 25

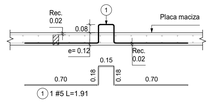

NOTAS:

1. Capacidad de gancho 3 T.
2. La varilla para gancho de línea de vida debe estar posicionada en la malla inferior de la placa
3. Las varillas expuestas para ganchos se deben protegen contra la corrosión con éposxico según proveedores especializados.

DETALLE DE GANCHO PARA LINEA DE VIDA
Escala 1 : 25

CARGA VIVA

Cubierta: 180 Kg/m^2

CONCRETO

f'c=28 MPa
f'c=280 kg/cm²
f'c=4000 psi

CONVENCIONES

- Indica muros e=0.25m
- Indica muros e=0.30m
- Indica columnas S=40x100
- Indica columnas S=70x100
- Indica columnas S=75x55
- Indica columnas que mueren
- Indica vigas
- 000 Indica N° de viga

NOTAS

1. Ver detalles generales en el PL.N° 2002
2. Ver despieces de vigas en el PL.N° 2776
3. Carga viva de 180 Kg/m^2
4. Prever riostras para apoyo superior de ventanería piso a techo de los balcones, las cuales se fundirán en conjunto con la placa y vigas de cada entrepiso.

EST - 2775-PP-P1
VERSIÓN PLANO V-01
OBRA No. 1157

CONSTRUCCIONES PLANIFICADAS
Carrera 13 No. 26A - 47 Piso 2
PBX: 339 41 11 Fax: 287 02 16

Robledales RESERVADO

CONTIENE:

NOMBRE DEL PROYECTO
ROBLEDALES-TORRE PALMERI 1

Dirección AK 7 134 06

PLANTA PISO 25 Y CUBIERTA

ESCALA: INDICADA

ARCHIVO: 1157-EST-2775-PP-P1-PLANTA PISO 25 Y CUBIERTA.DWG

FECHA:	DIBUJADO POR:
05/03/2026	KAREN CASTILLO

DISEÑADOR ESTRUCTURAL
ROBERTO AYCARDI FONSECA
TP: 2520257258 CND

DISEÑADOR DE ELMENTOS NO ESTRUCTURALES
VICTOR H. DÁVILA F.
TP: 2520122782 CND

REVISOR ESTRUCTURAL
NICOLAS PARRA GARCIA
TP: 25202-62063 CND

CONSTRUCTOR RESPONSABLE
ALVARO DÍAZ ULLOA
TP: 2520275046 CND

CONSTRUCCIONES PLANIFICADAS

GERENTE DE DISEÑO

DIRECTOR DE ARQUITECTURA
ANDRÉS VALCARCEL

DIRECTOR DE INGENIERÍA
MARIO FERNANDO RIVERA

DIRECTOR DE PRESUPUESTOS
JAVIER CLAVIJO

EQUIPO DISEÑO CPSA
MP, CO, LL, EC.

MODIFICACIONES

#	Fecha	Emitida por	Modificación

VERSIONES DE PLANOS

Versión	Fecha
V-01	05-03-2026

PROPÓSITO DE LA EMISIÓN

DRAFT	
Coordinación Técnica	
Revisión	
Construcción	X
Curaduría	
Presupuestos	

MODELO FUENTE:	VERSIÓN MODELO:
1157_ROBL-BOG_VIV_ESTR_TP1 17/03/2026	FASE III / V-03

EST - 2775-PP-P1
VERSIÓN PLANO V-01
OBRA No. 1157