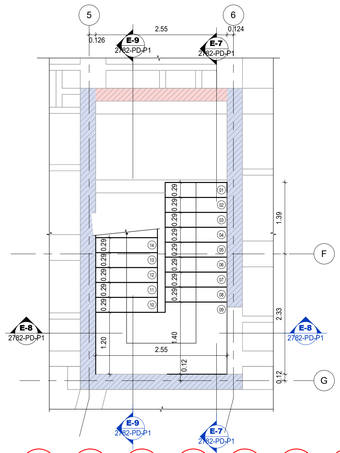

PLANTA ARRANQUE ESCALERA TIPO 1 DE LOBBY A PISO 1
Escala 1 : 50

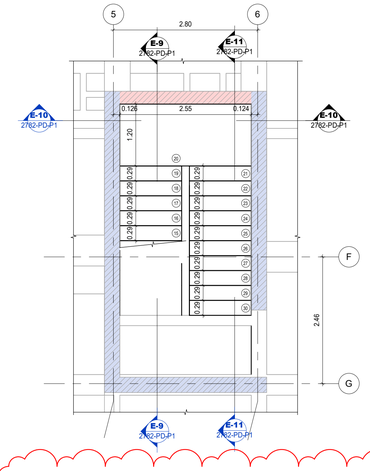

PLANTA LLEGADA ESCALERA TIPO 1 DE LOBBY A PISO 2
Escala 1 : 50

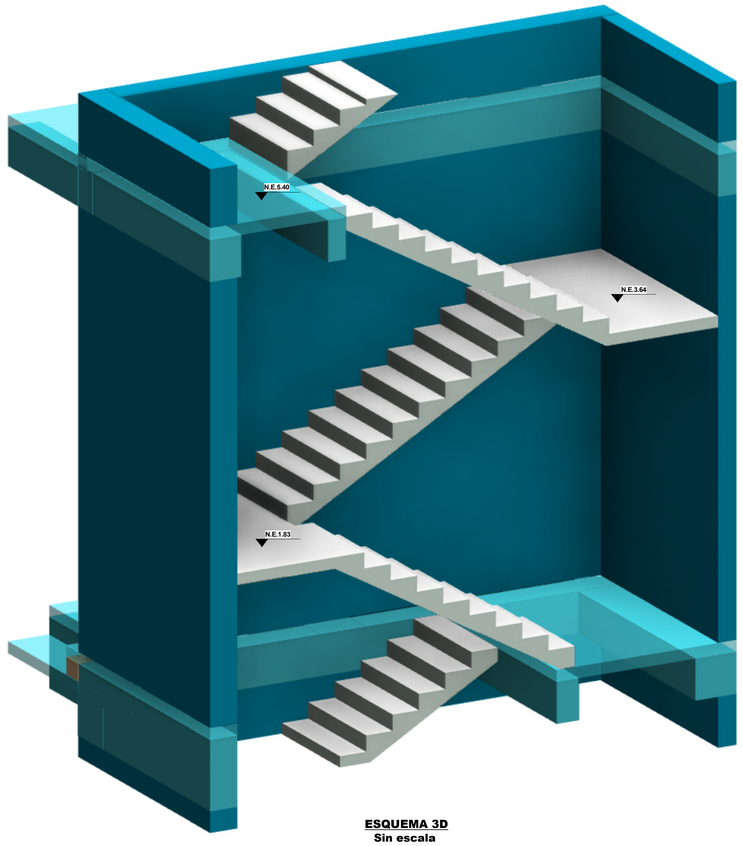

ESQUEMA 3D
Sin escala

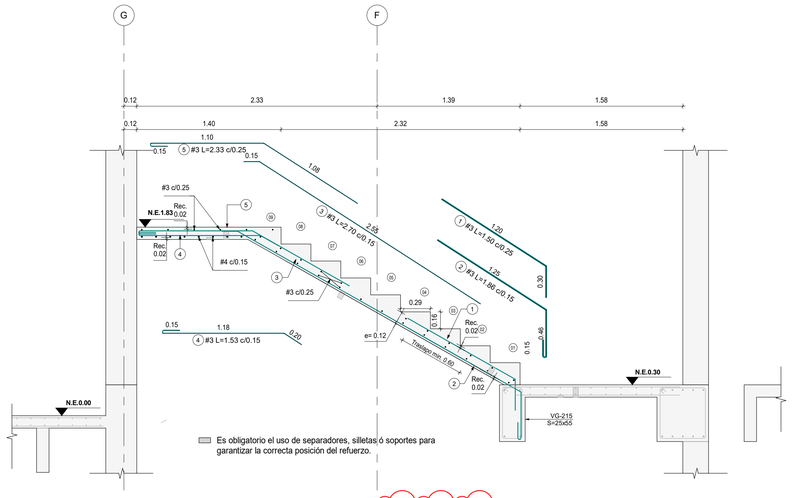

CORTE E-7
Escala 1 : 25

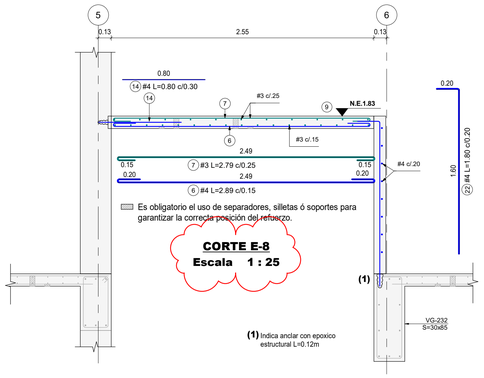

CORTE E-8
Escala 1 : 25

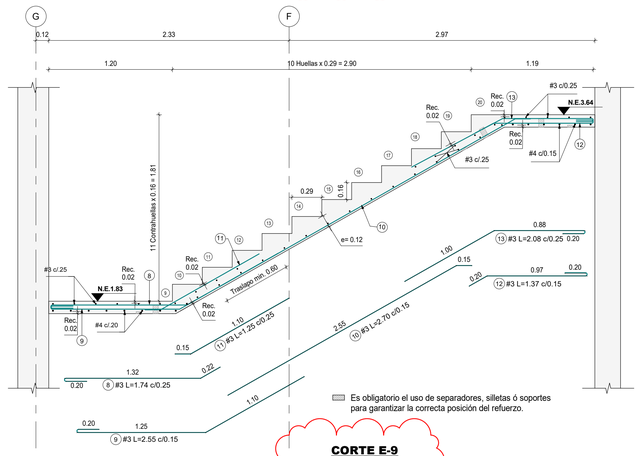

CORTE E-9
Escala 1 : 25

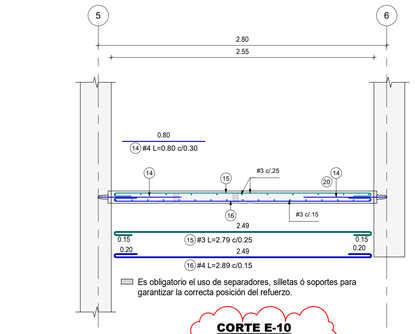

CORTE E-10
Escala 1 : 25

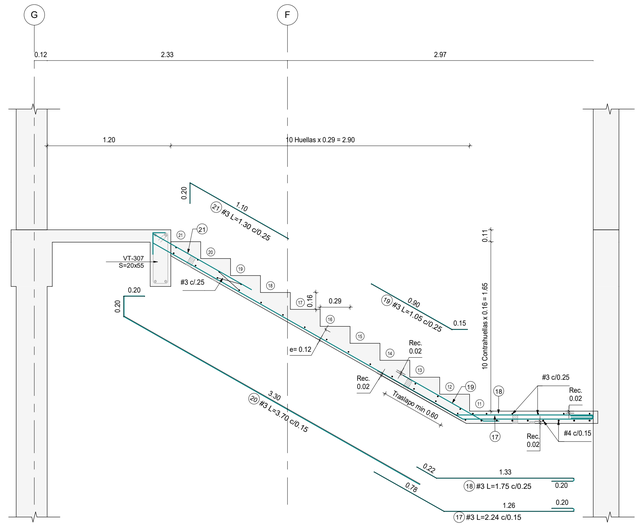

CORTE E-11
Escala 1 : 25

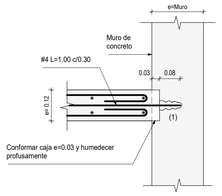

(1) Indica anclar con epóxico estructural
Indica caja de 3cm de profundidad

DETALLE ANCLAJE EPOXICO
Escala 1 : 10

CONCRETO
f'c=21 MPa
f'c=210 kg/cm²
f'c=3000 psi
CONVENCIONES
Indica muros e=0.25m
Indica muros e=0.30m
NOTAS
1. Ver detalles generales en el PL.N° 2002

EST - 2782-PD-P1
VERSIÓN PLANO V-02
OBRA No. 1157

CONSTRUCCIONES PLANIFICADAS
Carrera 13 No. 26A - 47 Piso 2
PBX: 339 41 11 Fax: 287 62 16

Robledales RESERVADO

CONTIENE:

NOMBRE DEL PROYECTO
ROBLEDALES-TORRE PALMERI 1

Dirección AK 7 134 06

DESPIECE ESCALERA TIPO 1 LOBBY A PISO 1

ESCALA: INDICADA

ARCHIVO: 2782-PD-P1-DESPIECE ESCALERA TIPO 1 LOBBY A PISO 1.DWG

FECHA:	DIBUJADO POR:
17/03/2026	KAREN CASTILLO

DISEÑADOR ESTRUCTURAL
ROBERTO AYCARDI FONSECA
TP: 2520257258 CND

DISEÑADOR DE ELMENTOS NO ESTRUCTURALES
VICTOR H. DÁVILA F.
TP: 2520122782 CND

REVISOR ESTRUCTURAL
NICOLAS PARRA GARCIA
TP: 25202-62063 CND

CONSTRUCTOR RESPONSABLE
ALVARO DÍAZ ULLOA
TP: 2520275046 CND

CONSTRUCCIONES PLANIFICADAS

GERENTE DE DISEÑO

DIRECTOR DE ARQUITECTURA
ANDRÉS VALCARCEL

DIRECTOR DE INGENIERÍA
MARIO FERNANDO RIVERA

DIRECTOR DE PRESUPUESTOS
JAVIER CLAVIJO

EQUIPO DISEÑO CPSA
MP, CO, LL, EC.

MODIFICACIONES

#	Fecha	Emitida por	Modificación
1	17/03/2026	B	Actualización General de refuerzo escalera

VERSIONES DE PLANOS

Versión	Fecha
V-01	13-03-2026
V-02	17-03-2026

PROPÓSITO DE LA EMISIÓN

DRAFT	
Coordinación Técnica	
Revisión	
Construcción	✖
Curaduría	
Presupuestos	

MODELO FUENTE: 1157_ROBL-BOG_VIV_ESTR_TP1
17/03/2026

VERSIÓN MODELO: FASE III / V-03

EST - 2782-PD-P1
VERSIÓN PLANO V-02
OBRA No. 1157