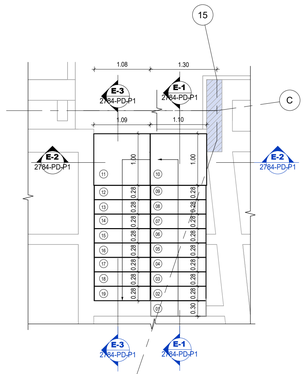


**PLANTA ESCALERA PISO 22 A PISO 23**
**Escala 1 : 50**

V-02
B | 1

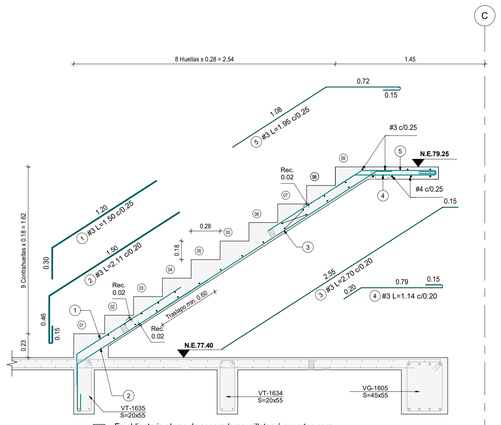


Es obligatorio el uso de separadores, silletas ó soportes para garantizar la correcta posición del refuerzo.

**CORTE E-1**
**Escala 1 : 25**

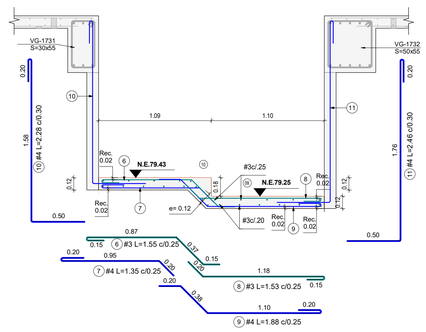


Es obligatorio el uso de separadores, silletas ó soportes para garantizar la correcta posición del refuerzo.

**CORTE E-2**
**Escala 1 : 25**

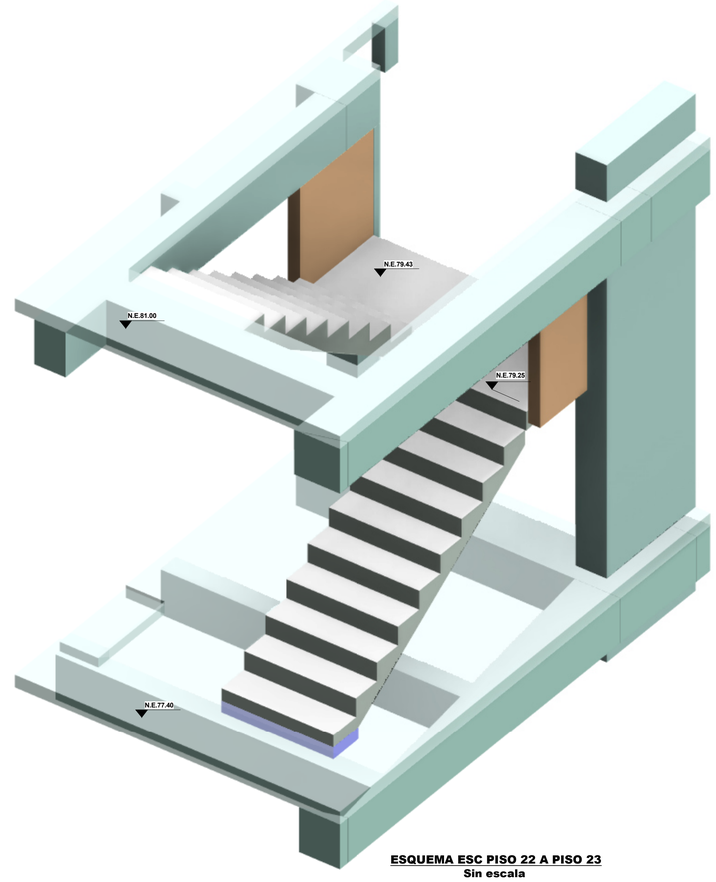


**ESQUEMA ESC PISO 22 A PISO 23**
**Sin escala**

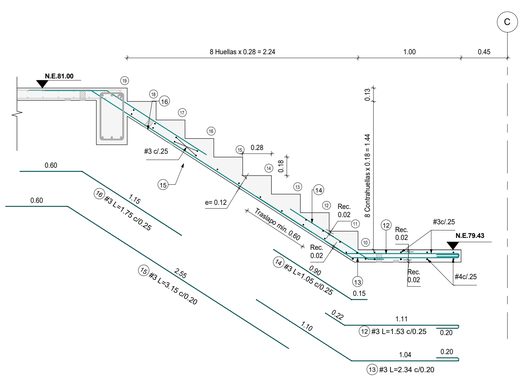


Es obligatorio el uso de separadores, silletas ó soportes para garantizar la correcta posición del refuerzo.

**CORTE E2-3**
**Escala 1 : 25**

| CONCRETO |
|---|
| **f'c=21 MPa** |
| **f'c=210 kg/cm²** |
| **f'c=3000 psi** |
| **CONVENCIONES** |
| Indica muros e=0.25m |
| Indica muros e=0.30m |
| **NOTAS** |
| 1. Ver detalles generales en el PL.N° 2002 |

EST - 2784-PD-P1
VERSIÓN PLANO V-02
OBRA No. 1157

CONSTRUCCIONES PLANIFICADAS
Carrera 13 No. 26A - 47 Piso 2
PBX: 339 41 11 Fax: 287 02 16

Robledales RESERVADO

CONTIENE:

NOMBRE DEL PROYECTO
ROBLEDALES-TORRE PALMERI 1

Dirección AK 7 134 06

DESPIECE ESCALERA TIPO 2
PISO 22

ESCALA: INDICADA

ARCHIVO: EST-2784-PD-P1-DESPIECE ESCALERA TIPO 2 PISO 22.DWG

| FECHA: | DIBUJADO POR: |
|---|---|
| 17/03/2026 | KAREN CASTILLO |

DISEÑADOR ESTRUCTURAL
ROBERTO AYCARDI FONSECA
TP: 2520257258 CND

DISEÑADOR DE ELMENTOS NO ESTRUCTURALES
VICTOR H. DÁVILA F.
TP: 2520122782 CND

REVISOR ESTRUCTURAL
NICOLAS PARRA GARCIA
TP: 25202-62063 CND

CONSTRUCTOR RESPONSABLE
ALVARO DÍAZ ULLOA
TP: 2520275046 CND

CONSTRUCCIONES PLANIFICADAS

GERENTE DE DISEÑO

DIRECTOR DE ARQUITECTURA
ANDRÉS VALCARCEL

DIRECTOR DE INGENIERÍA
MARIO FERNANDO RIVERA

DIRECTOR DE PRESUPUESTOS
JAVIER CLAVIJO

EQUIPO DISEÑO CPSA
MP, CO, LL, EC.

MODIFICACIONES

| # | Fecha | Emitida por | Modificación |
|---|---|---|---|
| 1 | 17/03/2026 | B | Actualización General de refuerzo escalera |

VERSIONES DE PLANOS

| Versión | Fecha |
|---|---|
| V-01 | 11-03-2026 |
| V-02 | 17-03-2026 |

PROPÓSITO DE LA EMISIÓN

| | |
|---|---|
| DRAFT | |
| Coordinación Técnica | |
| Revisión | |
| Construcción | ✖ |
| Curaduría | |
| Presupuestos | |

MODELO FUENTE: 1157_ROBL-BOG_VIV_ESTR_TP1
17/03/2026

VERSIÓN MODELO: FASE III / V-03

EST - 2784-PD-P1
VERSIÓN PLANO V-02
OBRA No. 1157