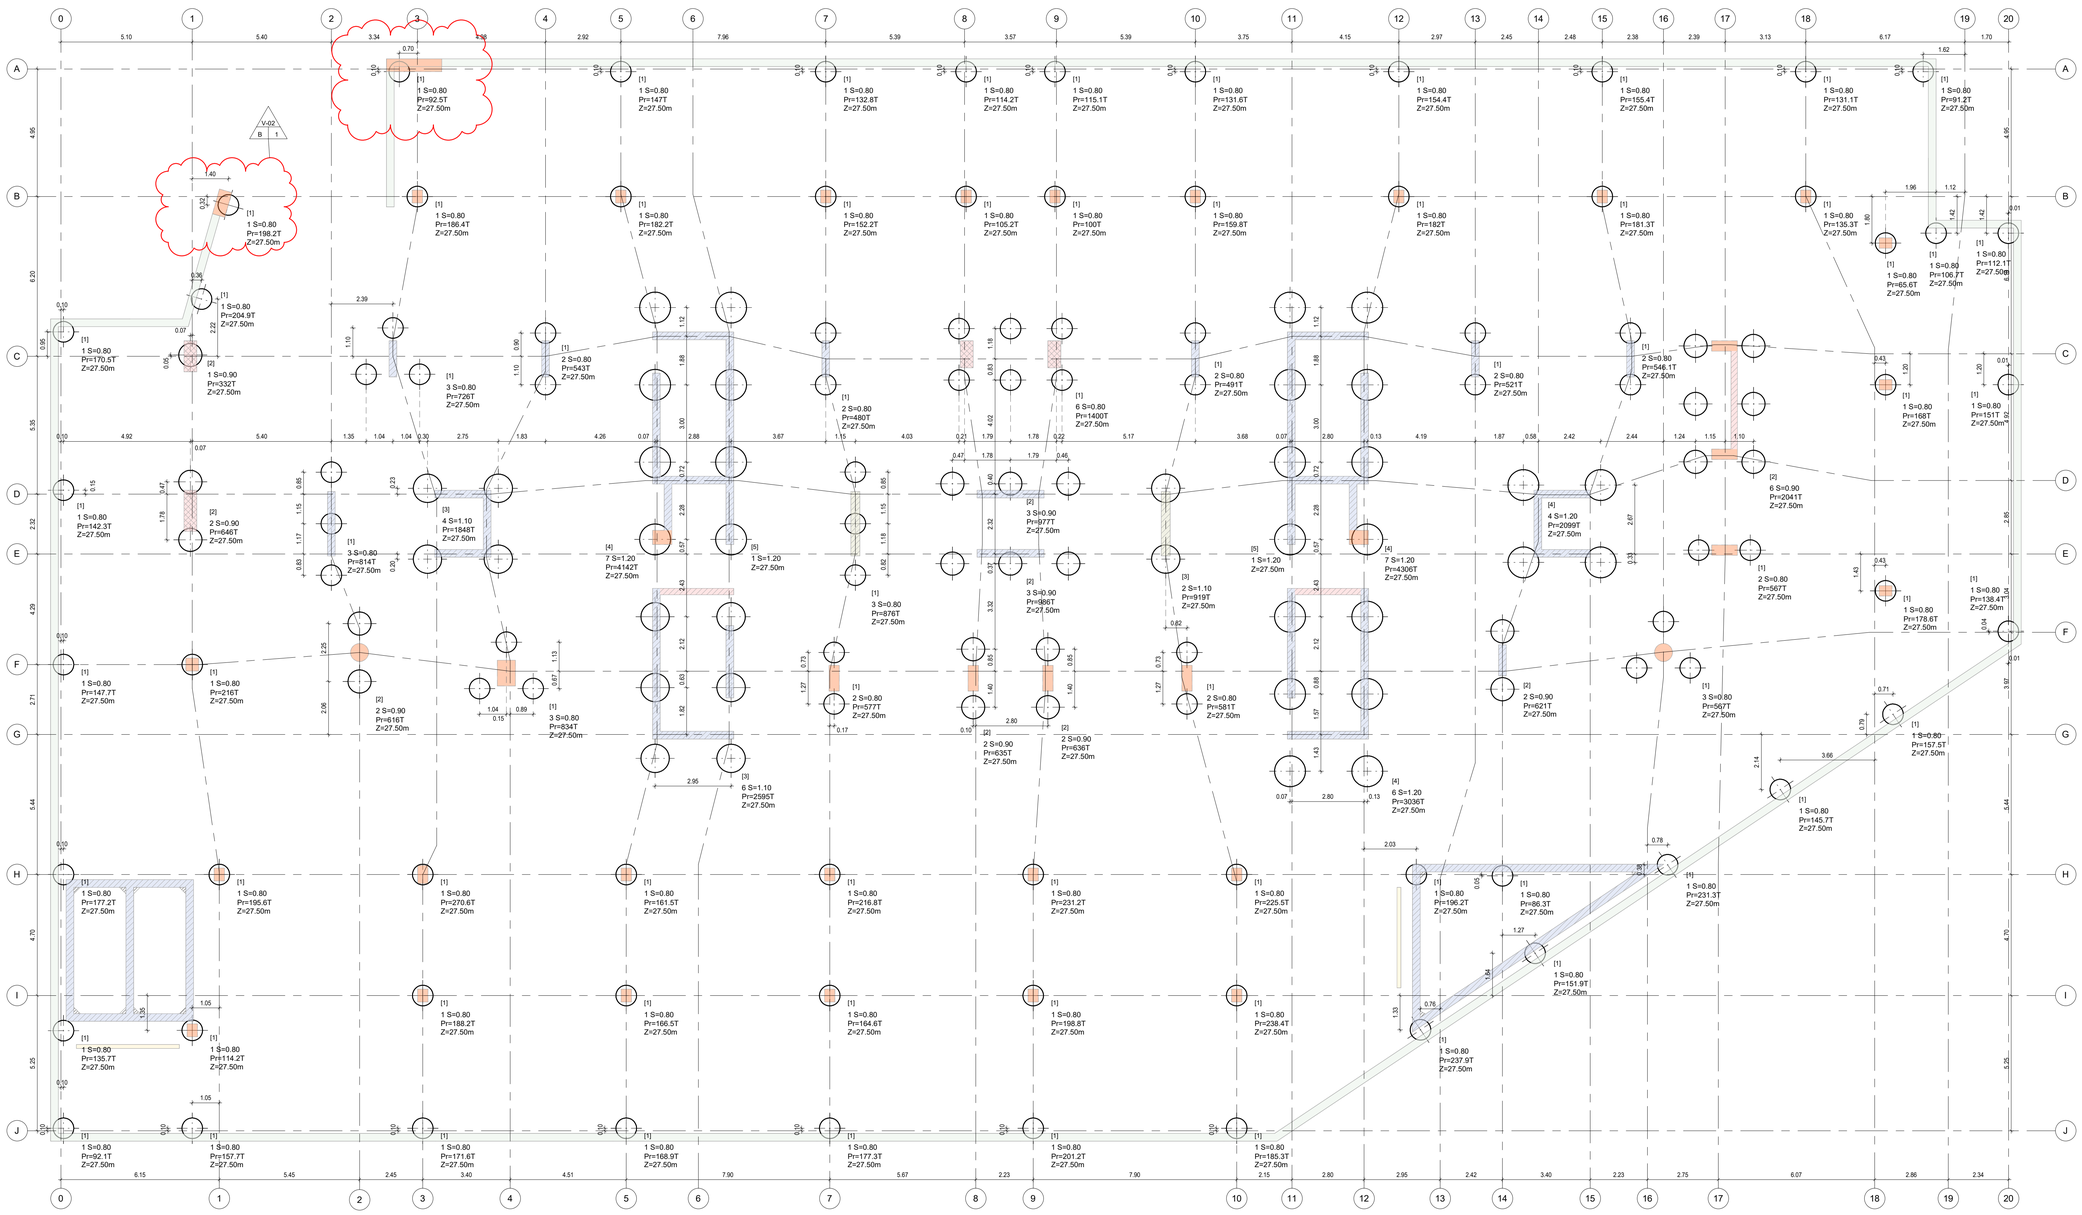

PLANTA LOCALIZACIÓN DE PILOTES
Escala 1 : 100

NOTA:

La longitud ó profundidad del pilote deberá ser revisada y aprobada en obra por el Ingeniero de Suelos para garantizar que la capacidad del elemento sea la establecida en el estudio de suelos.

V°B° INGENIERO DE SUELOS

CONCRETO
f'c=28 MPa
f'c=280 kg/cm²
f'c=4000 psi
CONVENCIONES
Indica muros e=0.25m
Indica muros e=0.30m
Indica muros e=0.35m
Indica muros e=0.50m
Indica columnas
Indica muros de contención
(#) Indica Tipo de Pilote
Pr = Indica carga real en toneladas
Z = Indica profundidad de la punta del pilote medida desde el nivel 0.00-cota 2613.70 M.S.N.M
NOTAS
1. Ver detalles generales en el PL.N° 2002
2. Ver detalles y cuadro de pilotes en el PL. N° 2101

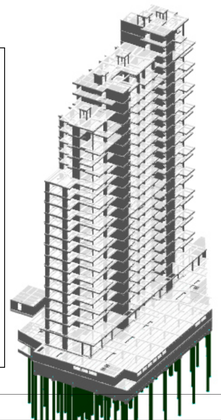

EST - 2100-PP-P1
VERSIÓN PLANO V-02
OBRA No. 1157

CONSTRUCCIONES PLANIFICADAS
Carrera 13 No. 26A - 47 Piso 2
PBX: 339 41 11 Fax: 287 62 16

Robledales RESERVADO

CONTIENE:

NOMBRE DEL PROYECTO
ROBLEDALES-TORRE PALMERI 1

Dirección AK 7 134 06

PLANTA LOCALIZACIÓN DE PILOTES

ESCALA: INDICADA

ARCHIVO: 17-EST-2100-PP-P1-PLANTA LOCALIZACIÓN DE PILOTES.DWG

FECHA:	DIBUJADO POR:
11/03/2026	ANDRES DUARTE

DISEÑADOR ESTRUCTURAL
ROBERTO AYCARDI FONSECA
TP: 2520257258 CND

DISEÑADOR DE ELMENTOS NO ESTRUCTURALES
VICTOR H. DÁVILA F.
TP: 2520212282 CND

REVISOR ESTRUCTURAL
NICOLAS PARRA GARCIA
TP: 25202-62063 CND

CONSTRUCTOR RESPONSABLE
ALVARO DÍAZ ULLOA
TP: 2520275046 CND

CONSTRUCCIONES PLANIFICADAS
GERENTE DE DISEÑO

DIRECTOR DE ARQUITECTURA
ANDRÉS VALCARCEL

DIRECTOR DE INGENIERÍA
MARIO FERNANDO RIVERA

DIRECTOR DE PRESUPUESTOS
JAVIER CLAVIJO

EQUIPO DISEÑO CPSA
MP, CO, LL, EC.

MODIFICACIONES

#	Fecha	Emitida por	Modificación
1	11/03/2026	B	se incluyen columnas para manejo de voladizo y se ajustan secciones de vigas.

VERSIONES DE PLANOS

Versión	Fecha
V-01	12/02/2026
V-02	11/03/2026

PROPÓSITO DE LA EMISIÓN

DRAFT	
Coordinación Técnica	
Revisión	
Construcción	✖
Curaduría	
Presupuestos	

MODELO FUENTE:	VERSIÓN MODELO:
1157_ROBL-BOG_VIV_ESTR_TP1 17/03/2026	FASE III / V-03

EST - 2100-PP-P1
VERSIÓN PLANO V-02
OBRA No. 1157