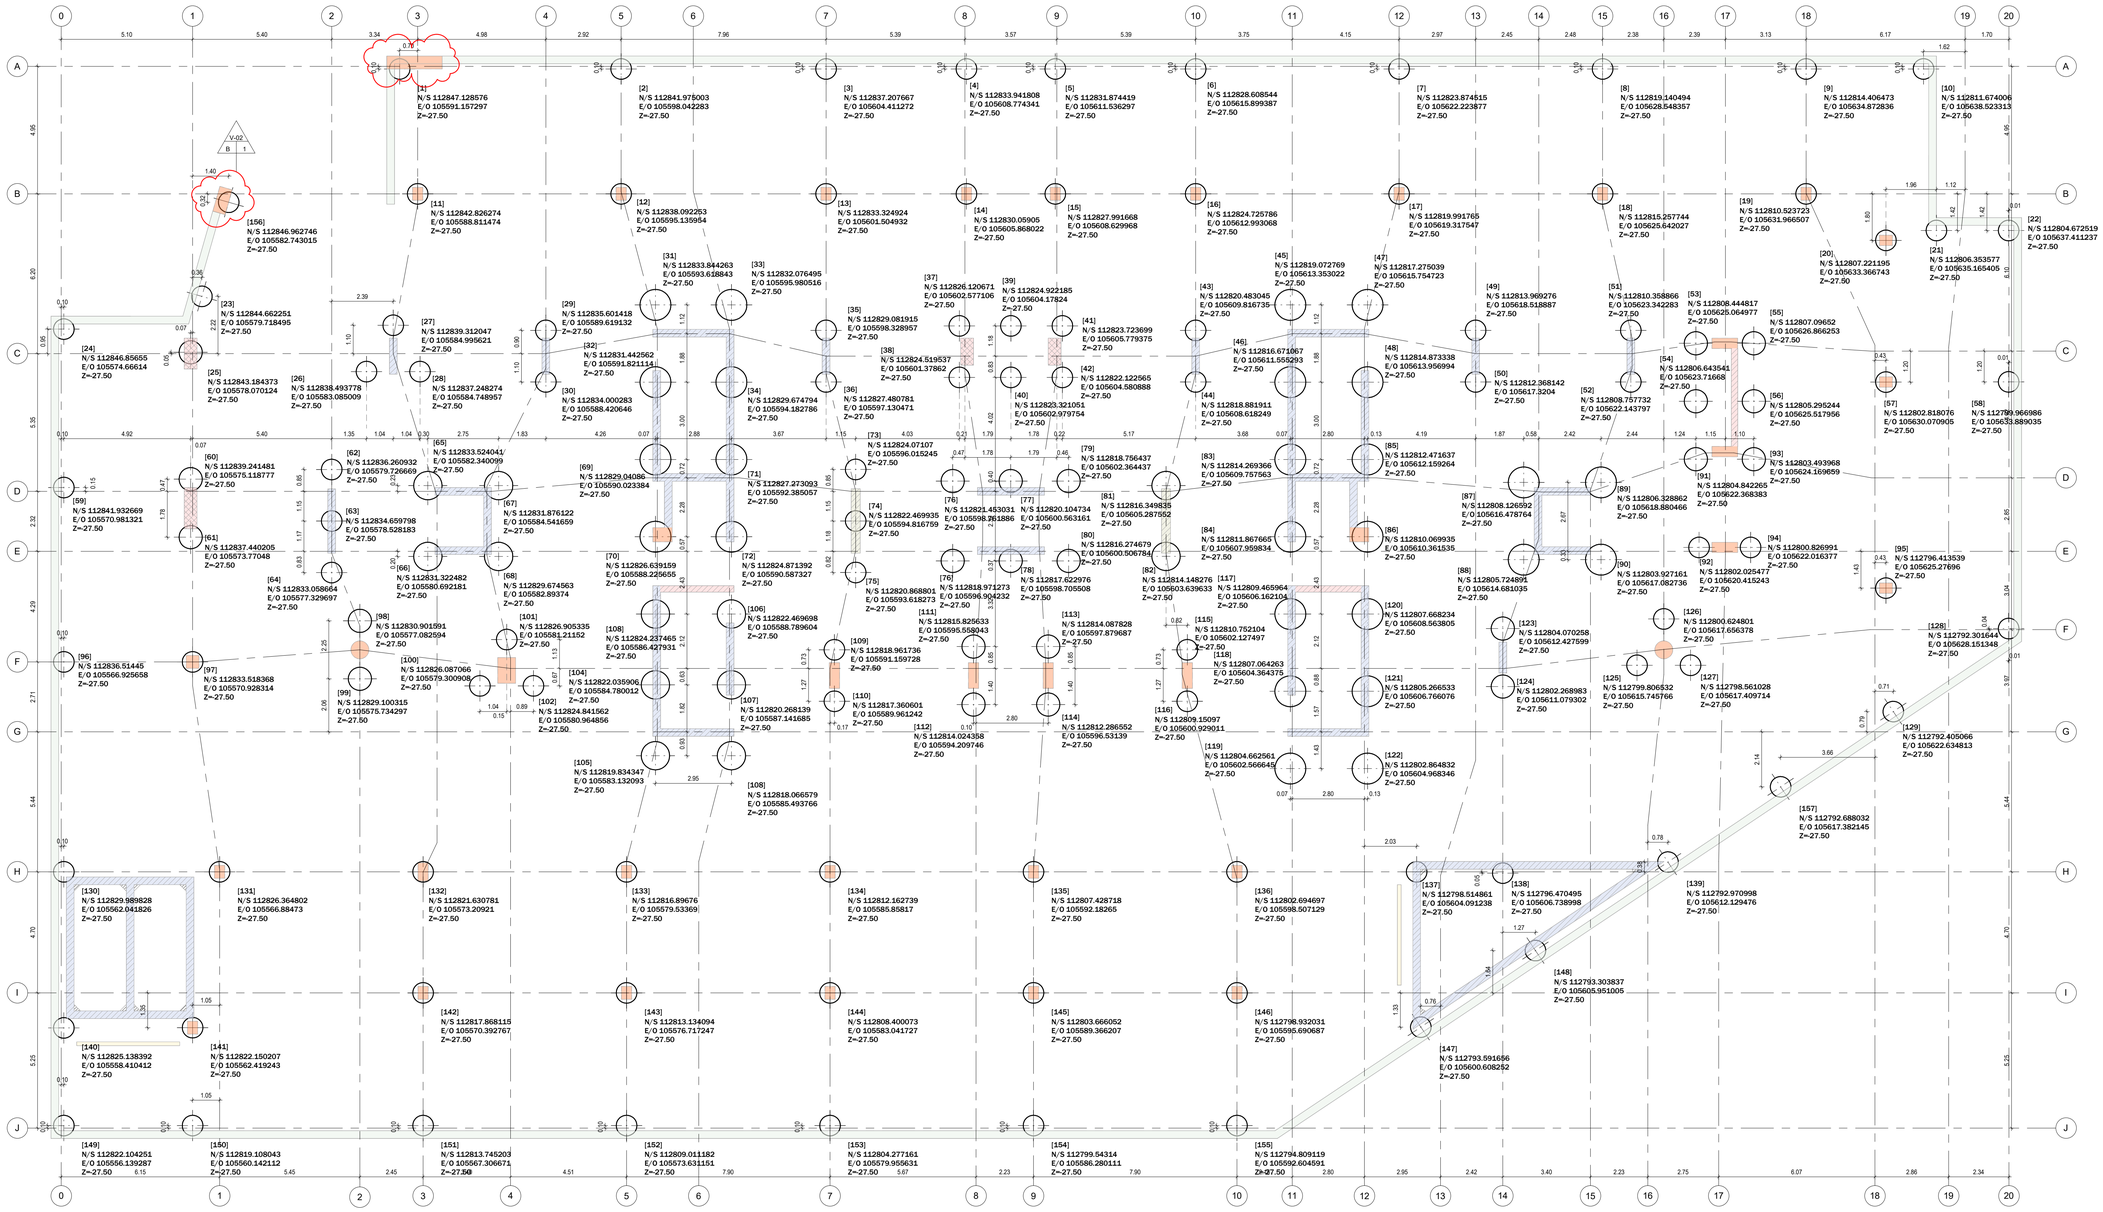

CUADRO DE LOCALIZACIÓN DE PILOTES

Consecutivo Pilote	CoordenadaX	CoordenadaY	Profundidad
1	105591.157297	112847.128576	-27.50
2	105598.042283	112841.975003	-27.50
3	105604.411272	112837.207667	-27.50
4	105608.774341	112833.941808	-27.50
5	105611.536297	112831.874419	-27.50
6	105615.899387	112828.608544	-27.50
7	105622.223877	112823.874515	-27.50
8	105628.548357	112819.140494	-27.50
9	105634.872836	112814.406473	-27.50
10	105638.523313	112811.674006	-27.50
11	105588.811474	112842.826274	-27.50
12	105595.135954	112838.092253	-27.50
13	105601.504932	112833.324924	-27.50
14	105605.868022	112830.05905	-27.50
15	105608.629968	112827.991668	-27.50
16	105612.993068	112824.725786	-27.50
17	105619.317547	112819.991765	-27.50
18	105625.642027	112815.257744	-27.50
19	105631.966507	112810.523723	-27.50
20	105633.366743	112807.221195	-27.50
21	105635.165405	112806.353577	-27.50
22	105637.411237	112804.672519	-27.50
23	105579.718495	112844.662251	-27.50
24	105574.66614	112846.85655	-27.50
25	105578.070124	112843.184373	-27.50
26	105583.085009	112838.493778	-27.50
27	105584.995621	112839.312047	-27.50
28	105584.748957	112837.248274	-27.50
29	105589.619132	112835.601418	-27.50
30	105588.420646	112834.000283	-27.50
31	105593.618843	112833.844263	-27.50
32	105591.821114	112831.442562	-27.50
33	105595.980516	112832.076495	-27.50
34	105594.182786	112829.674794	-27.50
35	105598.328957	112829.081915	-27.50

CUADRO DE LOCALIZACIÓN DE PILOTES

Consecutivo Pilote	CoordenadaX	CoordenadaY	Profundidad
36	105597.130471	112827.480781	-27.50
37	105602.577106	112826.120671	-27.50
38	105601.37862	112824.519537	-27.50
39	105604.17824	112824.922185	-27.50
40	105602.979754	112823.321051	-27.50
41	105605.779375	112823.723699	-27.50
42	105604.580888	112822.122565	-27.50
43	105609.816735	112820.483045	-27.50
44	105608.618249	112818.881911	-27.50
45	105613.353022	112819.072769	-27.50
46	105611.555293	112816.671067	-27.50
47	105615.754723	112817.275039	-27.50
48	105613.956994	112814.873338	-27.50
49	105618.518887	112813.969276	-27.50
50	105617.3204	112812.368142	-27.50
51	105623.342283	112810.358866	-27.50
52	105622.143797	112808.757732	-27.50
53	105625.064977	112808.444817	-27.50
54	105623.71668	112806.643541	-27.50
55	105626.866253	112807.09652	-27.50
56	105625.517956	112805.295244	-27.50
57	105630.070905	112802.818076	-27.50
58	105633.889035	112799.966986	-27.50
59	105570.981321	112841.932669	-27.50
60	105575.118777	112839.241481	-27.50
61	105573.77048	112837.440205	-27.50
62	105579.726669	112836.260932	-27.50
63	105578.528183	112834.659798	-27.50
64	105577.329697	112833.058664	-27.50
65	105582.340099	112833.524041	-27.50
66	105580.692181	112831.322482	-27.50
67	105584.541659	112831.876122	-27.50
68	105582.89374	112829.674563	-27.50
69	105590.023384	112829.04086	-27.50
70	105588.225655	112826.639159	-27.50

CUADRO DE LOCALIZACIÓN DE PILOTES

Consecutivo Pilote	CoordenadaX	CoordenadaY	Profundidad
71	105592.385057	112827.273093	-27.50
72	105590.587327	112824.871392	-27.50
73	105596.015245	112824.07107	-27.50
74	105594.816759	112822.469935	-27.50
75	105593.618273	112820.868801	-27.50
76	105596.904232	112818.971273	-27.50
76	105598.761886	112821.453031	-27.50
77	105600.563161	112820.104734	-27.50
78	105598.705508	112817.622976	-27.50
79	105602.364437	112818.756437	-27.50
80	105600.506784	112816.274679	-27.50
81	105605.287552	112816.349835	-27.50
82	105603.639633	112814.148276	-27.50
83	105609.757563	112814.269366	-27.50
84	105607.959834	112811.867665	-27.50
85	105612.159264	112812.471637	-27.50
86	105610.361535	112810.069935	-27.50
87	105616.478764	112808.126592	-27.50
88	105614.681035	112805.724895	-27.50
89	105618.880466	112806.328862	-27.50
90	105617.082736	112803.927161	-27.50
91	105622.368383	112804.842265	-27.50
92	105620.415243	112802.025477	-27.50
93	105624.169659	112803.493968	-27.50
94	105622.016377	112800.826991	-27.50
95	105625.27696	112796.413539	-27.50
96	105566.925658	112836.51445	-27.50
97	105570.928314	112833.518368	-27.50
98	105577.082594	112830.901591	-27.50
99	105575.734297	112829.100315	-27.50
100	105579.300906	112826.087066	-27.50
101	105581.21152	112826.905335	-27.50
102	105580.964856	112824.841562	-27.50
104	105584.780012	112822.035906	-27.50

PLANTA LOCALIZACIÓN DE PILOTES CON COORDENADAS

Escala 1 : 100

CUADRO DE LOCALIZACIÓN DE PILOTES

Consecutivo Pilote	CoordenadaX	CoordenadaY	Profundidad
105	105583.132093	112819.834347	-27.50
106	105588.789604	112822.469698	-27.50
107	105587.141685	112820.268139	-27.50
108	105586.427931	112824.237465	-27.50
108	105585.493766	112818.066579	-27.50
109	105591.159728	112818.961736	-27.50
110	105589.961242	112817.360601	-27.50
111	105595.558043	112815.825633	-27.50
112	105594.209746	112814.024338	-27.50
113	105597.879687	112814.087828	-27.50
114	105596.53139	112812.286552	-27.50
116	105600.929011	112809.15097	-27.50
117	105606.162104	112809.465964	-27.50
118	105604.364376	112807.064263	-27.50
119	105602.566645	112804.662561	-27.50
120	105608.563805	112807.668234	-27.50
121	105606.766076	112805.266533	-27.50
122	105604.968346	112802.864832	-27.50
123	105612.427599	112804.070258	-27.50
124	105611.079302	112802.268983	-27.50
125	105615.745766	112799.806532	-27.50
126	105617.656378	112800.624801	-27.50
127	105617.409714	112798.561028	-27.50
128	105628.151348	112792.301644	-27.50
129	105622.634813	112792.405066	-27.50
130	105562.041826	112829.989828	-27.50

CUADRO DE LOCALIZACIÓN DE PILOTES

Consecutivo Pilote	CoordenadaX	CoordenadaY	Profundidad
131	105566.88473	112826.364802	-27.50
132	105573.20921	112821.630781	-27.50
133	105579.53369	112816.89676	-27.50
134	105585.85817	112812.162739	-27.50
135	105592.18265	112807.428718	-27.50
136	105598.507129	112802.694697	-27.50
137	105604.091238	112798.514861	-27.50
138	105606.738998	112796.470495	-27.50
139	105612.129476	112792.970998	-27.50
140	105558.410412	112825.138392	-27.50
141	105562.419243	112822.150207	-27.50
142	105570.392767	112817.868115	-27.50
143	105576.717247	112813.134094	-27.50
144	105583.041727	112808.400073	-27.50
145	105589.366207	112803.666052	-27.50
146	105595.690687	112798.932031	-27.50
147	105600.608252	112793.591656	-27.50
148	105605.951005	112793.303837	-27.50
149	105556.139287	112822.104251	-27.50
150	105560.142112	112819.108043	-27.50
151	105567.306671	112813.745203	-27.50
152	105573.631151	112809.011182	-27.50
153	105579.955631	112804.277161	-27.50
154	105586.280111	112799.54314	-27.50
155	105592.604591	112794.809119	-27.50
156	105582.743015	112846.962746	-27.50
157	105617.382145	112792.688032	-27.50

NOTA:

La longitud ó profundidad del pilote deberá ser revisada y aprobada en obra por el Ingeniero de Suelos para garantizar que la capacidad del elemento sea la establecida en el estudio de suelos.

V°B° INGENIERO DE SUELOS

CONCRETO

f'c=28 MPa
f'c=280 kg/cm²
f'c=4000 psi

CONVENCIONES

- Indica muros e=0.25m
- Indica muros e=0.30m
- Indica muros e=0.35m
- Indica muros e=0.50m
- Indica columnas
- Indica muros de contención
- (#) Indica Tipo de Pilote
- Pr = Indica carga real en toneladas
- z = Indica profundidad de la punta del pilote medida desde el nivel 0.00-cota 2613.70 M.S.N.M

NOTAS

1. Ver detalles generales en el PL.N° 2002
2. Ver detalles y cuadro de pilotes en el PL. N° 2101
3. Ver plano de localización general de pilotes en el PL. N° 2100

EST - 2102-PP-P1
VERSIÓN PLANO V-02
OBRA No. 1157

CONSTRUCCIONES PLANIFICADAS
Carrera 13 No. 26A - 47 Piso 2
PBX: 339 41 11 Fax: 287 62 16

Robledales RESERVADO

CONTIENE:

NOMBRE DEL PROYECTO
ROBLEDALES-TORRE PALMERI I

Dirección AK 7 134 06

PLANTA LOCALIZACIÓN DE PILOTES CON COORDENADAS

ESCALA: INDICADA

ARCHIVO: 1157-EST-2102-PP-P1-PLANTA LOCALIZACIÓN DE PILOTES CON COORDENADAS.DWG
FECHA: 11/03/2026
DIBUJADO POR: KAREN CASTILLO

DISEÑADOR ESTRUCTURAL
ROBERTO AYCARDI FONSECA
TP: 2520257258 CND

DISEÑADOR DE ELMENTOS NO ESTRUCTURALES
VICTOR H. DÁVILA F.
TP: 2520122782 CND

REVISOR ESTRUCTURAL
NICOLAS PARRA GARCIA
TP: 25202-62063 CND

CONSTRUCTOR RESPONSABLE
ALVARO DÍAZ ULLOA
TP: 2520275046 CND

CONSTRUCCIONES PLANIFICADAS
GERENTE DE DISEÑO

DIRECTOR DE ARQUITECTURA
ANDRÉS VALCARCEL

DIRECTOR DE INGENIERÍA
MARIO FERNANDO RIVERA

DIRECTOR DE PRESUPUESTOS
JAVIER CLAVIJO

EQUIPO DISEÑO CPSA
MP, CO, LL, EC.

MODIFICACIONES

#	Fecha	Emitida por	Modificación
1	11/03/2026	B	se incluyen columnas para manejo de voladizo y se ajustan secciones de vigas.

VERSIONES DE PLANOS

Versión	Fecha
V-01	12/02/2026
V-02	11/03/2026

PROPÓSITO DE LA EMISIÓN

DRAFT	
Coordinación Técnica	
Revisión	
Construcción	✖
Curaduría	
Presupuestos	

MODELO FUENTE: 1157_ROBL-BOG_VIV_ESTR_TP1
17/03/2026

VERSIÓN MODELO: FASE III / V-03

EST - 2102-PP-P1
VERSIÓN PLANO V-02
OBRA No. 1157