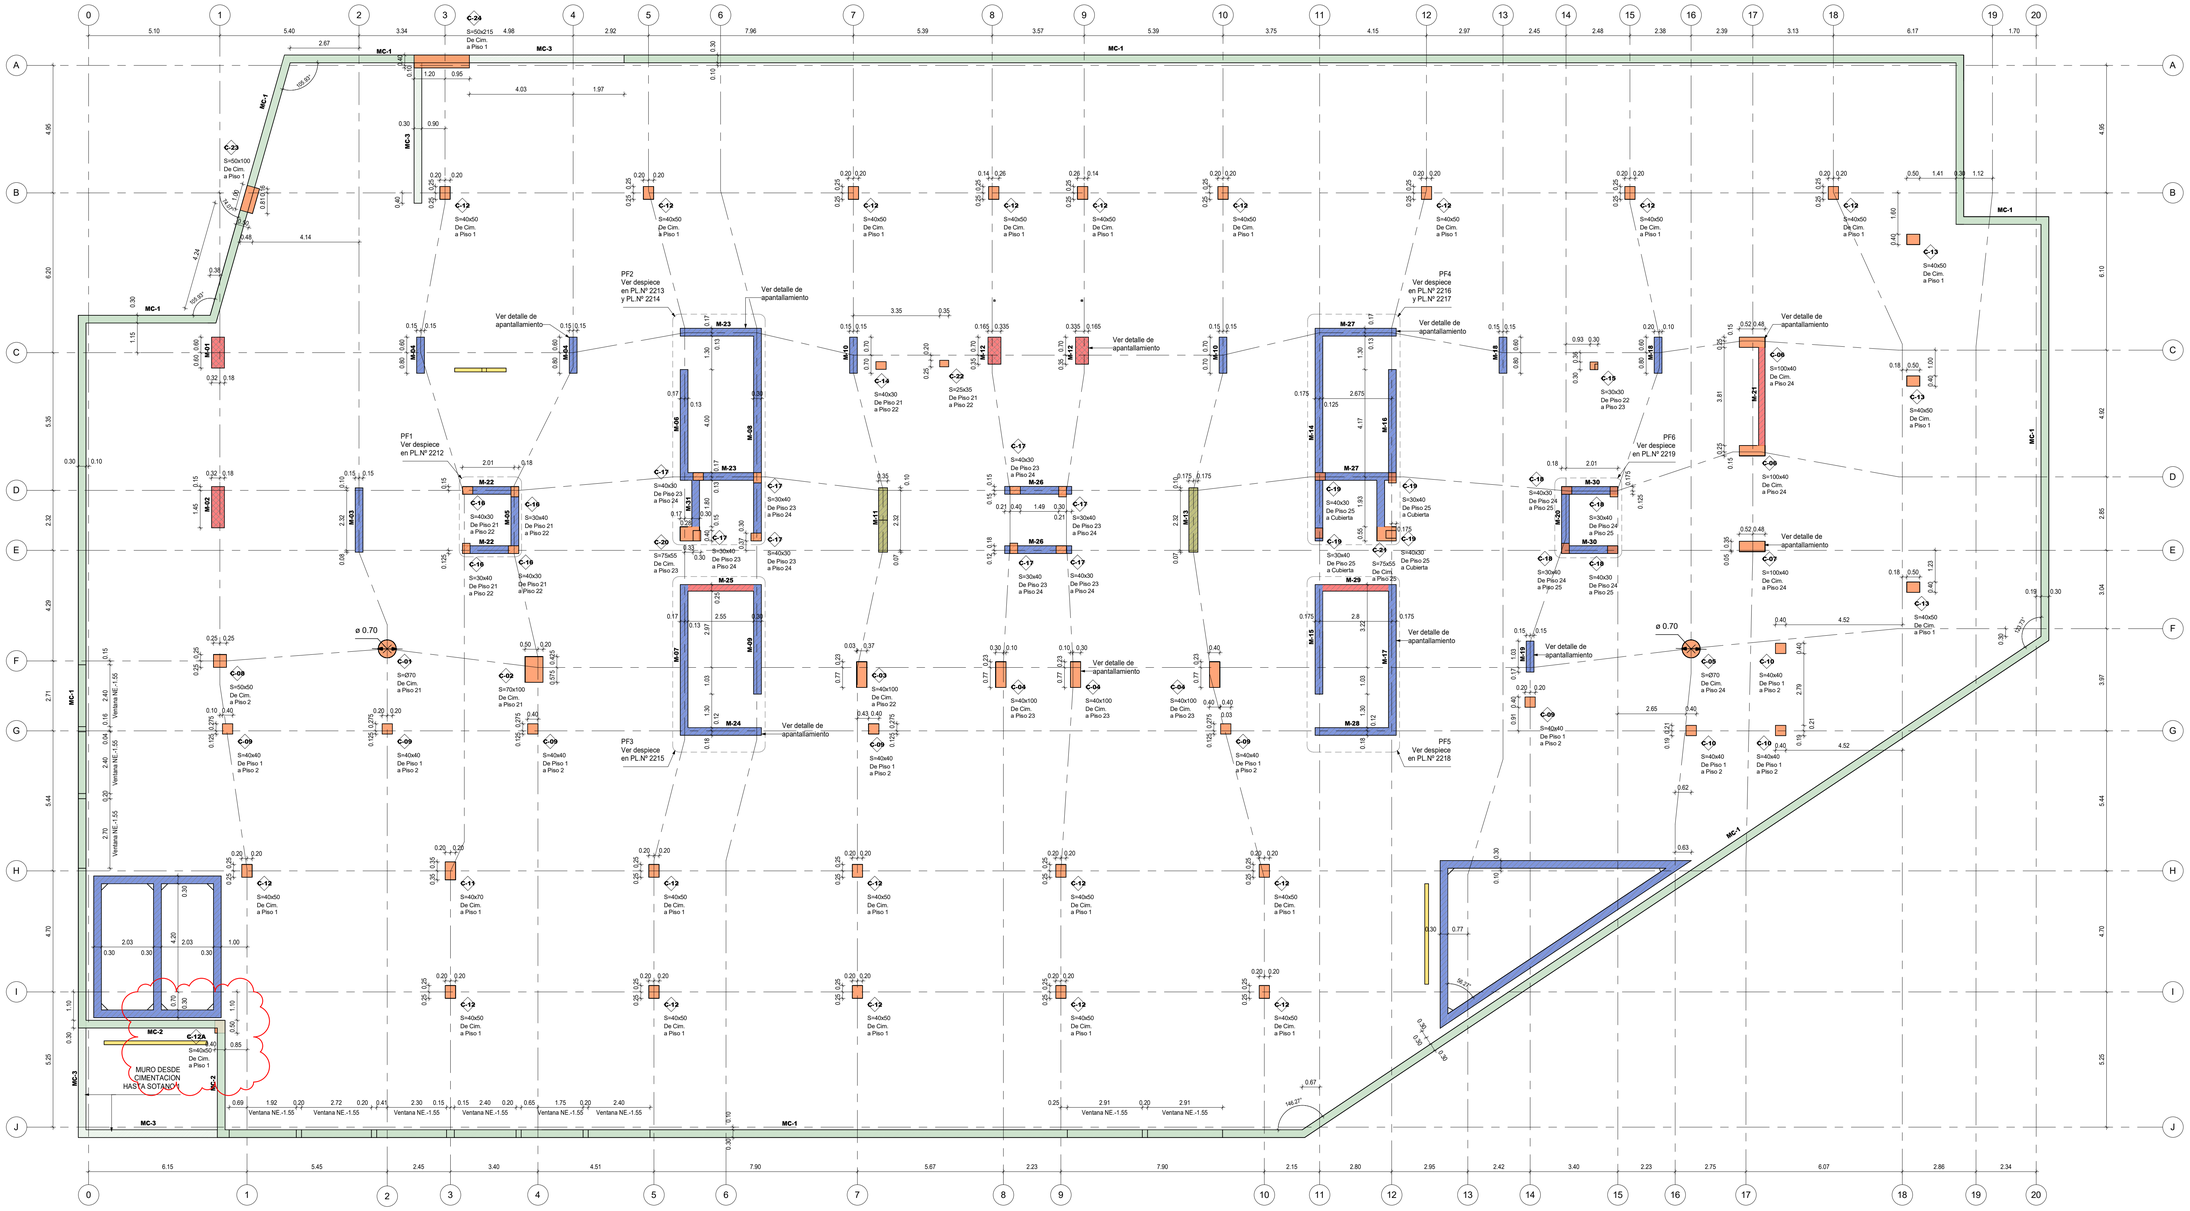

PLANTA LOCALIZACIÓN DE MUROS Y COLUMNAS

Escala 1 : 100

CONCRETO MUROS-COLUMNAS				
• CIM A PISO 4	• PISO 4 A PISO 8	• PISO 8 A PISO 12	• PISO 12 A PISO 16	• PISO 16 A CUBIERTA
f'c=56 MPa	**f'c=49 MPa**	**f'c=42 MPa**	**f'c=35 MPa**	**f'c=28 MPa**
f'c=560 kg/cm²	**f'c=490 kg/cm²**	**f'c=420 kg/cm²**	**f'c=350 kg/cm²**	**f'c=280 kg/cm²**
f'c=8000 psi	**f'c=7000 psi**	**f'c=6000 psi**	**f'c=5000 psi**	**f'c=4000 psi**

NOTAS

1. Ver detalles generales en el PL.N° 2002
2. Ver despieces de columnas en los PL.N° 2201 - PL.N° 2203
3. Ver despieces de muros en los PL.N° 2204 - PL.N° 2219
4. Ver detalles de muros de contención en el PL.N° 2220

CONVENCIONES

- Indica muros e=0.25m
- Indica muros e=0.30m
- Indica muros e=0.35m
- Indica muros e=0.50m
- Indica columnas
- Indica muros de contención nivel NE.-6.40
- Indica muros de contención nivel NE.-3.20
- 00 Indica Tipo de Columna
- M-# Indica Tipo de Muro

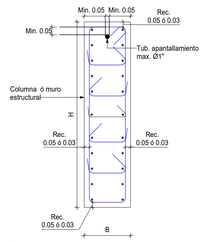

NOTAS:

1. La tubería no debe entrar en contacto con ningún refuerzo estructural.
2. Se debe garantizar una separación mínima de 5cm respecto a cualquier barra longitudinal o transversal.
3. En ningun caso se debe ubicar la tuberia en la zona de recubrimiento indicada en los planos estructurales.
4. La posición de la tuberia debe consultarse en los planos eléctricos de apantallamiento.

DETALLE PARA LA TUBERIA DE APANTALLAMIENTO
Sin escala

EST - 2200-PP-P1

VERSIÓN PLANO V-03

OBRA No. 1157

CONSTRUCCIONES PLANIFICADAS
Carrera 13 No. 26A - 47 Piso 2
PBX: 339 41 11 Fax: 287 02 16

Robledales
RESERVADO

CONTIENE:

NOMBRE DEL PROYECTO
ROBLEDALES-TORRE PALMERI 1

Dirección AK 7 134 06

PLANTA LOC. DE MUR Y COL

ESCALA: INDICADA

ARCHIVO: 1157-EST-2200-PP-P1-PLANTA LOC. DE MUR Y COL.DWG

FECHA:	DIBUJADO POR:
17/03/2026	ANDRES DUARTE

DISEÑADOR ESTRUCTURAL
ROBERTO AYCARDI FONSECA
TP: 2520257258 CND

DISEÑADOR DE ELMENTOS NO ESTRUCTURALES
VICTOR H. DÁVILA F.
TP: 2520122782 CND

REVISOR ESTRUCTURAL
NICOLAS PARRA GARCIA
TP: 25202-62063 CND

CONSTRUCTOR RESPONSABLE
ALVARO DÍAZ ULLOA
TP: 2520275046 CND

CONSTRUCCIONES PLANIFICADAS

GERENTE DE DISEÑO

DIRECTOR DE ARQUITECTURA
ANDRÉS VALCARCEL

DIRECTOR DE INGENIERÍA
MARIO FERNANDO RIVERA

DIRECTOR DE PRESUPUESTOS
JAVIER CLAVIJO

EQUIPO DISEÑO CPSA
MP, CO, LL, EC.

MODIFICACIONES

#	Fecha	Emitida por	Modificación
1	11/03/2026	B	se incluyen columnas para manejo de voladizo y se ajustan secciones de vigas.
2	17/03/2026	B	Se incluye etiqueta para columna C12-A

VERSIONES DE PLANOS

Versión	Fecha
V-01	12/02/2026
V-02	11/03/2026
V-03	17/03/2026

PROPÓSITO DE LA EMISIÓN

DRAFT	
Coordinación Técnica	
Revisión	
Construcción	✖
Curaduría	
Presupuestos	

MODELO FUENTE:	VERSIÓN MODELO:
1157_ROBL-BOG_VIV_ESTR_TP1 17/03/2026	FASE III / V-03

EST - 2200-PP-P1

VERSIÓN PLANO V-03

OBRA No. 1157