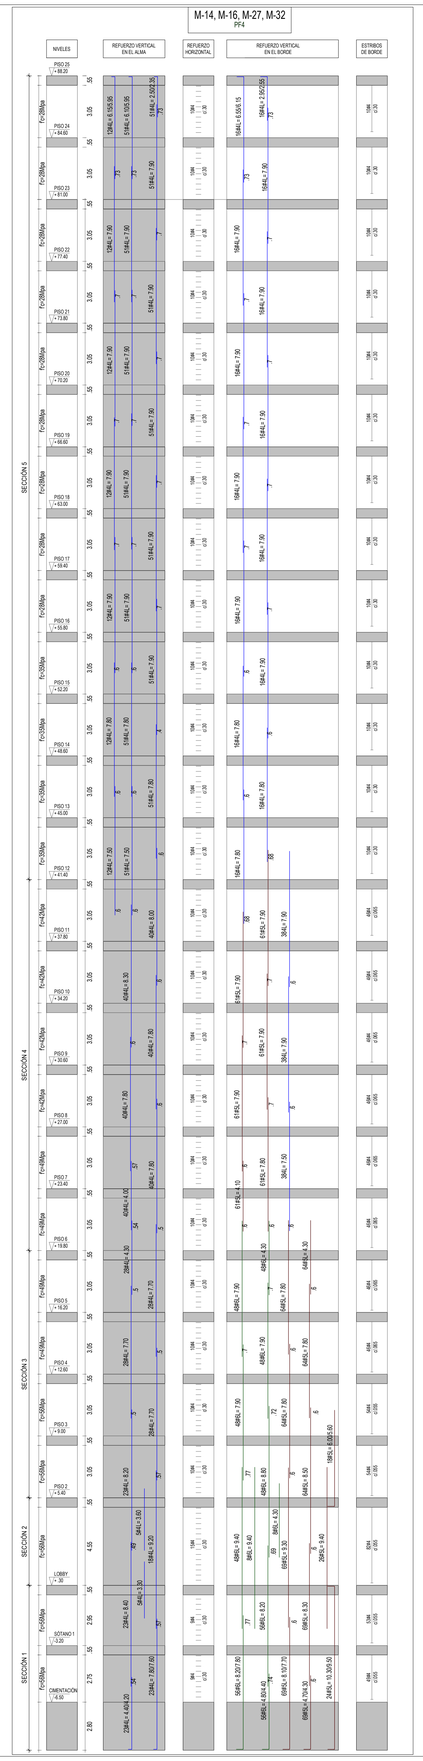


SECCIÓN 1 (CIMENTACIÓN-PISO 1)

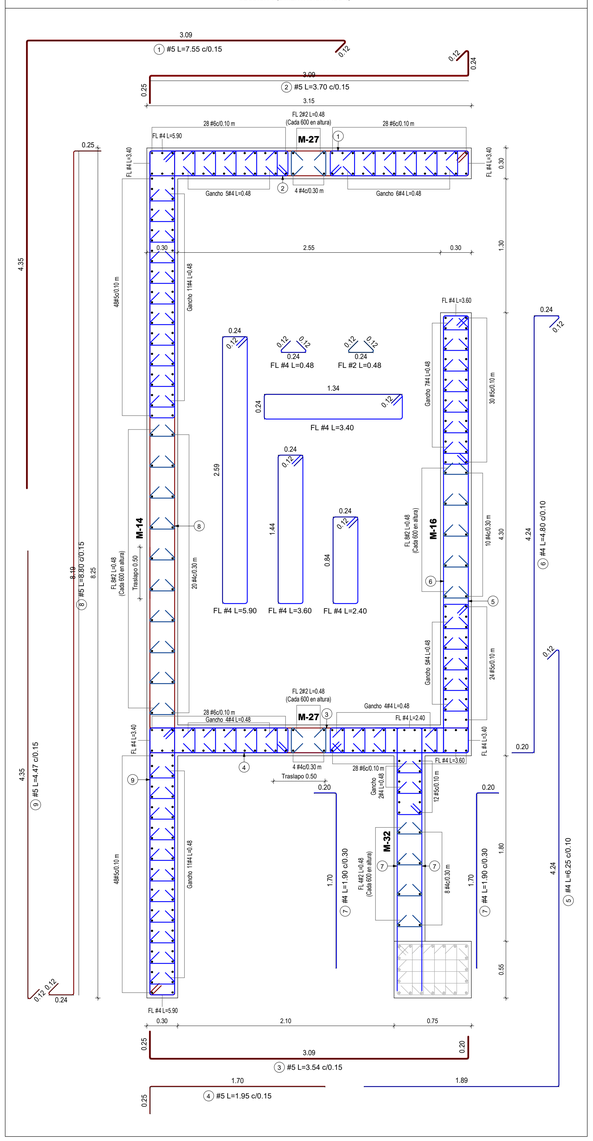


SECCIÓN 2 (PISO 1-PISO 2)

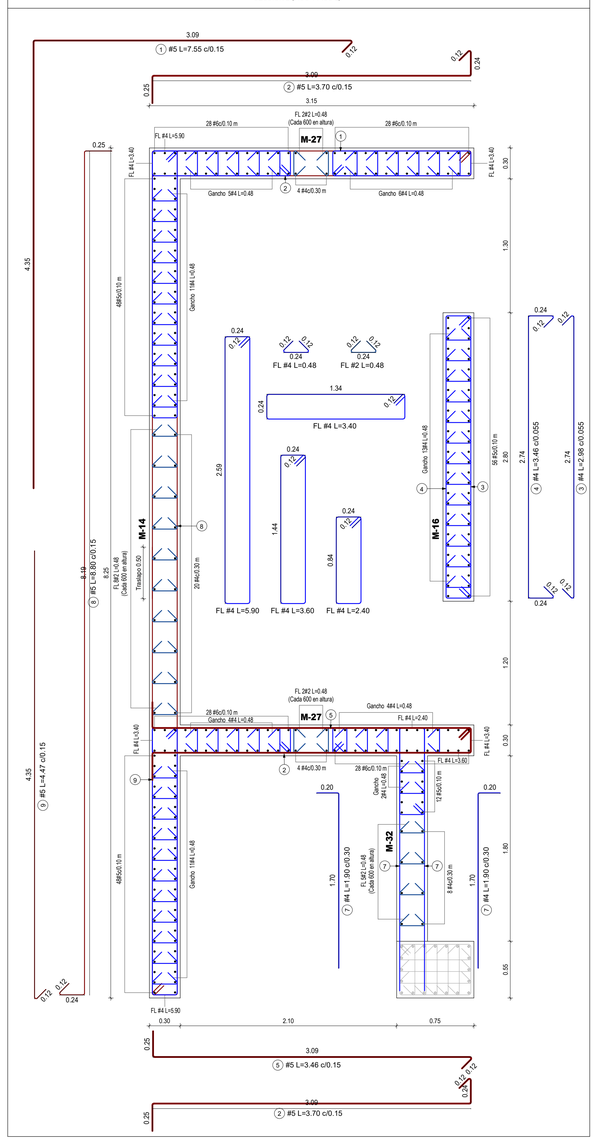


**NOTAS**

1. Ver detalles generales en el PL.N° 2002
2. Ver planta de localización de muros y columnas en el PL.N° 2200

**ESCALAS**

- Alzado___ 1:150
- Secciones_1:25

| MODELO FUENTE: | VERSIÓN MODELO: |
|---|---|
| 1157_ROBL-BOG_VIV_ESTR_TP1<br>17/03/2026 | FASE III / V-03 |

EST - 2216-PD-P1

VERSIÓN PLANO V-01

OBRA No. 1157

EST - 2216-PD-P1

VERSIÓN PLANO V-01

OBRA No. 1157

CONSTRUCCIONES PLANIFICADAS
Carrera 13 No. 26A - 47 Piso 2
PBX: 339 41 11 Fax: 287 02 16

Robledales
RESERVADO

CONTIENE:

NOMBRE DEL PROYECTO
ROBLEDALES-TORRE PALMERI 1

Dirección AK 7 134 06

DESPICES DE MUROS

ESCALA: INDICADA

| ARCHIVO: | 1157-EST-2216-PD-P1-DESPICES DE MUROS.DWG |
|---|---|
| FECHA: 11/03/2026 | DIBUJADO POR: ANDRES DUARTE |

DISEÑADOR ESTRUCTURAL
ROBERTO AYCARDI FONSECA
TP: 2520257258 CND

DISEÑADOR DE ELMENTOS NO ESTRUCTURALES
VICTOR H. DÁVILA F.
TP: 2520122782 CND

REVISOR ESTRUCTURAL
NICOLAS PARRA GARCIA
TP: 25202-62063 CND

CONSTRUCTOR RESPONSABLE
ALVARO DÍAZ ULLOA
TP: 2520275046 CND

CONSTRUCCIONES PLANIFICADAS

GERENTE DE DISEÑO

DIRECTOR DE ARQUITECTURA
ANDRÉS VALCARCEL

DIRECTOR DE INGENIERÍA
MARIO FERNANDO RIVERA

DIRECTOR DE PRESUPUESTOS
JAVIER CLAVIJO

EQUIPO DISEÑO CPSA

MP, CO, LL, EC.

MODIFICACIONES

| # | Fecha | Emitida por | Modificación |
|---|---|---|---|

VERSIONES DE PLANOS

| Versión | Fecha |
|---|---|
| V-01 | 11/03/2026 |

PROPÓSITO DE LA EMISIÓN

| | |
|---|---|
| DRAFT | |
| Coordinación Técnica | |
| Revisión | |
| Construcción | ✖ |
| Curaduría | |
| Presupuestos | |