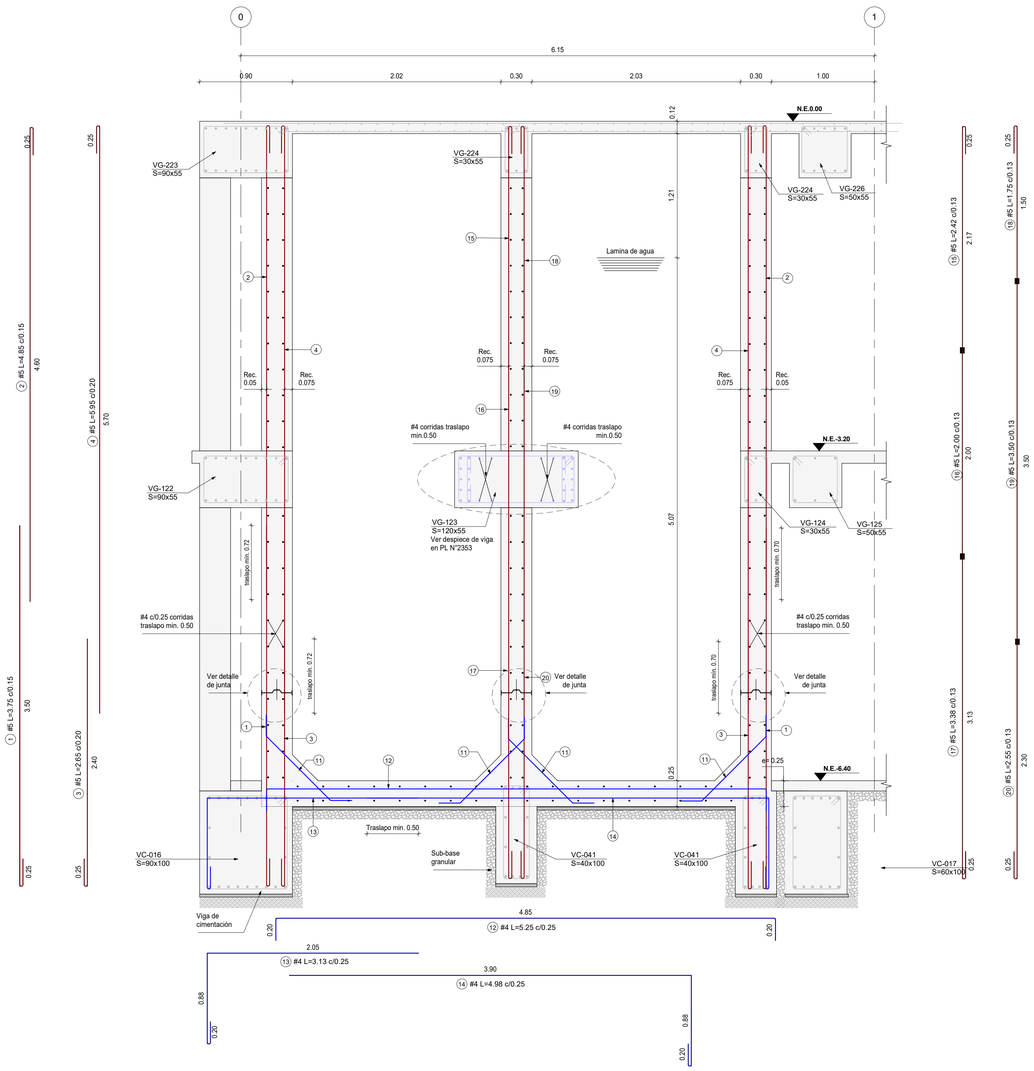

CORTE TQ2-TQ2
Escala 1 : 25

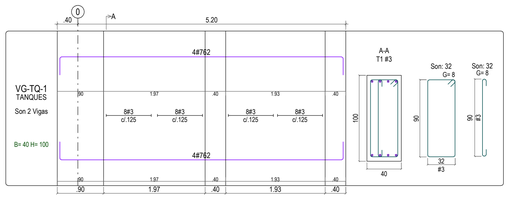

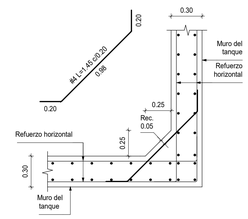

DETALLE 1 ESQUINA EN MURO DE TANQUE (PLANTA)
Escala 1 : 25

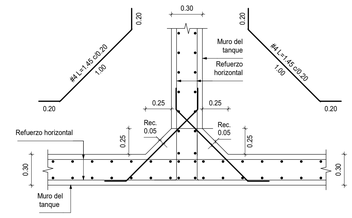

DETALLE 2 ESQUINA EN MURO DE TANQUE (PLANTA)
Escala 1 : 25

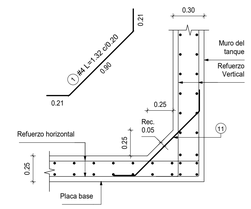

DETALLE ESQUINA EN MURO DE TANQUE (ALZADO) e= 0.30m
Escala 1 : 25

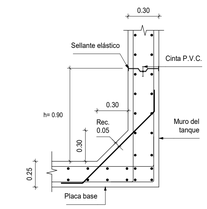

DETALLE DE JUNTA (ALZADO)
Escala 1 : 25

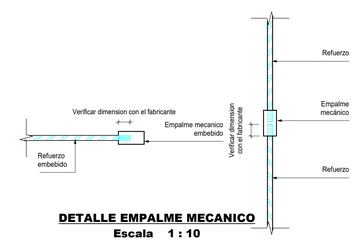

DETALLE EMPALME MECANICO
Escala 1 : 10

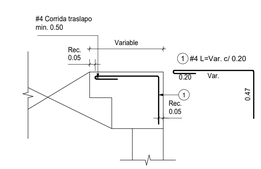

DETALLE 3 SOBRE ANCHO DE VIGA
Escala 1 : 25

CONCRETO

- **f'c=4000 Psi**
- **f'c=28 MPa**
- Relación A/C=<0.50
- Curado intensivo por lo menos durante 15 dias.

CONVENCIONES

Indica muros tanque e=0.30m

Indica muros de contención

NOTAS

1. Ver detalles generales en el PL.N° 2002
2. Ver planta de cimentación en el PL.N° 2300
3. Ver planta de tanque de agua potable en el PL.N° 2325
4. Ver corte TQ1-TQ1 en el PL.N° 2325

EST - 2326-PD-P1

VERSIÓN PLANO V-01

OBRA No. 1157

CONSTRUCCIONES PLANIFICADAS
Carrera 13 No. 26A - 47 Piso 2
PBX: 339 41 11 Fax: 287 02 16

Robledales RESERVADO

CONTIENE:

NOMBRE DEL PROYECTO
ROBLEDALES-TORRE PALMERI 1

Dirección AK 7 134 06

DESPIECES DE TANQUE 1

ESCALA: INDICADA

ARCHIVO: 1157-EST-2326-PD-P1-DESPIECES DE TANQUE 1.DWG

FECHA:	DIBUJADO POR:
20/02/2026	KAREN CASTILLO

DISEÑADOR ESTRUCTURAL
ROBERTO AYCARDI FONSECA
TP: 2520257258 CND

DISEÑADOR DE ELMENTOS NO ESTRUCTURALES
VICTOR H. DÁVILA F.
TP: 2520122782 CND

REVISOR ESTRUCTURAL
NICOLAS PARRA GARCIA
TP: 25202-62063 CND

CONSTRUCTOR RESPONSABLE
ALVARO DÍAZ ULLOA
TP: 2520275046 CND

CONSTRUCCIONES PLANIFICADAS

GERENTE DE DISEÑO

DIRECTOR DE ARQUITECTURA
ANDRÉS VALCARCEL

DIRECTOR DE INGENIERÍA
MARIO FERNANDO RIVERA

DIRECTOR DE PRESUPUESTOS
JAVIER CLAVIJO

EQUIPO DISEÑO CPSA
MP, CO, LL, EC.

MODIFICACIONES

#	Fecha	Emitida por	Modificación

VERSIONES DE PLANOS

Versión	Fecha
V-01	20-02-2026

PROPÓSITO DE LA EMISIÓN

DRAFT	
Coordinación Técnica	
Revisión	
Construcción	✖
Curaduría	
Presupuestos	

MODELO FUENTE: 1157_ROBL-BOG_VIV_ESTR_TP1
17/03/2026

VERSIÓN MODELO: FASE III / V-03

EST - 2326-PD-P1

VERSIÓN PLANO V-01

OBRA No. 1157