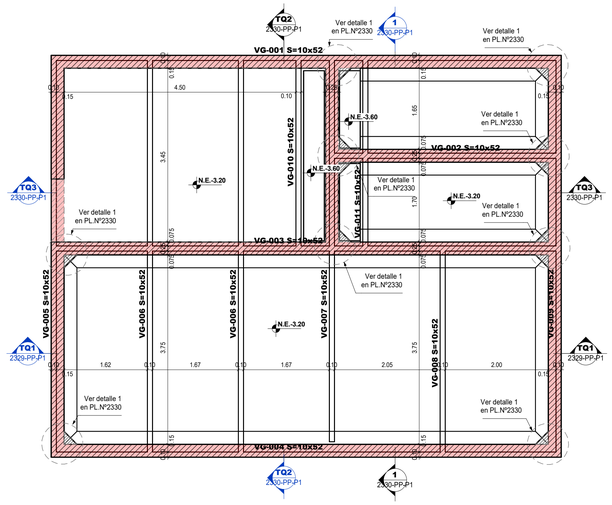

PLANTA DE CIMENTACIÓN TANQUE EXTERNO
Escala 1 : 50

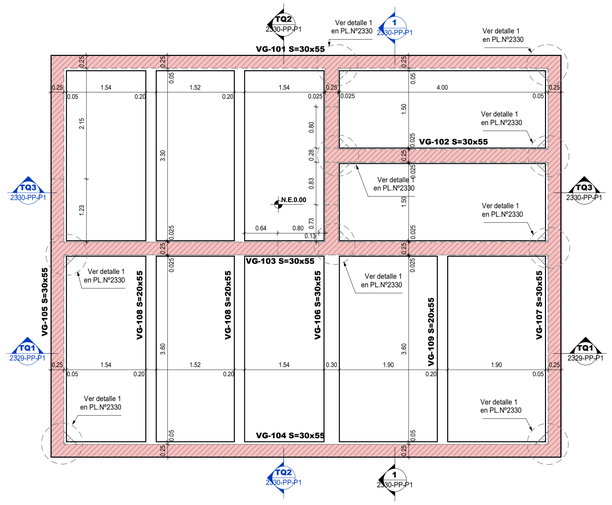

PLANTA TAPA TANQUE EXTERNO
Escala 1 : 50

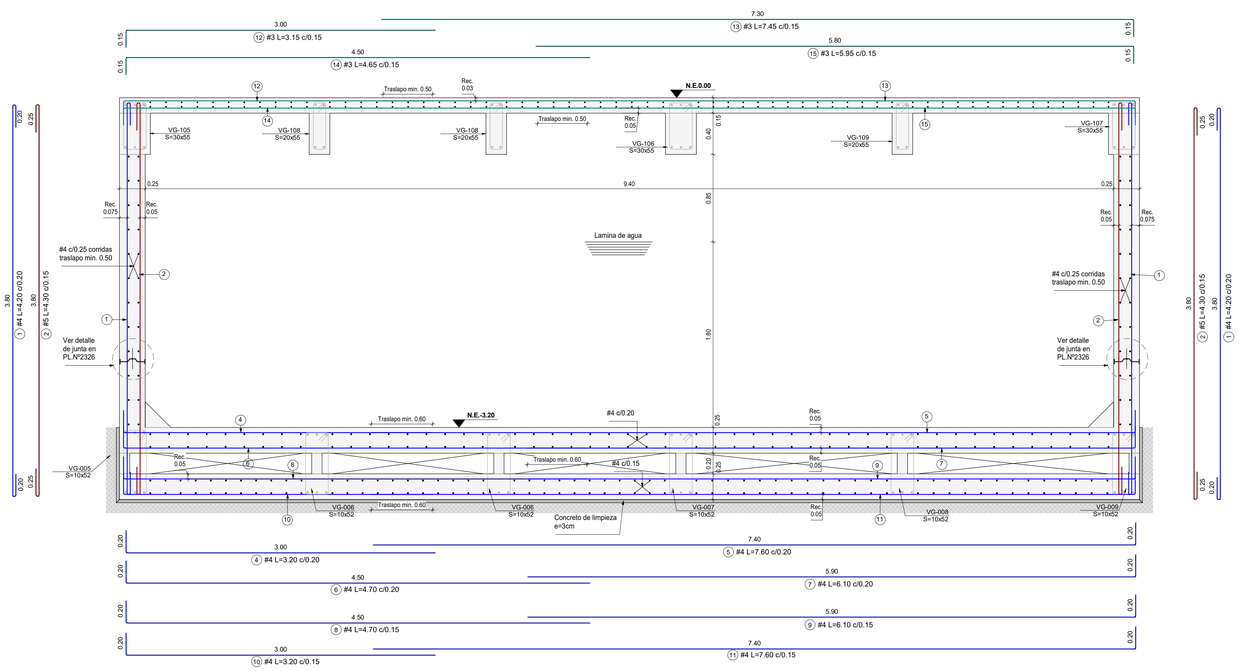

CORTE TANQUE EXTERNO TQ1
Escala 1 : 25

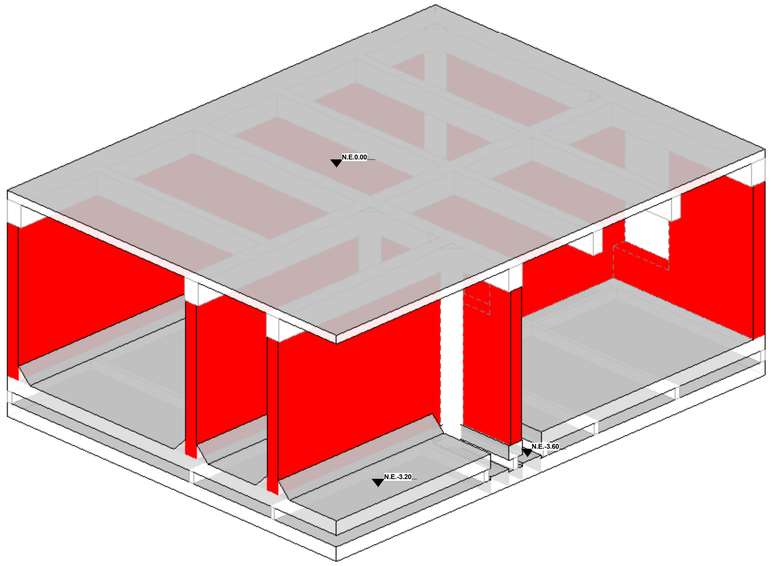

ESQUEMA 3D TANQUE EXTERNO
Sin escala

CONCRETO

- **f'c=5000 Psi**
- **f'c=35 MPa**
- Relación A/C=<0.50
- Curado intensivo por lo menos durante 15 dias.

CONVENCIONES

Indica muros tanque e=0.25m

NOTAS

1. Ver detalles generales en el PL.N° 2002
2. Ver cortes TQ en el PL.N° 2330
3. Ver detalles de tanque en el PL.N° 2330
4. Ver despieces de vigas TQ en el PL.N° 2331

NOTA:
Este plano debe ser revisado y aprobado por el Ingeniero de suelos.

V°B° INGENIERO DE SUELOS

EST - 2329-PP-P1
VERSIÓN PLANO V-01
OBRA No. 1157

CONSTRUCCIONES PLANIFICADAS
Carrera 13 No. 26A - 47 Piso 2
PBX: 339 41 11 Fax: 287 62 16

Robledales
RESERVADO

CONTIENE:

NOMBRE DEL PROYECTO
ROBLEDALES-TORRE PALMERI 1

Dirección AK 7 134 06

DESPIECES TANQUE EXTERNO

ESCALA: INDICADA

ARCHIVO: 1157-EST-2329-PP-P1-DESPIECES TANQUE EXTERNO.DWG

FECHA:	DIBUJADO POR:
11/03/2026	JOAN GAMBOA

DISEÑADOR ESTRUCTURAL
ROBERTO AYCARDI FONSECA
TP: 2520257258 CND

DISEÑADOR DE ELMENTOS NO ESTRUCTURALES
VICTOR H. DÁVILA F.
TP: 2520122782 CND

REVISOR ESTRUCTURAL
NICOLAS PARRA GARCIA
TP: 25202-62063 CND

CONSTRUCTOR RESPONSABLE
ALVARO DÍAZ ULLOA
TP: 2520275046 CND

CONSTRUCCIONES PLANIFICADAS
GERENTE DE DISEÑO
DIRECTOR DE ARQUITECTURA
ANDRÉS VALCARCEL
DIRECTOR DE INGENIERÍA
MARIO FERNANDO RIVERA
DIRECTOR DE PRESUPUESTOS
JAVIER CLAVIJO

EQUIPO DISEÑO CPSA
MP, CO, LL, EC.

MODIFICACIONES

#	Fecha	Emitida por	Modificación

VERSIONES DE PLANOS

Versión	Fecha
V-01	11/03/2026

PROPÓSITO DE LA EMISIÓN

DRAFT	
Coordinación Técnica	
Revisión	
Construcción	X
Curaduría	
Presupuestos	

MODELO FUENTE: 1157_ROBL-BOG_VIV_ESTR_TP1
17/03/2026

VERSIÓN MODELO: FASE III / V-03

EST - 2329-PP-P1
VERSIÓN PLANO V-01
OBRA No. 1157