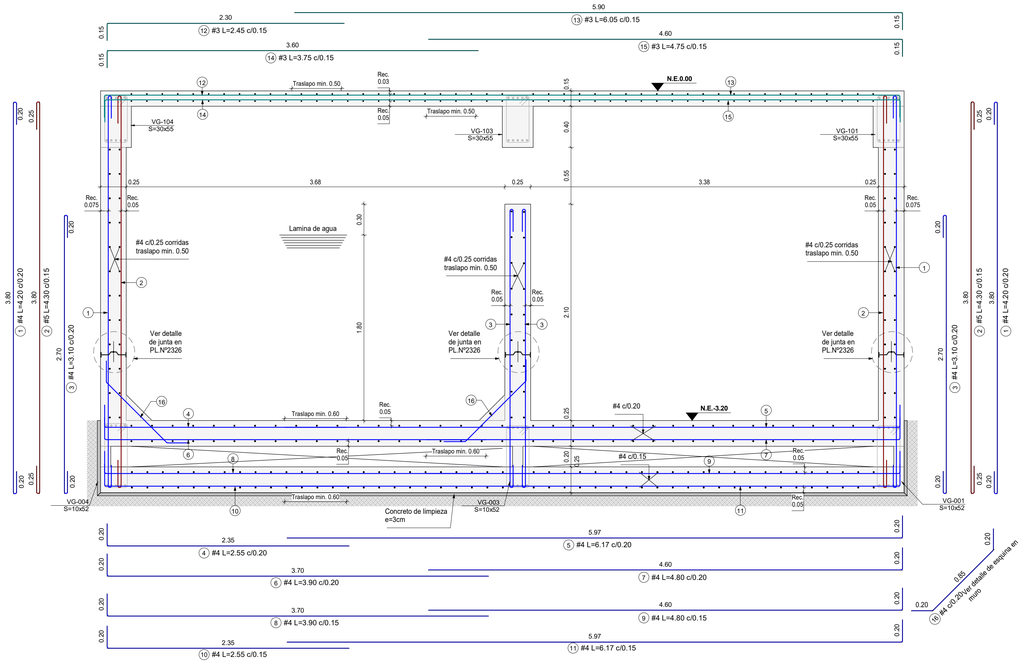

CORTE TANQUE EXTERNO TQ2

Escala 1 : 25

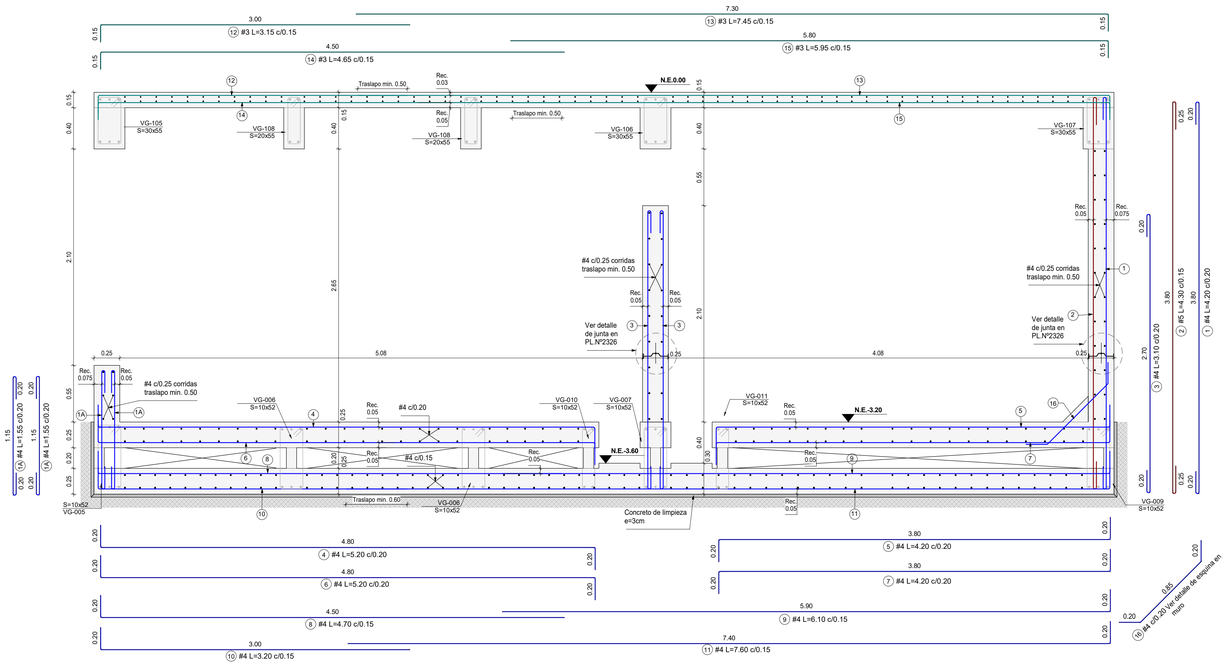

CORTE TANQUE EXTERNO TQ3

Escala 1 : 25

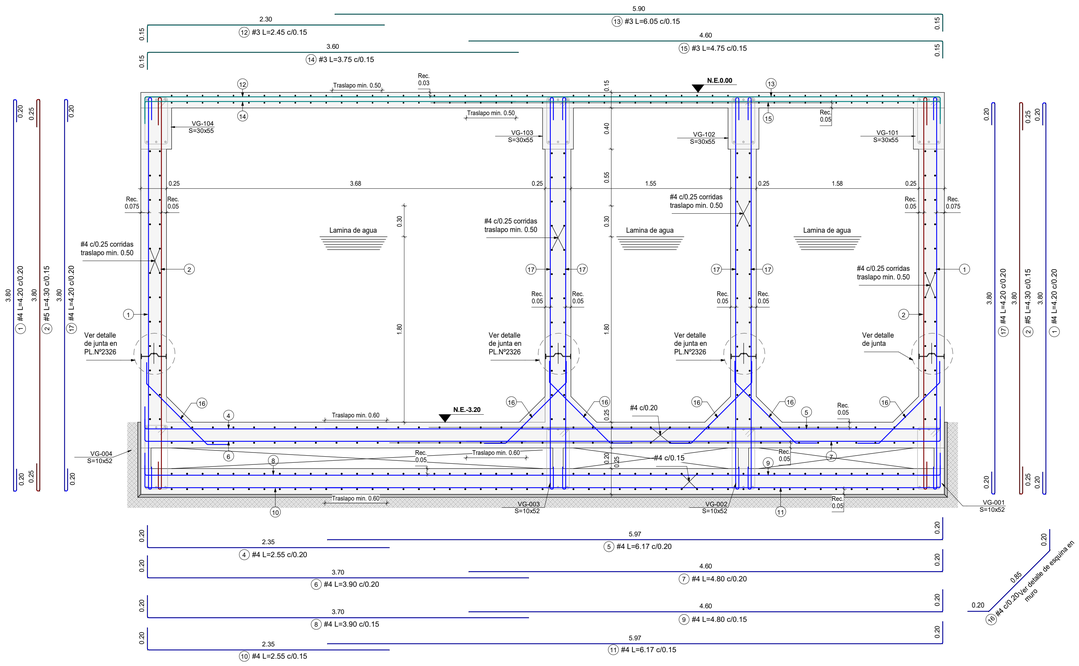

CORTE TANQUE EXTERNO TQ4

Escala 1 : 25

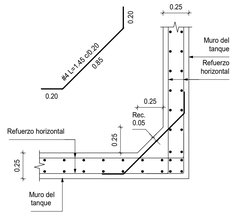

DETALLE 1 ESQUINA EN MURO DE TANQUE (PLANTA)

Escala 1 : 25

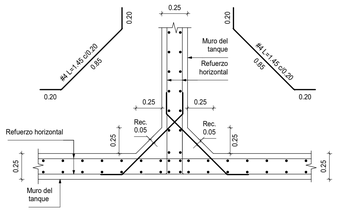

DETALLE 2 ESQUINA EN MURO DE TANQUE (PLANTA)

Escala 1 : 25

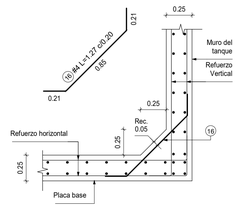

DETALLE ESQUINA EN MURO DE TANQUE (ALZADO) e= 0.25m

Escala 1 : 25

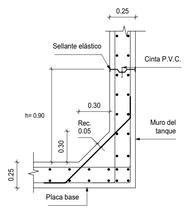

DETALLE DE JUNTA (ALZADO)

Escala 1 : 25

CONCRETO

- **f'c=5000 Psi**
- **f'c=35 MPa**
- Relación A/C=<0.50
- Curado intensivo por lo menos durante 15 días.

CONVENCIONES

Indica muros tanque e=0.25m

NOTAS

1. Ver detalles generales en el PL.N° 2002
2. Ver plantas en el PL.N° 2329
3. Ver corte TQ1 en el PL.N° 2329
4. Ver despieces de vigas TQ en el PL.N° 2331

NOTA:
Este plano debe ser revisado y aprobado por el Ingeniero de suelos.

VºBº INGENIERO DE SUELOS

EST - 2330-PP-P1

VERSIÓN PLANO V-01

OBRA No. 1157

CONSTRUCCIONES PLANIFICADAS
Carrera 13 No. 26A - 47 Piso 2
PBX: 339 41 11 Fax: 287 02 16

Robledales RESERVADO

CONTIENE:

NOMBRE DEL PROYECTO
ROBLEDALES-TORRE PALMERI 1

Dirección AK 7 134 06

DESPIECES TANQUE EXTERNO

ESCALA: INDICADA

ARCHIVO: 1157-EST-2330-PP-P1-DESPIECES TANQUE EXTERNO.DWG

FECHA:	DIBUJADO POR:
11/03/2026	JOAN GAMBOA

DISEÑADOR ESTRUCTURAL
ROBERTO AYCARDI FONSECA
TP: 2520257258 CND

DISEÑADOR DE ELMENTOS NO ESTRUCTURALES
VICTOR H. DÁVILA F.
TP: 2520122782 CND

REVISOR ESTRUCTURAL
NICOLAS PARRA GARCIA
TP: 25202-62063 CND

CONSTRUCTOR RESPONSABLE
ALVARO DÍAZ ULLOA
TP: 2520275046 CND

CONSTRUCCIONES PLANIFICADAS

GERENTE DE DISEÑO

DIRECTOR DE ARQUITECTURA
ANDRÉS VALCARCEL

DIRECTOR DE INGENIERÍA
MARIO FERNANDO RIVERA

DIRECTOR DE PRESUPUESTOS
JAVIER CLAVIJO

EQUIPO DISEÑO CPSA
MP, CO, LL, EC.

MODIFICACIONES

#	Fecha	Emitida por	Modificación

VERSIONES DE PLANOS

Versión	Fecha
V-01	11/03/2026

PROPÓSITO DE LA EMISIÓN

DRAFT	
Coordinación Técnica	
Revisión	
Construcción	✖
Curaduría	
Presupuestos	

MODELO FUENTE: 1157_ROBL-BOG_VIV_ESTR_TP1
17/03/2026

VERSIÓN MODELO: FASE III / V-03

EST - 2330-PP-P1
VERSIÓN PLANO V-01
OBRA No. 1157