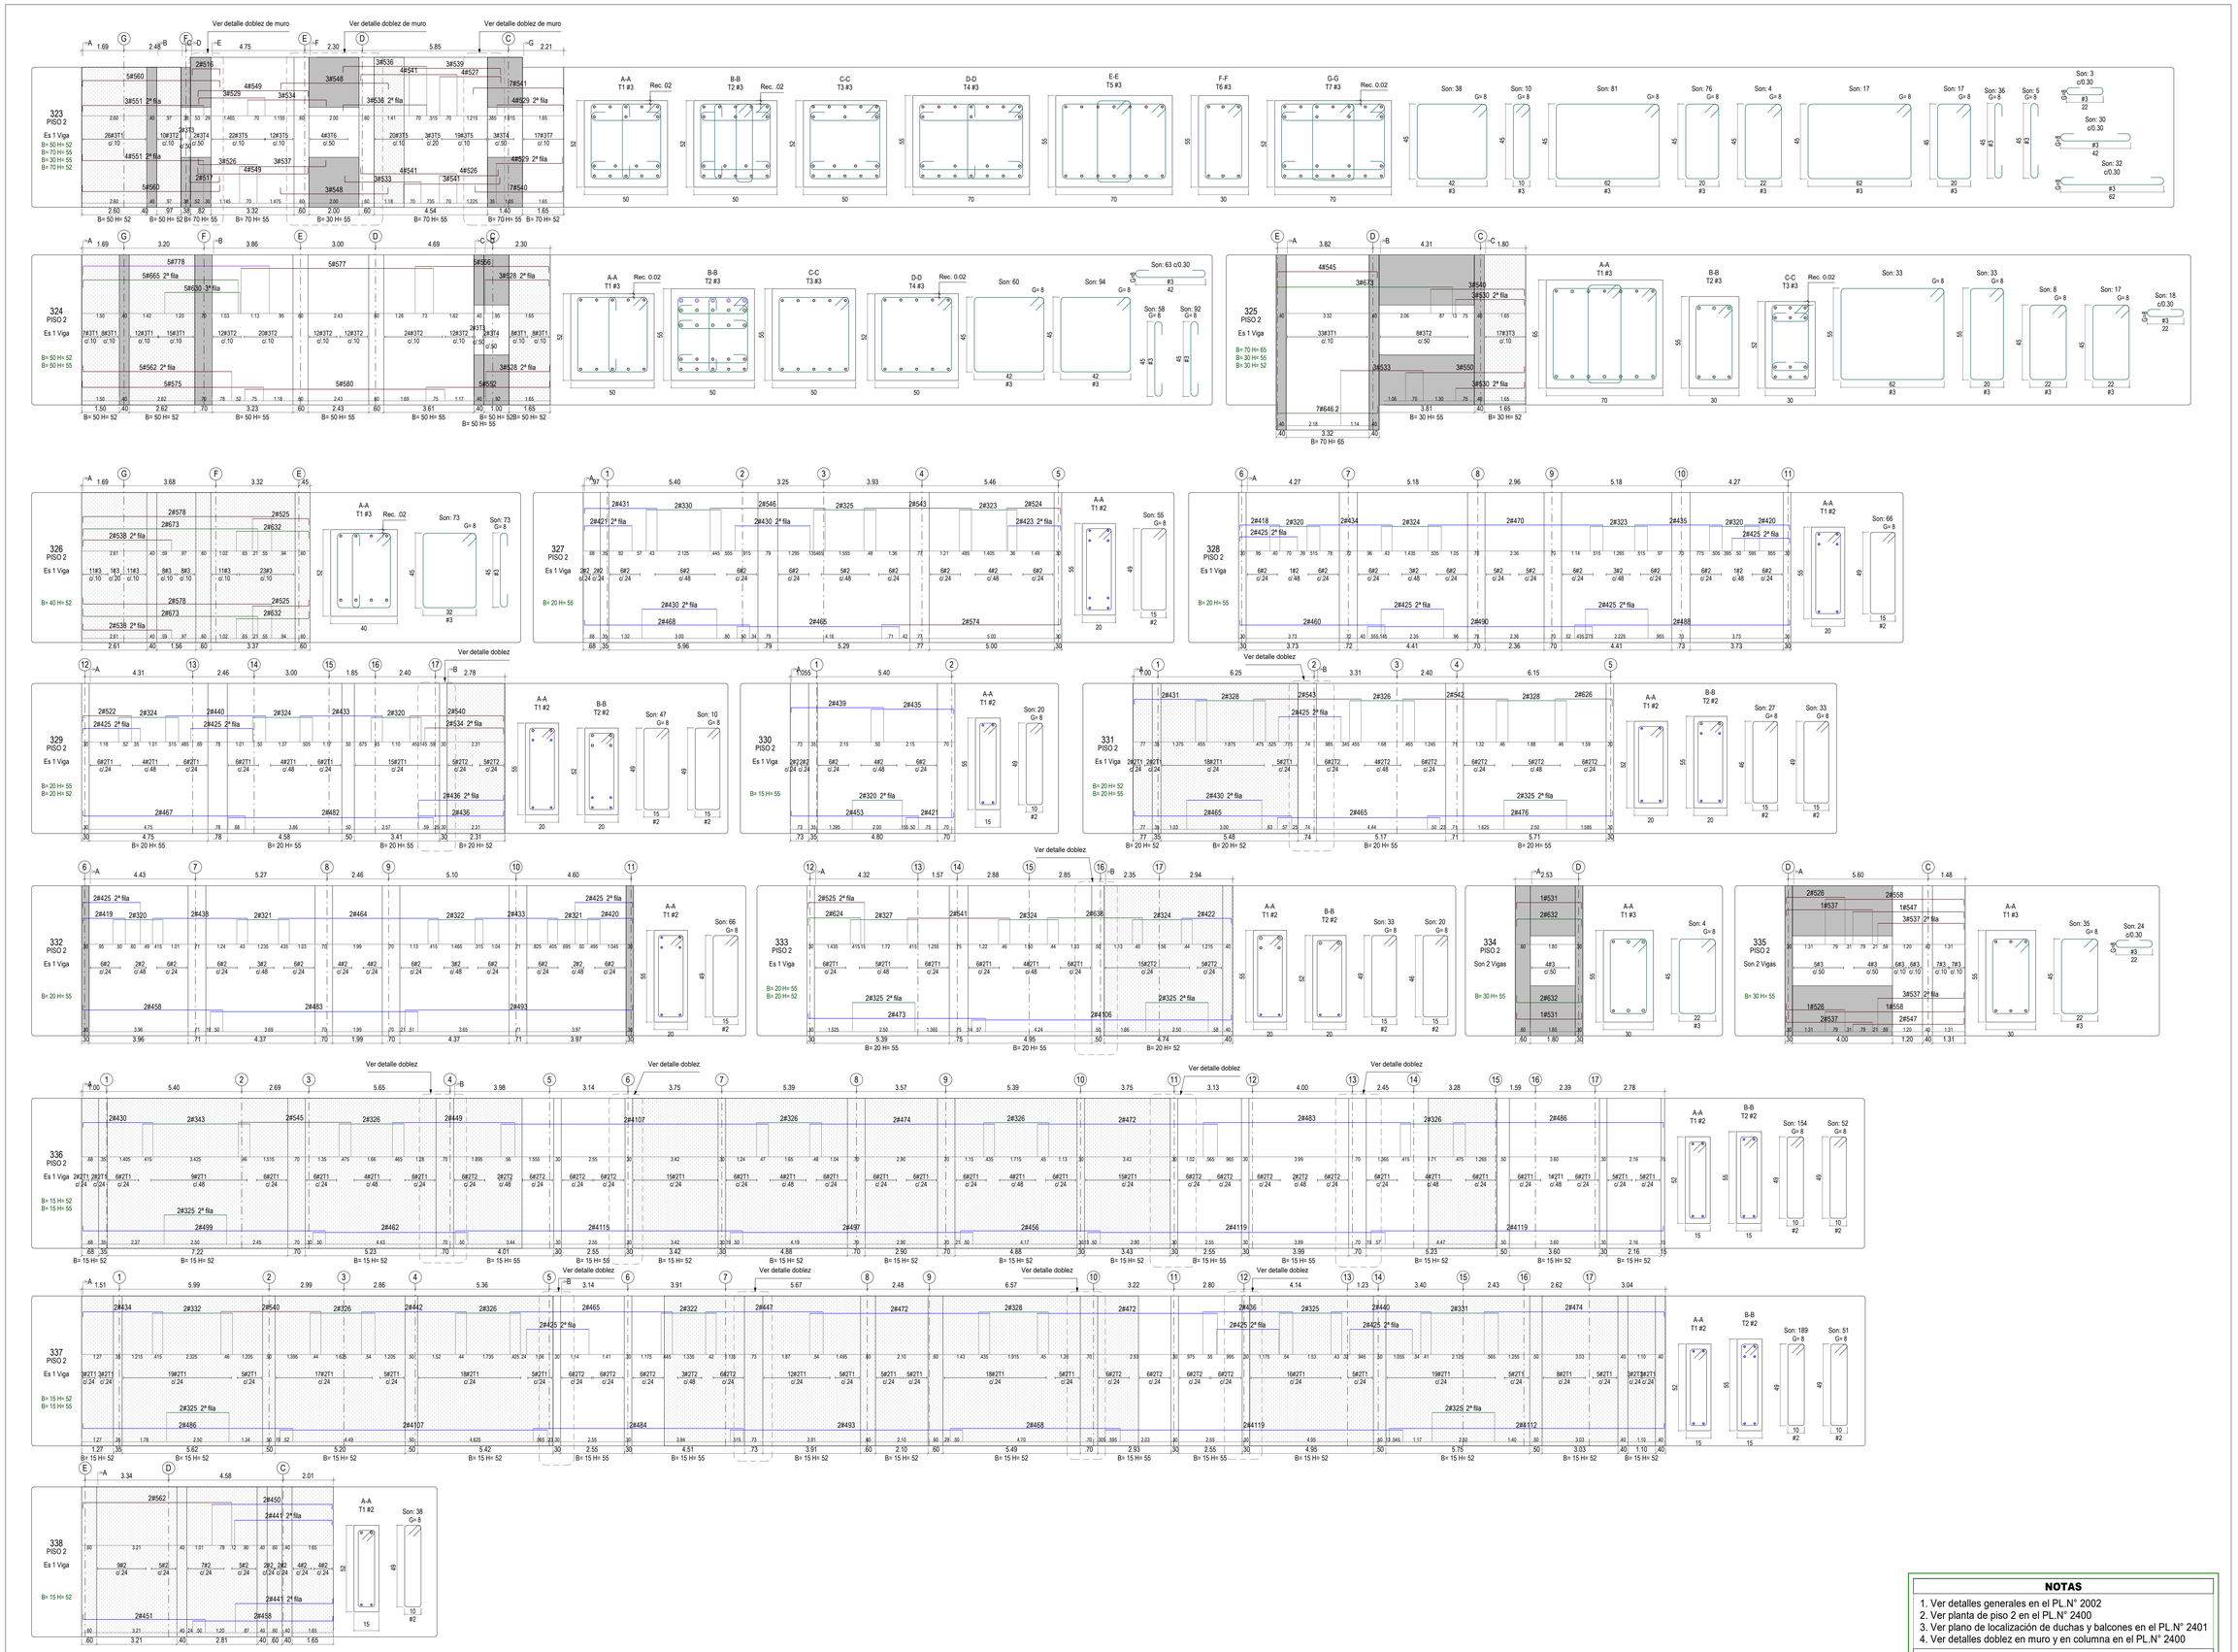


## NOTAS

1. Ver detalles generales en el PL.N° 2002
2. Ver planta de piso 2 en el PL.N° 2400
3. Ver plano de localización de duchas y balcones en el PL.N° 2401
4. Ver detalles doblez en muro y en columna en el PL.N° 2400

## CONVENCIONES

Indica desnivel de 3cm, ver detalle recubrimientos vigas y viguetas en zonas con desnivel de 3cm PL.N° 2404

EST - 2404-PD-P1

VERSIÓN PLANO V-01

OBRA No. 1157


CONSTRUCCIONES PLANIFICADAS
Carrera 13 No. 26A - 47 Piso 2
PBX: 339 41 11 Fax: 287 02 16


Robledales RESERVADO

CONTIENE:

NOMBRE DEL PROYECTO
ROBLEDALES-TORRE PALMERI 1

Dirección AK 7 134 06

DESPIECE VIGAS P2

ESCALA: INDICADA

| | |
|---|---|
| ARCHIVO: | 1157-EST-2404-PD-P1-DESPIECE VIGAS P2.DWG |
| FECHA: 26/01/2026 | DIBUJADO POR: KAREN CASTILLO |

DISEÑADOR ESTRUCTURAL
ROBERTO AYCARDI FONSECA
TP: 2520257258 CND

DISEÑADOR DE ELMENTOS NO ESTRUCTURALES
VICTOR H. DÁVILA F.
TP: 2520212278 2 CND

REVISOR ESTRUCTURAL
NICOLAS PARRA GARCIA
TP: 25202-62063 CND

CONSTRUCTOR RESPONSABLE
ALVARO DÍAZ ULLOA
TP: 2520275046 CND

CONSTRUCCIONES PLANIFICADAS

GERENTE DE DISEÑO

DIRECTOR DE ARQUITECTURA
ANDRÉS VALCARCEL

DIRECTOR DE INGENIERÍA
MARIO FERNANDO RIVERA

DIRECTOR DE PRESUPUESTOS
JAVIER CLAVIJO

EQUIPO DISEÑO CPSA

MP, CO, LL, EC.

MODIFICACIONES

| # | Fecha | Emitida por | Modificación |
|---|---|---|---|

VERSIONES DE PLANOS

| Versión | Fecha |
|---|---|
| V-01 | 26-01-2026 |

PROPÓSITO DE LA EMISIÓN

| | |
|---|---|
| DRAFT | |
| Coordinación Técnica | |
| Revisión | |
| Construcción | ✖ |
| Curaduría | |
| Presupuestos | |

| | |
|---|---|
| MODELO FUENTE: 1157_ROBL-BOG_VIV_ESTR_TP1 17/03/2026 | VERSIÓN MODELO: FASE III / V-03 |


EST - 2404-PD-P1

VERSIÓN PLANO V-01

OBRA No. 1157