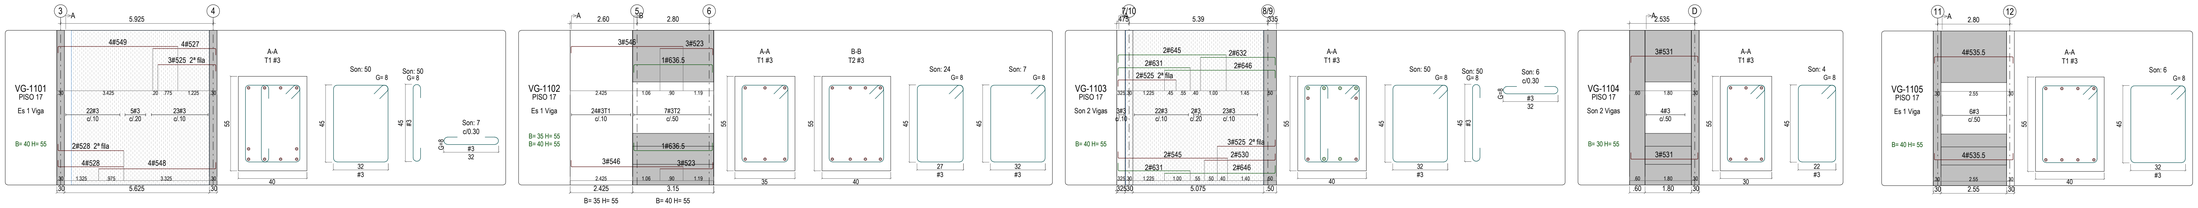

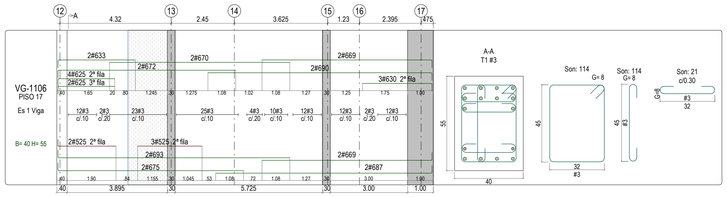

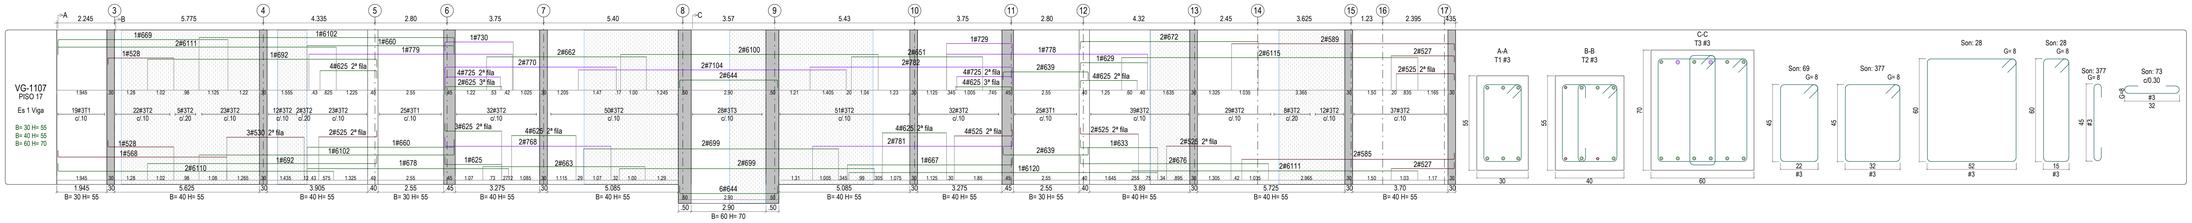

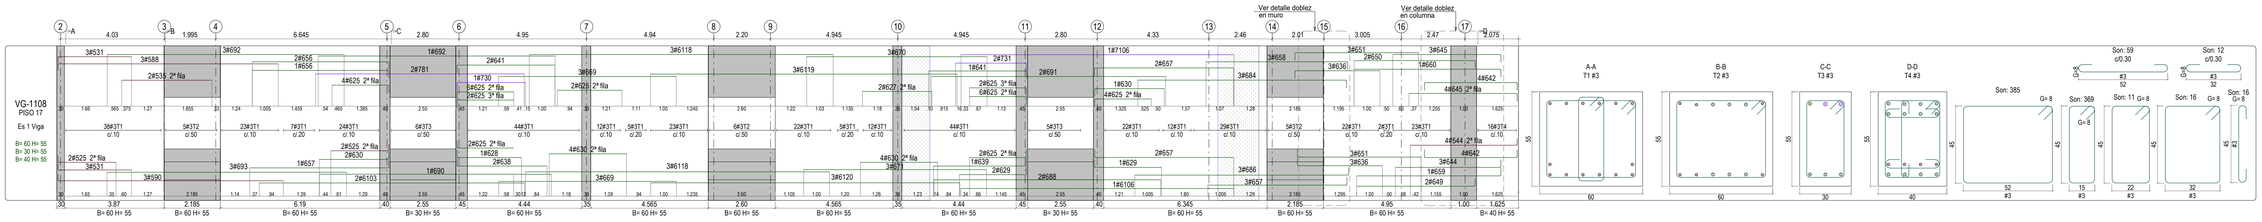

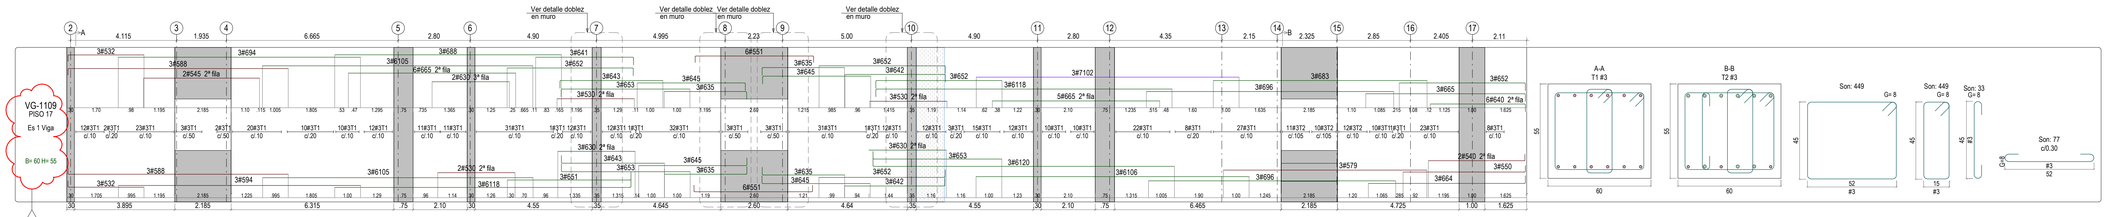

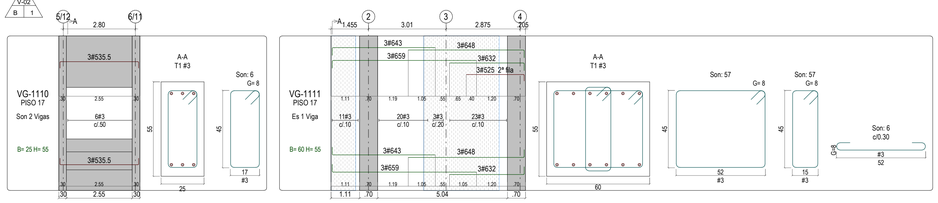

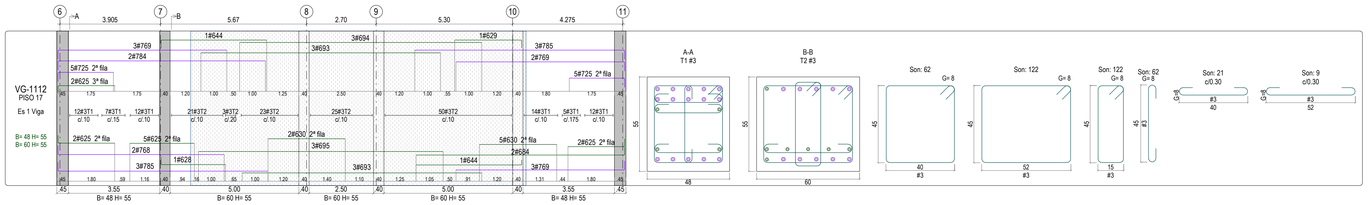

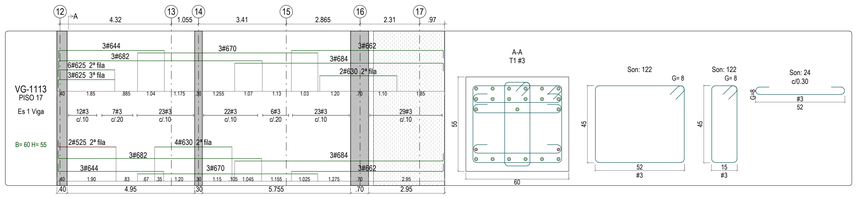

NOTAS

1. Ver detalles generales en el PL.N° 2002
2. Ver planta de piso 17 en el PL.N° 2575
3. Ver plano de localización de duchas y balcones en el PL.N° 2576
4. Ver detalles doblez en muro y en columna en el PL.N° 2575

CONVENCIONES

Indica desnivel de 3cm, ver detalle recubrimientos vigas y viguetas en zonas con desnivel de 3cm PL.N° 2576

EST - 2577-PD-P1

VERSIÓN PLANO V-02

OBRA No. 1157

CONSTRUCCIONES PLANIFICADAS
Carrera 13 No. 26A - 47 Piso 2
PBX: 339 41 11 Fax: 287 62 16

Robledales RESERVADO

CONTIENE:

NOMBRE DEL PROYECTO
ROBLEDALES-TORRE PALMERI 1

Dirección AK 7 134 06

DESPIECE VIGAS P17

ESCALA: INDICADA

ARCHIVO: 1157-EST-2577-PD-P1-DESPIECE VIGAS P17.DWG

FECHA:	DIBUJADO POR:
17/03/2026	KAREN CASTILLO

DISEÑADOR ESTRUCTURAL

ROBERTO AYCARDI FONSECA
TP: 2520572258 CND

DISEÑADOR DE ELMENTOS NO ESTRUCTURALES

VICTOR H. DÁVILA F.
TP: 2520122782 CND

REVISOR ESTRUCTURAL

NICOLAS PARRA GARCIA
TP: 252O2-62063 CND

CONSTRUCTOR RESPONSABLE

ALVARO DÍAZ ULLOA
TP: 2520275046 CND

CONSTRUCCIONES PLANIFICADAS

GERENTE DE DISEÑO

DIRECTOR DE ARQUITECTURA

ANDRÉS VALCARCEL

DIRECTOR DE INGENIERÍA

MARIO FERNANDO RIVERA

DIRECTOR DE PRESUPUESTOS

JAVIER CLAVIJO

EQUIPO DISEÑO CPSA

MP, CO, LL, EC.

MODIFICACIONES

#	Fecha	Emitida por	Modificación
1	17/03/2026	B	Se adiciona refuerzo en voladizos atendiendo obs. de rev externo

VERSIONES DE PLANOS

Versión	Fecha
V-01	02-03-2026
V-02	17-03-2026

PROPÓSITO DE LA EMISIÓN

DRAFT	
Coordinación Técnica	
Revisión	
Construcción	✖
Curaduría	
Presupuestos	

MODELO FUENTE:	VERSIÓN MODELO:
1157_ROBL-BOG_VIV_ESTR_TP1 17/03/2026	FASE III / V-03

EST - 2577-PD-P1

VERSIÓN PLANO V-02

OBRA No. 1157