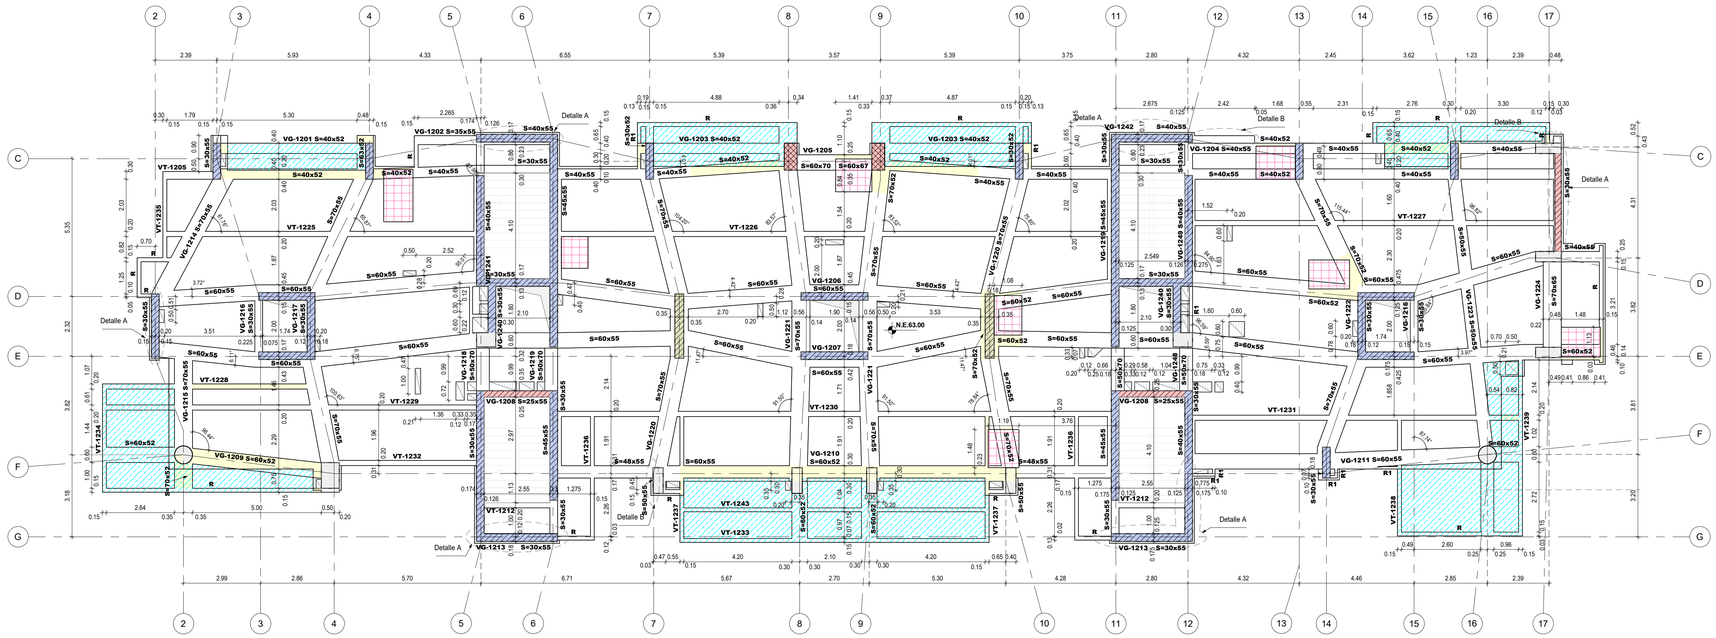

PLANTA DE PISO 18_NE(+63.00)
Escala 1 : 100

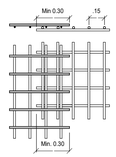

DETALLE TRASLAPO DE MALLAS
Escala 1 : 25

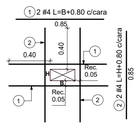

DETALLE DE VACÍOS
Escala 1 : 25

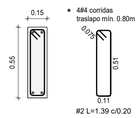

RIOSTRA 15X55 (R)
Escala 1 : 20

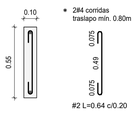

RIOSTRA 10X55 (R1)
Escala 1 : 20

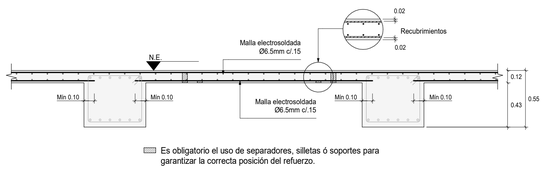

Es obligatorio el uso de separadores, silletas ó soportes para garantizar la correcta posición del refuerzo.

CORTE TÍPICO PLACA e=0.12
Escala 1 : 25

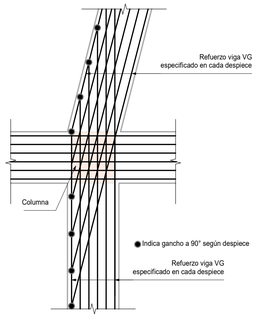

PLANTA

DETALLE DE DOBLEZ EN COLUMNA
Escala 1 : 25

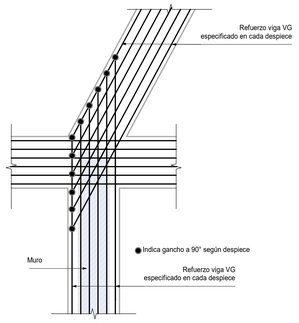

PLANTA

DETALLE DE DOBLEZ EN MURO
Escala 1 : 25

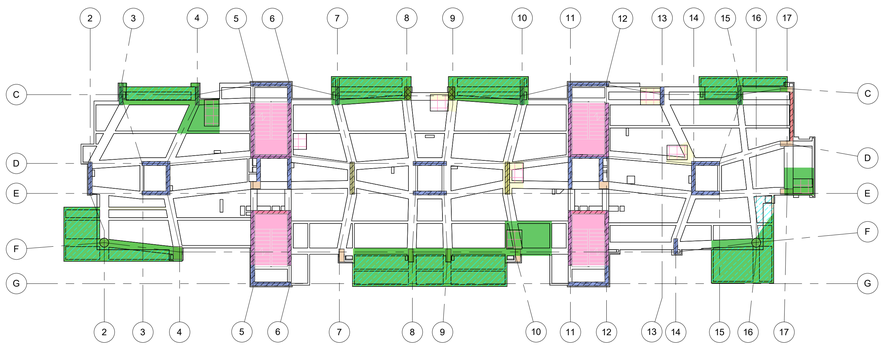

CONVENCIONES CARGA VIVA
Indica carga viva 300 Kg/m²
Indica carga viva 500 Kg/m²
Indica carga viva 180 Kg/m²

PLANTA DE PISO 18_NE(+63.00)-CARGAS VIVAS
Escala 1 : 200

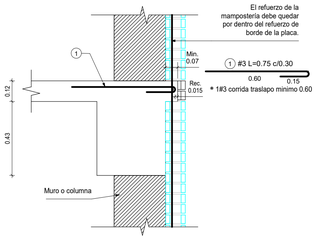

DETALLE A
Escala 1 : 15

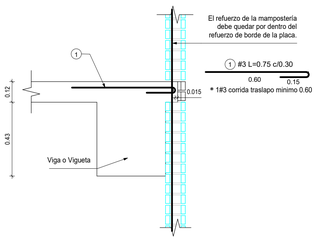

DETALLE B
Escala 1 : 15

CONCRETO
f'c=28 MPa
f'c=280 kg/cm²
f'c=4000 psi

CONVENCIONES	
	Indica muros e=0.25m
	Indica muros e=0.30m
	Indica muros e=0.35m
	Indica muros e=0.50m
	Indica columnas S=40x100
	Indica columnas S=70x100
	Indica columnas S=75x55
	Indica columnas S=Ø70
	Indica columnas que mueren
	Indica vigas
000	Indica N° de viga

NOTAS

1. Ver detalles generales en el PL.N° 2002
2. Ver despieces de vigas en los PL.N° 2602 - PL.N° 2604
3. Todas las vigas que se encuentren en el desnivel de -0.03m por presencia de duchas o balcones son de h=52
4. Ver plano de localización de Duchas y balcones en PL.N° 2601
5. Prever riostras para apoyo superior de ventanería piso a techo de los balcones, las cuales se fundirán en conjunto con la placa y vigas de cada entrepiso.

EST - 2600-PP-P1
VERSIÓN PLANO V-01
OBRA No. 1157

CONSTRUCCIONES PLANIFICADAS
Carrera 13 No. 26A - 47 Piso 2
PBX: 339 41 11 Fax: 287 02 16

Robledales RESERVADO

CONTIENE:

NOMBRE DEL PROYECTO
ROBLEDALES-TORRE PALMERI 1

Dirección AK 7 134 06

PLANTA PISO 18

ESCALA: INDICADA

ARCHIVO:	1157-EST-2600-PP-P1-PLANTA PISO 18.DWG
FECHA: 02/03/2026	DIBUJADO POR: KAREN CASTILLO

DISEÑADOR ESTRUCTURAL
ROBERTO AYCARDI FONSECA
TP: 2520257258 CND

DISEÑADOR DE ELMENTOS NO ESTRUCTURALES
VICTOR H. DÁVILA F.
TP: 2520122782 CND

REVISOR ESTRUCTURAL
NICOLAS PARRA GARCIA
TP: 25202-62063 CND

CONSTRUCTOR RESPONSABLE
ALVARO DÍAZ ULLOA
TP: 2520275046 CND

CONSTRUCCIONES PLANIFICADAS
GERENTE DE DISEÑO
DIRECTOR DE ARQUITECTURA
ANDRÉS VALCARCEL
DIRECTOR DE INGENIERÍA
MARIO FERNANDO RIVERA
DIRECTOR DE PRESUPUESTOS
JAVIER CLAVIJO

EQUIPO DISEÑO CPSA
MP, CO, LL, EC.

MODIFICACIONES

#	Fecha	Emitida por	Modificación

VERSIONES DE PLANOS

Versión	Fecha
V-01	02-03-2026

PROPÓSITO DE LA EMISIÓN

DRAFT	
Coordinación Técnica	
Revisión	
Construcción	✖
Curaduría	
Presupuestos	

MODELO FUENTE: 1157_ROBL-BOG_VIV_ESTR_TP1 17/03/2026	VERSIÓN MODELO: FASE III / V-03

EST - 2600-PP-P1
VERSIÓN PLANO V-01
OBRA No. 1157