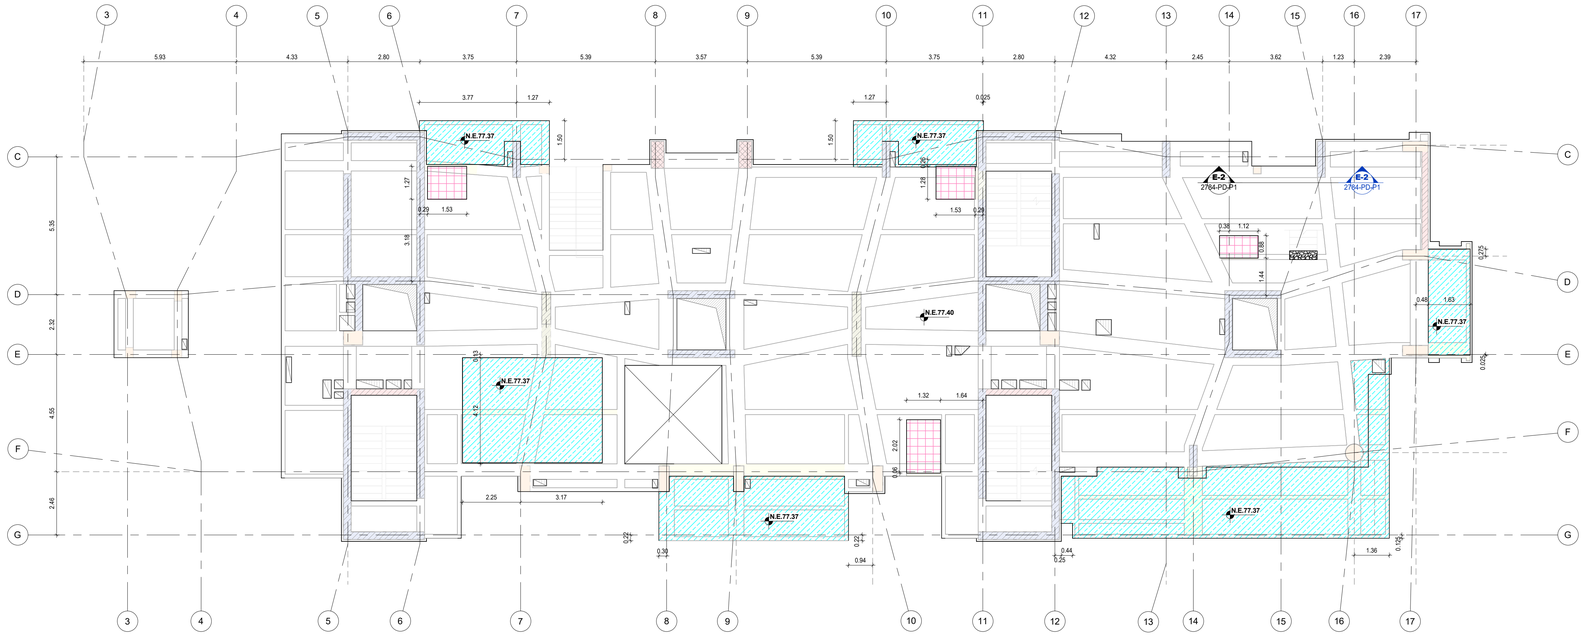

PLANTA LOCALIZACIÓN DE DUCHAS PISO 22 NE(+77.40)
Escala 1 : 100

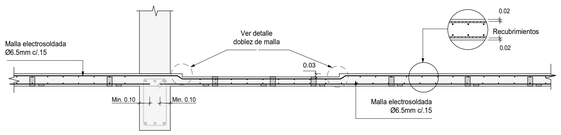

CORTE TÍPICO DE PLACA ZONA DE DUCHAS
Escala 1 : 25

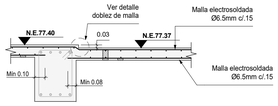

CORTE TÍPICO DE PLACA e=0.12 con paso a PLACA e=0.12 EN APOYO VIGA
Escala 1 : 25

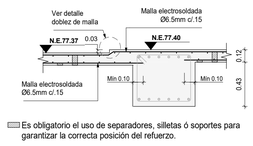

CORTE TÍPICO DE PLACA e=0.12 con paso a PLACA e=0.12 EN APOYO PLACA
Escala 1 : 25

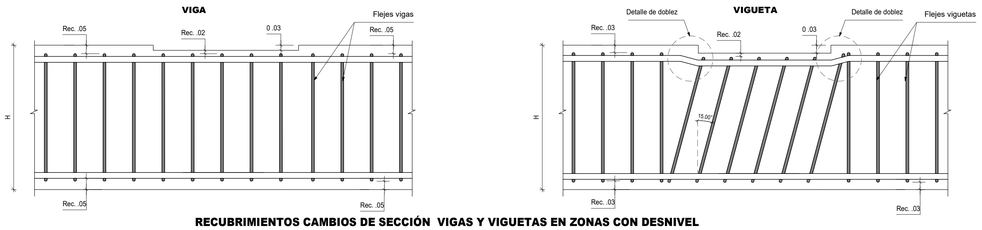

RECUBRIMIENTOS CAMBIOS DE SECCIÓN VIGAS Y VIGUETAS EN ZONAS CON DESNIVEL

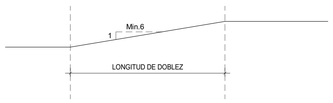

DETALLE DE DOBLEZ DE MALLA Y VARILLA
Escala 1 : 10

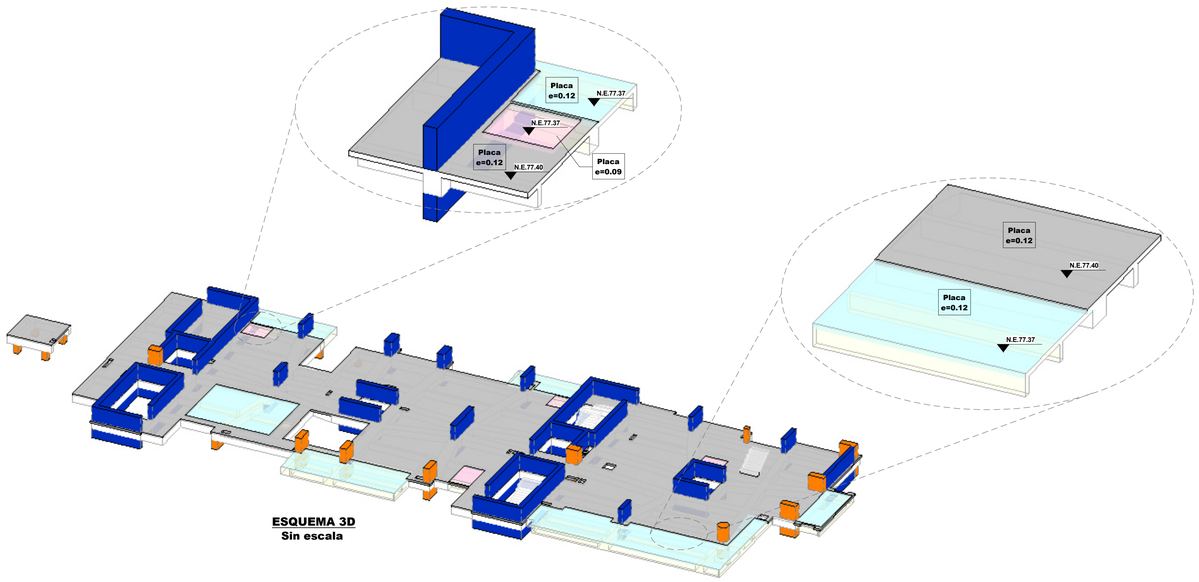

ESQUEMA 3D
Sin escala

CONCRETO
f'c=28 MPa
f'c=280 kg/cm²
f'c=4000 psi

CONVENCIONES

- Indica muros e=0.25m
- Indica muros e=0.30m
- Indica muros e=0.35m
- Indica muros e=0.50m
- Indica columnas S=40x100
- Indica columnas S=70x100
- Indica columnas S=75x55
- Indica columnas S=Ø70
- Indica columnas que mueren
- Indica vigas
- 000 Indica N° de viga

NOTAS

1. Ver detalles generales en el PL.N° 2002
2. Ver despieces de vigas en los PL.N° 2702 - PL.N° 2704
3. Todas las vigas que se encuentren en el desnivel de -0.03m por presencia de duchas o balcones son de h=52.

EST - 2701-PP-P1
VERSIÓN PLANO V-01
OBRA No. 1157

CONSTRUCCIONES PLANIFICADAS
Carrera 13 No. 26A - 47 Piso 2
PBX: 339 41 11 Fax: 287 62 16

Robledales RESERVADO

CONTIENE:

NOMBRE DEL PROYECTO
ROBLEDALES-TORRE PALMERI 1

Dirección AK 7 134 06

PLANTA DUCHAS PISO 22

ESCALA: INDICADA

ARCHIVO: 1157-EST-2701-PP-P1-PLANTA DUCHAS PISO 22.DWG
FECHA: 02/03/2026
DIBUJADO POR: KAREN CASTILLO

DISEÑADOR ESTRUCTURAL
ROBERTO AYCARDI FONSECA
TP: 2520257258 CND

DISEÑADOR DE ELMENTOS NO ESTRUCTURALES
VICTOR H. DÁVILA F.
TP: 2520122782 CND

REVISOR ESTRUCTURAL
NICOLAS PARRA GARCIA
TP: 25202-62063 CND

CONSTRUCTOR RESPONSABLE
ALVARO DÍAZ ULLOA
TP: 2520275046 CND

CONSTRUCCIONES PLANIFICADAS
GERENTE DE DISEÑO
DIRECTOR DE ARQUITECTURA
ANDRÉS VALCARCEL
DIRECTOR DE INGENIERÍA
MARIO FERNANDO RIVERA
DIRECTOR DE PRESUPUESTOS
JAVIER CLAVIJO

EQUIPO DISEÑO CPSA
MP, CO, LL, EC.

MODIFICACIONES

#	Fecha	Emitida por	Modificación

VERSIONES DE PLANOS

Versión	Fecha
V-01	02-03-2026

PROPÓSITO DE LA EMISIÓN

DRAFT	
Coordinación Técnica	
Revisión	
Construcción	✖
Curaduría	
Presupuestos	

MODELO FUENTE: 1157_ROBL-BOG_VIV_ESTR_TP1 17/03/2026
VERSIÓN MODELO: FASE III / V-03

EST - 2701-PP-P1
VERSIÓN PLANO V-01
OBRA No. 1157