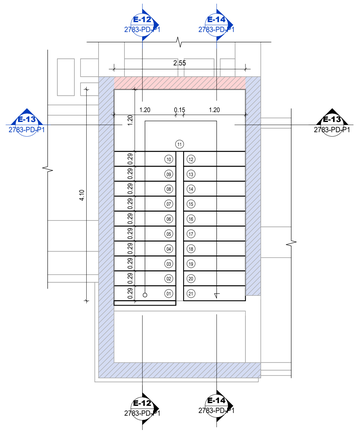

PLANTA DE ESCALERAS PISO TIPO
Escala 1 : 50

V-02
B 1

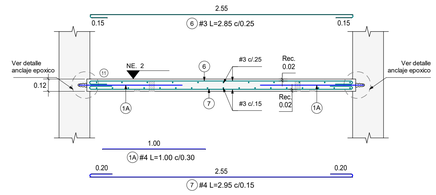

Es obligatorio el uso de separadores, silletas ó soportes para garantizar la correcta posición del refuerzo.

CORTE E-13
Escala 1 : 25

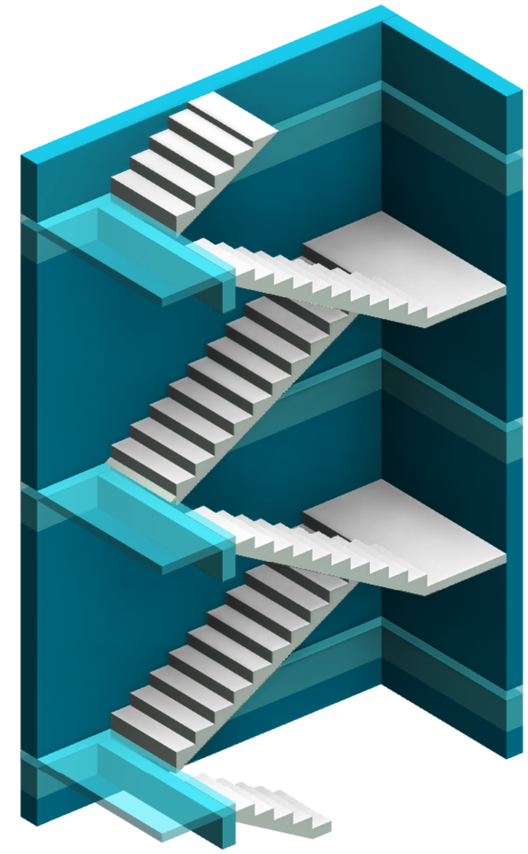

ESQUEMA 3D ESCALERA
Sin escala

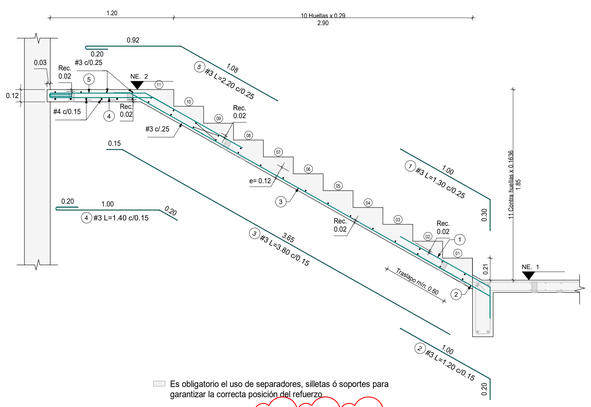

Es obligatorio el uso de separadores, silletas ó soportes para garantizar la correcta posición del refuerzo.

CORTE E-12
Escala 1 : 25

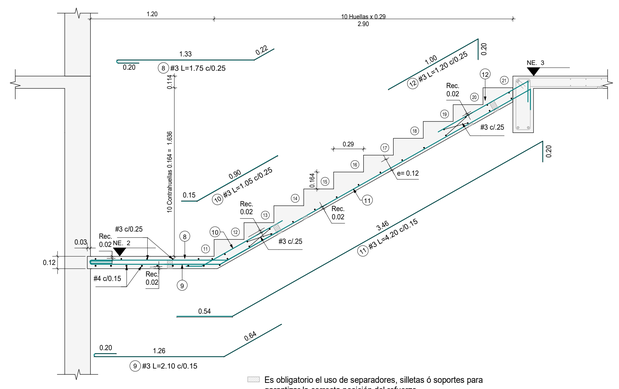

Es obligatorio el uso de separadores, silletas ó soportes para garantizar la correcta posición del refuerzo.

CORTE E-14
Escala 1 : 25

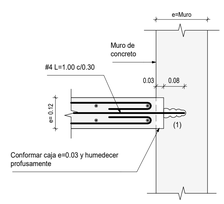

(1) Indica anclar con epóxico estructural
Indica caja de 3cm de profundidad

DETALLE ANCLAJE EPOXICO
Escala 1 : 10

NIVELES ESCALERA TIPO 1 DE PISO 2 A...

Piso	NE.1	NE.2	NE.3
PISO 02_NE(+5.40)	5.40	7.25	9.00
PISO 03_NE(+9.00)	9.00	10.85	12.60
PISO 04_NE(+12.60)	12.60	14.45	16.20
PISO 05_NE(+16.20)	16.20	18.05	19.80
PISO 06_NE(+19.80)	19.80	21.65	23.40
PISO 07_NE(+23.40)	23.40	25.25	27.00
PISO 08_NE(+27.00)	27.00	28.85	30.60
PISO 09_NE(+30.60)	30.60	32.45	34.20
PISO 10_NE(+34.20)	34.20	36.05	37.80
PISO 11_NE(+37.80)	37.80	39.65	41.40
PISO 12_NE(+41.40)	41.40	43.25	45.00
PISO 13_NE(+45.00)	45.00	46.85	48.60
PISO 14_NE(+48.60)	48.60	50.45	52.20
PISO 15_NE(+52.20)	52.20	54.05	55.80
PISO 16_NE(+55.80)	55.80	57.65	59.40
PISO 17_NE(+59.40)	59.40	61.25	63.00
PISO 18_NE(+63.00)	63.00	64.85	66.60
PISO 19_NE(+66.60)	66.60	68.45	70.20
PISO 20_NE(+70.20)	70.20	72.05	73.80
PISO 21 NE(+73.80)	73.80	75.65	77.40
PISO 22_NE(+77.40)	77.40	79.25	81.00
PISO 23_NE(+81.00)	81.00	82.85	84.60

CONCRETO

f'c=21 MPa
f'c=210 kg/cm²
f'c=3000 psi

CONVENCIONES

Indica muros e=0.25m
Indica muros e=0.30m

NOTAS

1. Ver detalles generales en el PL.N° 2002

EST - 2783-PD-P1
VERSIÓN PLANO V-02
OBRA No. 1157

CONSTRUCCIONES PLANIFICADAS
Carrera 13 No. 26A - 47 Piso 2
PBX: 339 41 11 Fax: 287 62 16

Robledales
RESERVADO

CONTIENE:

NOMBRE DEL PROYECTO
ROBLEDALES-TORRE PALMERI 1

Dirección AK 7 134 06

DESPIECE ESCALERA TIPO 1 PISOS TIPO

ESCALA: INDICADA

ARCHIVO: EST-2783-PD-P1-DESPIECE ESCALERA TIPO 1 PISOS TIPO.DWG

FECHA:	DIBUJADO POR:
17/03/2026	KAREN CASTILLO

DISEÑADOR ESTRUCTURAL
ROBERTO AYCARDI FONSECA
TP: 2520257258 CND

DISEÑADOR DE ELMENTOS NO ESTRUCTURALES
VICTOR H. DÁVILA F.
TP: 2520122782 CND

REVISOR ESTRUCTURAL
NICOLAS PARRA GARCIA
TP: 25202-62063 CND

CONSTRUCTOR RESPONSABLE
ALVARO DÍAZ ULLOA
TP: 2520275046 CND

CONSTRUCCIONES PLANIFICADAS

GERENTE DE DISEÑO

DIRECTOR DE ARQUITECTURA
ANDRÉS VALCARCEL

DIRECTOR DE INGENIERÍA
MARIO FERNANDO RIVERA

DIRECTOR DE PRESUPUESTOS
JAVIER CLAVIJO

EQUIPO DISEÑO CPSA
MP, CO, LL, EC.

MODIFICACIONES

#	Fecha	Emitida por	Modificación
1	17/03/2026	B	Actualización General de refuerzo escalera

VERSIONES DE PLANOS

Versión	Fecha
V-01	11-03-2026
V-02	17-03-2026

PROPÓSITO DE LA EMISIÓN

DRAFT	
Coordinación Técnica	
Revisión	
Construcción	✖
Curaduría	
Presupuestos	

MODELO FUENTE: 1157_ROBL-BOG_VIV_ESTR_TP1
17/03/2026

VERSIÓN MODELO: FASE III / V-03

EST - 2783-PD-P1
VERSIÓN PLANO V-02
OBRA No. 1157