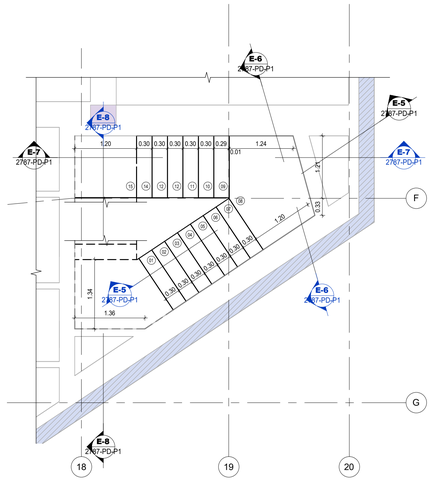

PLANTA ARRANQUE DE ESCALERA TIPO 3 DE SOT 1 A PISO 1
Escala 1 : 50

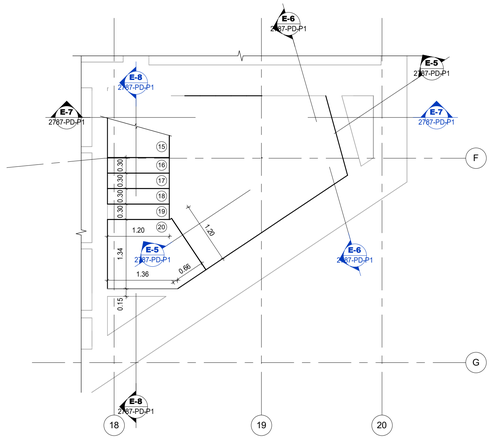

PLANTA LLEGADA ESCALERA TIPO 3 DE SOT 1 A PISO 01_NE(+0.00)
Escala 1 : 50

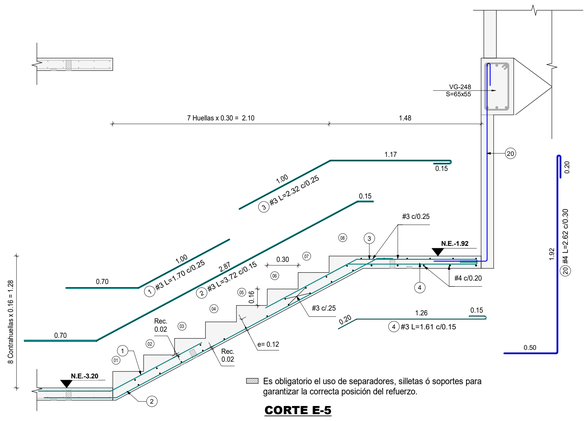

Es obligatorio el uso de separadores, silletas ó soportes para garantizar la correcta posición del refuerzo.

CORTE E-5
Escala 1 : 25

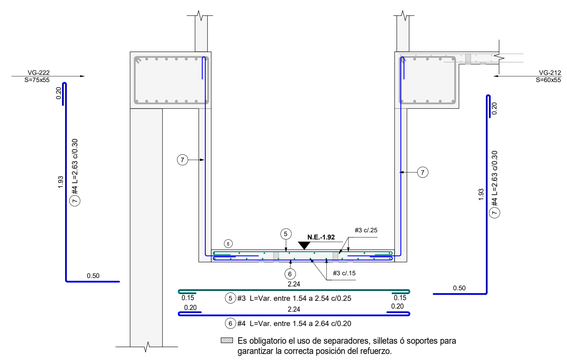

Es obligatorio el uso de separadores, silletas ó soportes para garantizar la correcta posición del refuerzo.

CORTE E-6
Escala 1 : 25

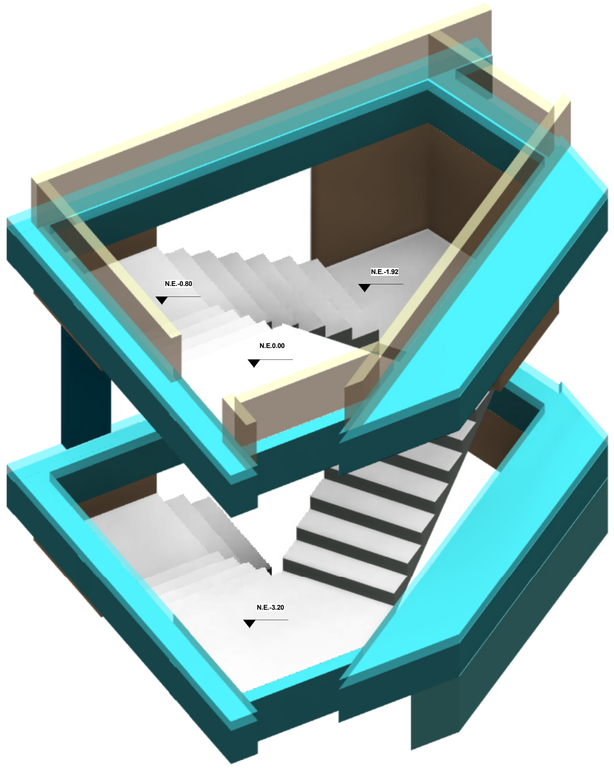

ESQUEMA 3D
Sin escala

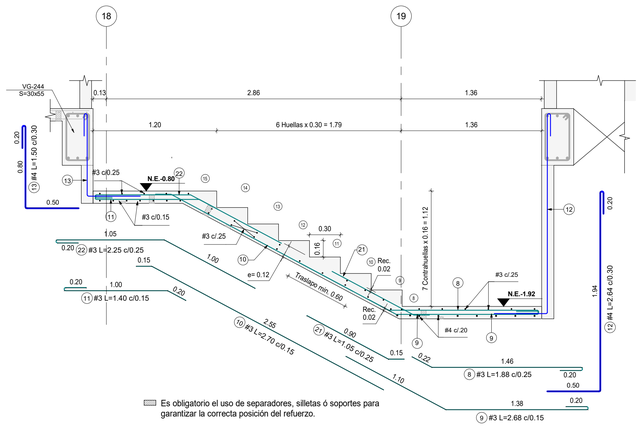

Es obligatorio el uso de separadores, silletas ó soportes para garantizar la correcta posición del refuerzo.

CORTE E-7
Escala 1 : 25

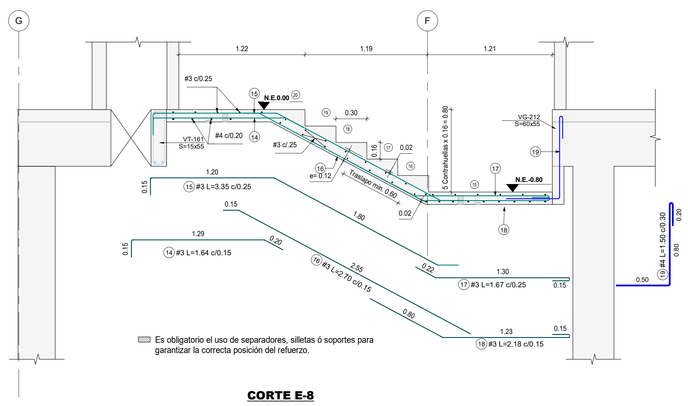

Es obligatorio el uso de separadores, silletas ó soportes para garantizar la correcta posición del refuerzo.

CORTE E-8
Escala 1 : 25

CONCRETO
f'c=21 MPa
f'c=210 kg/cm²
f'c=3000 psi
CONVENCIONES
Indica muros e=0.25m
Indica muros e=0.30m
NOTAS
1. Ver detalles generales en el PL.N° 2002

EST - 2787-PD-P1
VERSIÓN PLANO V-01
OBRA No. 1157

CONSTRUCCIONES PLANIFICADAS
Carrera 13 No. 26A - 47 Piso 2
PBX: 339 41 11 Fax: 287 02 16

Robledales RESERVADO

CONTIENE:

NOMBRE DEL PROYECTO
ROBLEDALES-TORRE PALMERI 1

Dirección AK 7 134 06

DESPIECE ESCALERA TIPO 3 SOT 1 A PISO 1

ESCALA: INDICADA

ARCHIVO: 2787-PD-P1-DESPIECE ESCALERA TIPO 3 SOT 1 A PISO 1.DWG

FECHA:	DIBUJADO POR:
17/03/2026	ANDRES DUARTE

DISEÑADOR ESTRUCTURAL
ROBERTO AYCARDI FONSECA
TP: 2520257258 CND

DISEÑADOR DE ELMENTOS NO ESTRUCTURALES
VICTOR H. DÁVILA F.
TP: 25202122782 CND

REVISOR ESTRUCTURAL
NICOLAS PARRA GARCIA
TP: 25202-62063 CND

CONSTRUCTOR RESPONSABLE
ALVARO DÍAZ ULLOA
TP: 2520275046 CND

CONSTRUCCIONES PLANIFICADAS

GERENTE DE DISEÑO

DIRECTOR DE ARQUITECTURA
ANDRÉS VALCARCEL

DIRECTOR DE INGENIERÍA
MARIO FERNANDO RIVERA

DIRECTOR DE PRESUPUESTOS
JAVIER CLAVIJO

EQUIPO DISEÑO CPSA
MP, CO, LL, EC.

MODIFICACIONES

#	Fecha	Emitida por	Modificación

VERSIONES DE PLANOS

Versión	Fecha
V-01	17-03-2026

PROPÓSITO DE LA EMISIÓN

DRAFT	
Coordinación Técnica	
Revisión	
Construcción	X
Curaduría	
Presupuestos	

MODELO FUENTE:	VERSIÓN MODELO:
1157_ROBL-BOG_VIV_ESTR_TP1 17/03/2026	FASE III / V-03

EST - 2787-PD-P1
VERSIÓN PLANO V-01
OBRA No. 1157