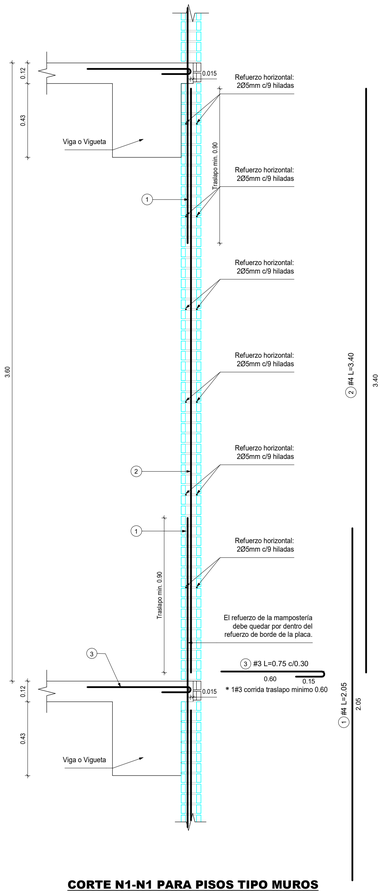

CORTE N1-N1 PARA PISOS TIPO MUROS DE FACHADA LADRILLO TOLETE
Escala 1 : 15

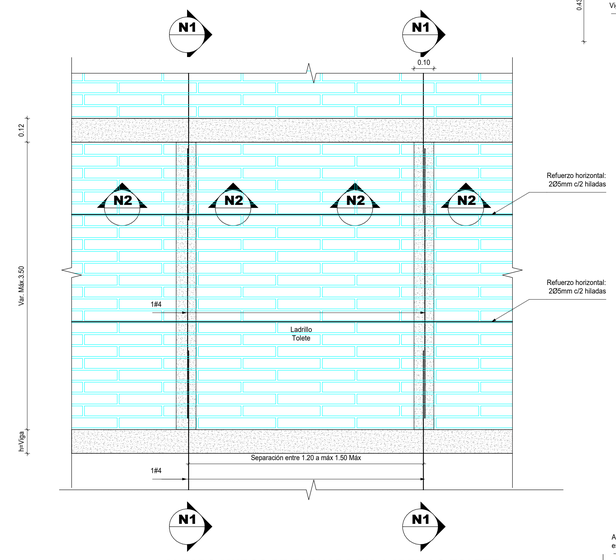

ALZADO MUROS DE FACHADA EN LADRILLO TOLETE
Escala 1 : 13

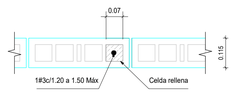

CORTE N2-N2 LADRILLO TOLETE
Escala 1 : 10

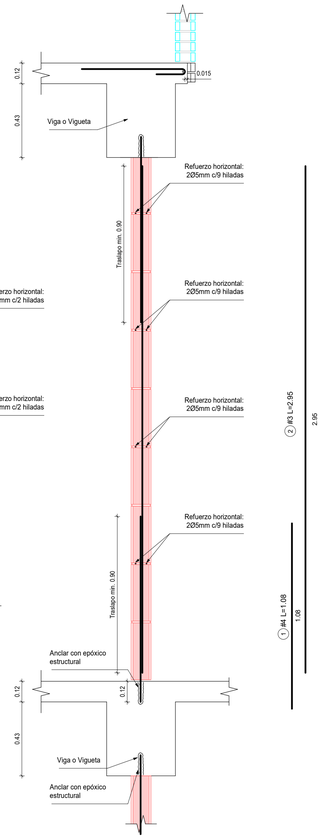

CORTE N3-N3 MUROS INTERNOS EN BLOQUE N° 5
Escala 1 : 15

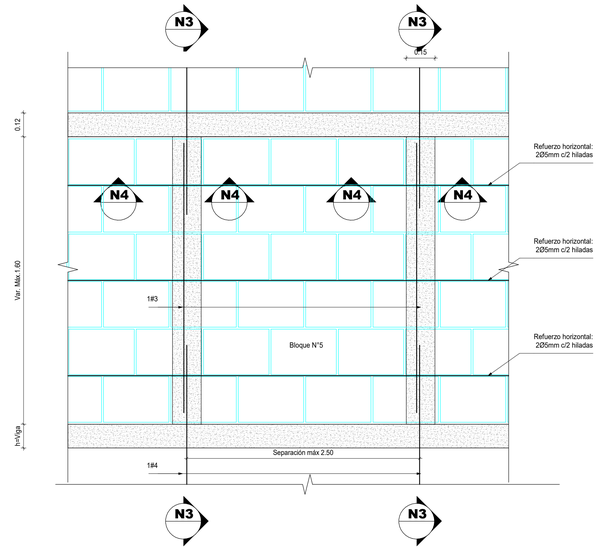

ALZADO MUROS INTERNOS EN BLOQUE N° 5
Escala 1 : 13

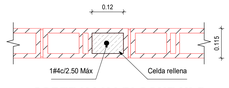

CORTE N4-N4 BLOQUE N° 5
Escala 1 : 10

ESPECIFICACIONES

1. El mortero de pega se hará según la siguiente disposición:

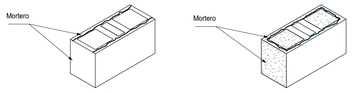

CASO TÍPICO **CASO DE CELDA RELLENAS**

2. Las juntas verticales y horizontales son de 10 mm. con tolerancia de 3 mm.
3. Toda celda reforzada debe llevar ventana de limpieza
4. El mortero de relleno lleva agregado máximo de 3/8"

MUROS NO ESTRUCTURALES DE MAMPOSTERÍA

f'cr (kg/cm²)	f'cp (kg/cm²)	f'm (kg/cm²)
Resistencia última a la compresión del mortero de relleno	Resistencia última a la compresión del mortero de pega	Resistencia mínima a la compresión del murete en mampostería
100	100	80

• Las resistencias deben comprobarse mediante ensayos ejecutados de acuerdo con las normas colombianas de diseño y construcción sismo-resistente (NRS-10)

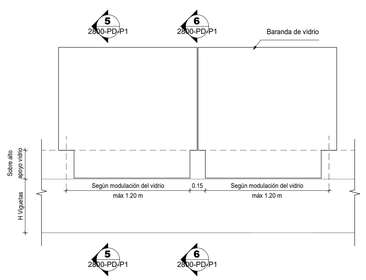

DETALLE DE BARANDA
Escala 1 : 25

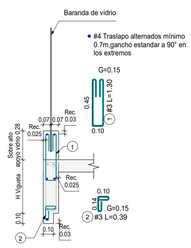

CORTE 5-5
Escala 1 : 25

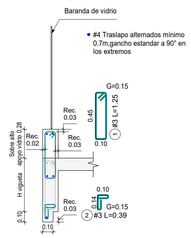

CORTE 6-6
Escala 1 : 25

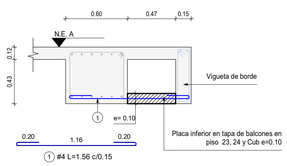

DETALLES NICHOS FACHADAS Y VENTANAS
Escala 1 : 25

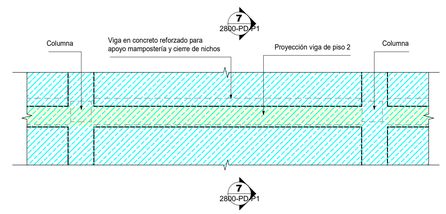

PLANTA TÍPICA NICHOS EN FACHADA
Escala 1 : 50

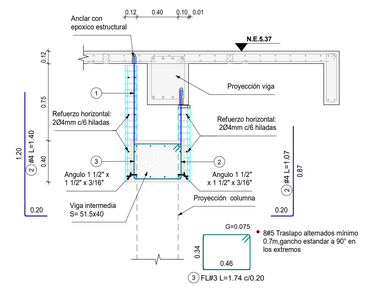

CORTE 3-3
Escala 1 : 25

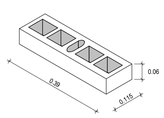

LADRILLO TOLETE GRAN FORMATO RUGOSO
Escala 1 : 10

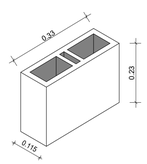

LADRILLO ESTRUCTURAL BLOQUE N°5
Escala 1 : 10

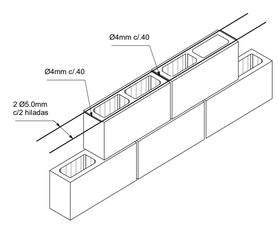

REFUERZO HORIZONTAL TÍPICO MUROS e=0.12
Sin escala

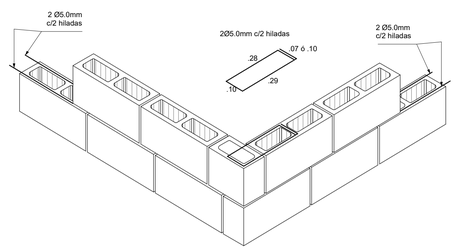

NOES-REFUERZO HORIZONTAL TÍPICO PARA ESQUINA MUROS e=0.12
Sin escala

CONVENCIONES
- Indica Mortero de relleno
- Indica Concreto

Grado de desempeño: **BAJO**

NOTAS:
1. Se debe hacer la planificacion de las redes antes de ejecutar la construccion de los muros no estructurales.

NOTA:
Este plano debe ser revisado y aprobado por el Constructor del proyecto.

V°B° CONSTRUCTOR:

EST - 2800-PD-P1
VERSIÓN PLANO V-01
OBRA No. 1157

CONSTRUCCIONES PLANIFICADAS
Carrera 13 No. 26A - 47 Piso 2
PBX: 339 41 11 Fax: 287 62 16

Robledales RESERVADO

CONTIENE:

NOMBRE DEL PROYECTO
ROBLEDALES-TORRE PALMERI 1

Dirección AK 7 134 06

DETALLES MUROS NO ESTRUCTURALES

ESCALA: INDICADA

ARCHIVO: EST-2800-PD-P1-DETALLES MUROS NO ESTRUCTURALES.DWG

FECHA:	DIBUJADO POR:
23/12/2025	ANDRES DUARTE

DISEÑADOR ESTRUCTURAL
ROBERTO AYCARDI FONSECA
TP: 2520257258 CND

DISEÑADOR DE ELMENTOS NO ESTRUCTURALES
VICTOR H. DÁVILA F.
TP: 25202122782 CND

REVISOR ESTRUCTURAL
NICOLAS PARRA GARCIA
TP: 25202-62063 CND

CONSTRUCTOR RESPONSABLE
ALVARO DÍAZ ULLOA
TP: 2520275046 CND

CONSTRUCCIONES PLANIFICADAS

GERENTE DE DISEÑO

DIRECTOR DE ARQUITECTURA
ANDRÉS VALCARCEL

DIRECTOR DE INGENIERÍA
MARIO FERNANDO RIVERA

DIRECTOR DE PRESUPUESTOS
JAVIER CLAVIJO

EQUIPO DISEÑO CPSA
MP, CO, LL, EC.

MODIFICACIONES

#	Fecha	Emitida por	Modificación

VERSIONES DE PLANOS

Versión	Fecha

PROPÓSITO DE LA EMISIÓN

DRAFT	
Coordinación Técnica	
Revisión	
Construcción	✖
Curaduría	
Presupuestos	

MODELO FUENTE: 1157_ROBL-BOG_VIV_ESTR_TP1
17/03/2026

VERSIÓN MODELO: FASE III / V-03

EST - 2800-PD-P1
VERSIÓN PLANO V-01
OBRA No. 1157